


โครงการก่อสร้าง อาคารพักอาศัย คสล. ๑ ชั้น

รหัส (M1) 98

เจ้าของโครงการ

คุณปรินทร์ เรืองรัตนวาณิช

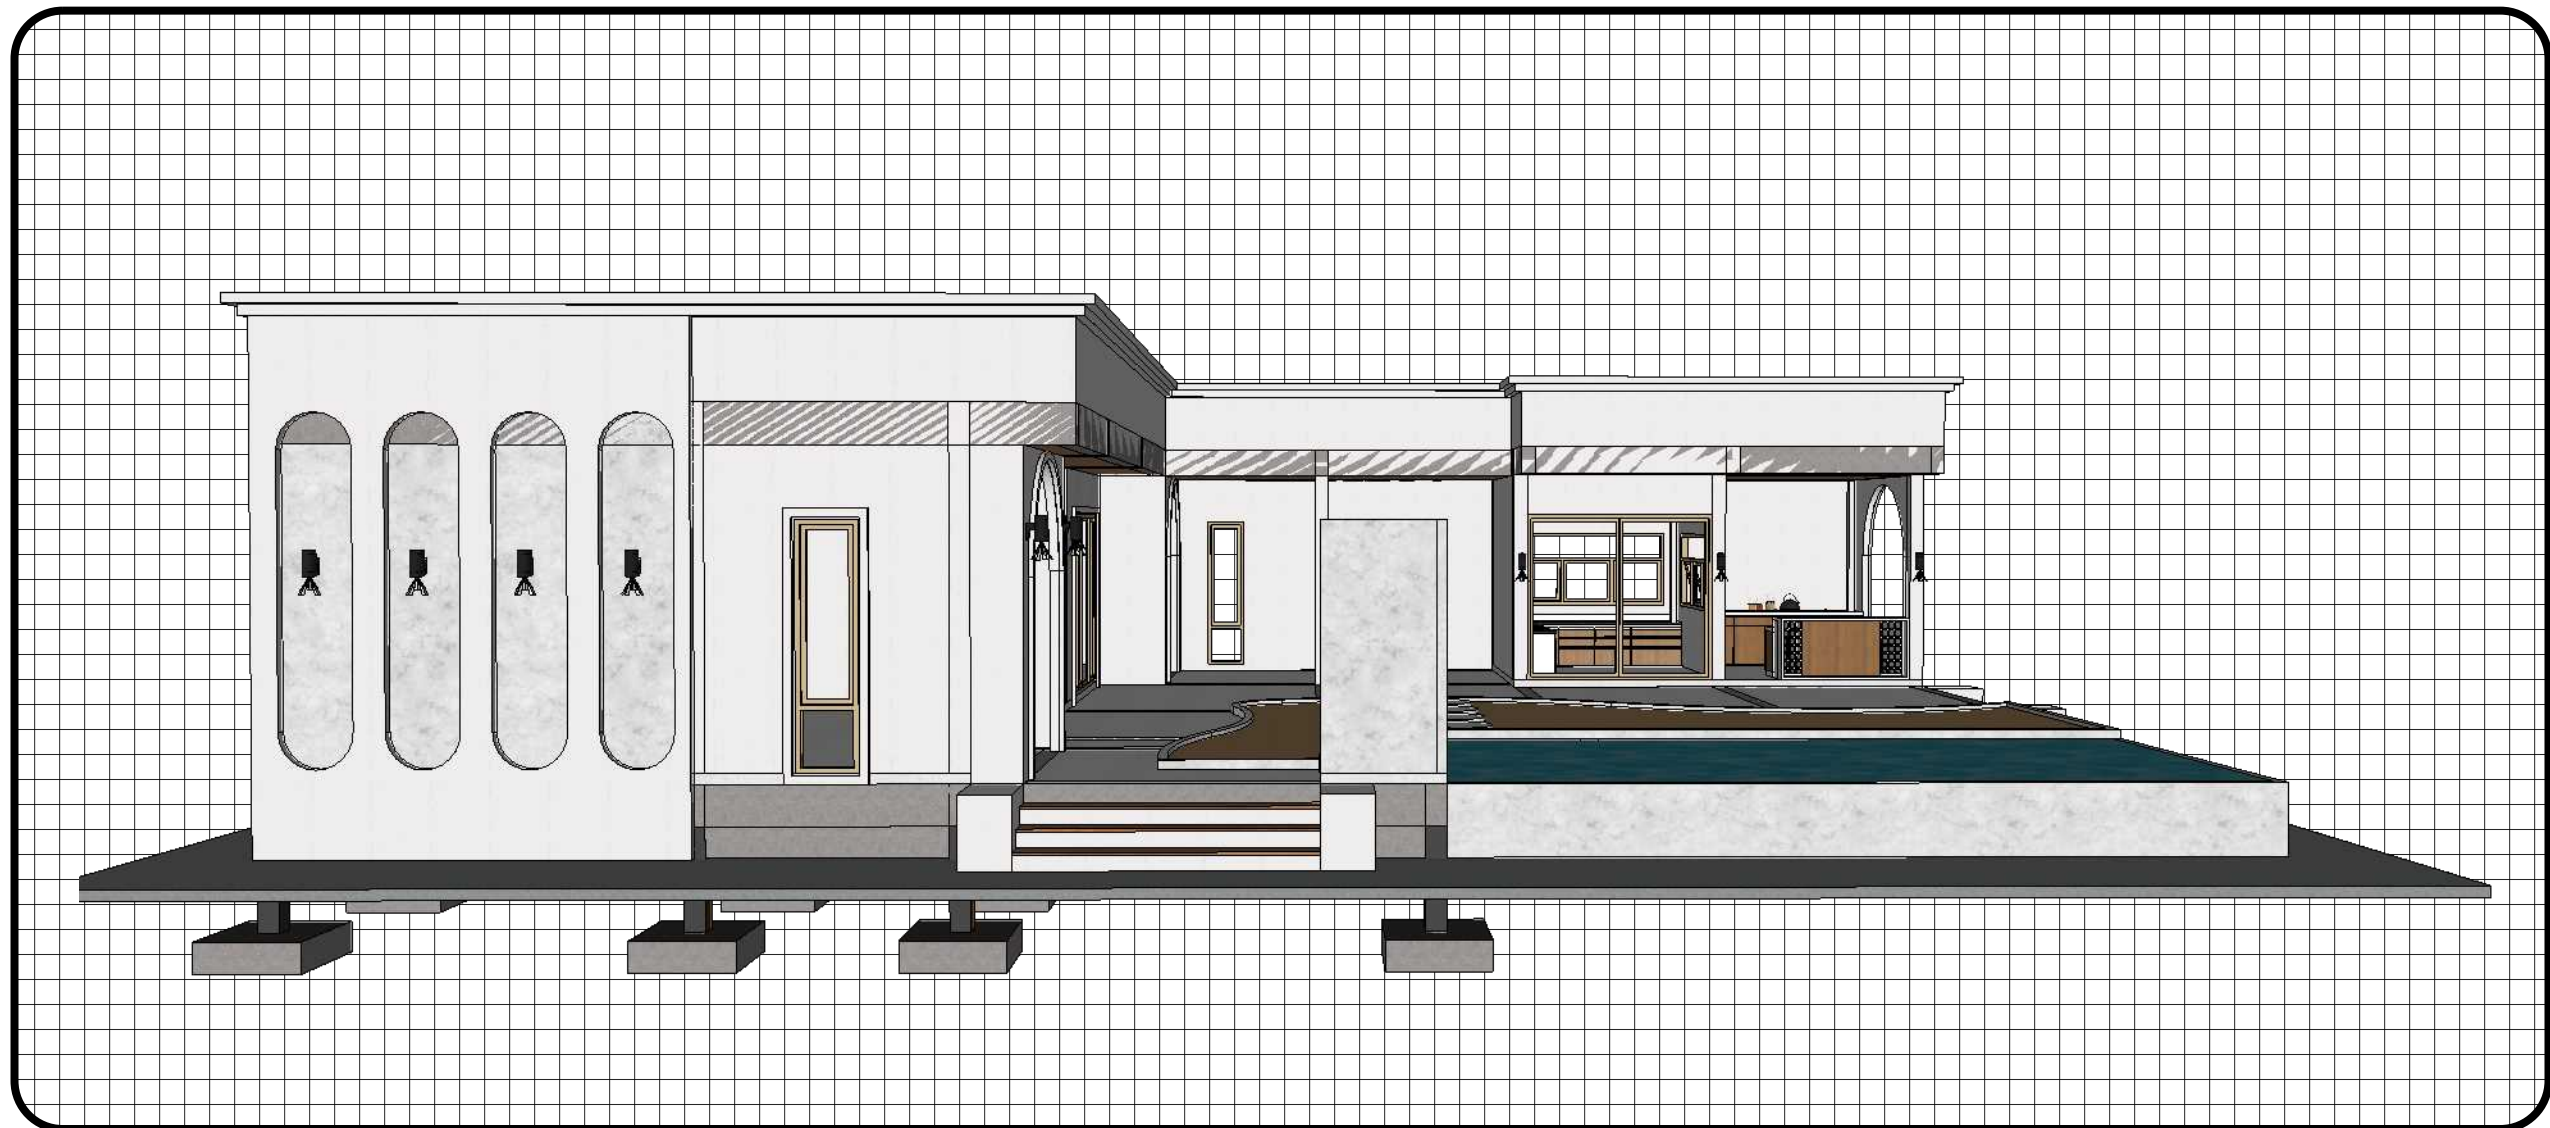

CH.THANAKRIT DESIGN

081-387-9527

ID LINE : jp_pt_


สถานที่ก่อสร้าง
บ้านไม้ขาว
ตำบล ป่าตอง
อำเภอ กะทู้
จังหวัดภูเก็ต

หลังคาเมทัลชีท

ชื่อโครงการ	
โครงการก่อสร้างอาคารพักอาศัย คสล. 1 ชั้น	
เจ้าของโครงการ	
คุณปรินทร์ เรืองรัตนวานิช	
สถาปนิก	
..... นายนิกร สุขแสง ภสถ.10581 ถ.แจ้งวัฒนะซอย6 แขวงตลาดบางเขน. เขตหลักสี่. กรุงเทพฯ	
วิศวกรโครงสร้าง	
..... นายปฐวี เชื้อชม ภย.33663 92 ม. 1 ต.ท่าโพธิ์ศรี อ.เดชอุดม จ.อุบลราชธานี	
วิศวกรไฟฟ้า	
-	
วิศวกรเครื่องกล	
-	
ผู้เขียน	
นายปฐวี เชื้อชม ภย.33663 92 ม. 1 ต.ท่าโพธิ์ศรี อ.เดชอุดม จ.อุบลราชธานี	
ที่ตั้ง	
บ้านไม้จ้าว ตำบล ป่าตอง อำเภอ กะทู้ จังหวัด ภูเก็ต	
แบบแสดง	
สารบัญ-รายการวัสดุ	
FILE NO	DRAWING NO
	3
SUB TOTAL	GRAND TOTAL
DATE	--

รายการประกอบแบบ	รายการประกอบแบบ	ชื่อโครงการ
งานก่ออิฐและฉาบปูน วัสดุทั่วไปเป็นอิฐมอญ ซีเมนต์ ทราย น้ำ เหมือนงาน ค.ส.ล. อัตราส่วนผสมปูนก่อ เมื่อผสมปูนซีเมนต์แล้วต้องใช้เวลาภายใน 1 ชั่วโมง ปูนซีเมนต์ 1 ส่วน ทรายหยาบ 3.5 - 4 ส่วน น้ำปริมาณเพียงพอทำงานได้ การก่อ ส่วนที่ก่อชนกับเสาเอ็นคอนกรีตต้องเสียบเหล็กขนาด 6 มม. ไว้ที่เสาขณะหล่อเสาทุกระยะไม่เกิน60 ซม. และต้องทำการรดน้ำเสาคอนกรีตก่อนทำการก่อการก่ออิฐบล็อกสำหรับผนังทั่วไป จะต้องใส่เอ็น ค.ส.ล.โดยใช้เหล็กขนาด 6 มม.ระยะห่าง 20 ซม. การใส่เอ็น ค.ส.ล. ให้ใส่ตรงตำแหน่งต่อไปนี้ ผนังก่ออิฐพื้นใหญ่ต้องมีทั้งทางตั้งและทางนอน ต่อพื้นที่ไม่เกิน 6 ตารางเมตร ทับหลังผนังก่ออิฐบนและล่าง วงกบ ประตู หน้าต่าง ด้านข้างวงกบ ประตู หน้าต่าง และตรงมุมห้องที่มีผนังก่ออิฐมาชนกัน อัตราส่วนผสมปูนฉาบ เมื่อผสมปูนซีเมนต์แล้วต้องใช้เวลาภายในครึ่งชั่วโมง ปูนซีเมนต์ 1 ส่วน ปูนขาว 1 ส่วน ทรายละเอียด 3 ส่วน งานไม้ ไม้ต้องเป็นไม้เนื้อแข็งไม่มีรู โปรง แตกร้าว บิดงอและข้อบกพร่องอื่น ๆ เป็นไม้ที่ผ่านการอบแห้งหากมีการยึดตัวภายหลัง ผู้รับจ้างต้องแก้ไขและรับผิดชอบต่อความเสียหายทั้งหมดโครงไม้ทั้งหมดต้องทาน้ำยากันปลวก ลักษณะทางสถาปัตยกรรม พื้น วัสดุผิวพื้น ตำแหน่งตามกำหนดในแบบ การปูพื้นจะต้องปูพื้นให้ถูกต้องตามหลักวิชาการและกรรมวิธีของผู้ผลิต วัสดุ ปูพื้นทุกชนิดที่นำมาใช้จะต้องไม่มีตำหนิ แตก บิ่น งอ ร้าว และจะต้องเป็นของใหม่ การปูกระเบื้องจะต้องได้แนวตรงกันการจัดวางกระเบื้องต้องพยายามให้ลงตัวพอดี เมื่อปูพื้นแล้วต้องเรียบไม่เป็นแอ่งส่วนที่ระบุให้ลาดเอียงให้เป็นไปตามแบบ วัสดุปูพื้น ต้องได้มาตรฐาน มอก. ผนัง ผนังทั่วไปเป็นผนังก่ออิฐมอญครึ่งแผ่นและเต็มแผ่น ก่อสลับแนว อิฐมอญที่ใช้ต้องมีขนาดและคุณภาพได้มาตรฐาน ใช้ชนิดอัดแน่นด้วยเครื่องเผาสุกได้ความแข็งแรงไม่เปราะหักง่าย ก่อด้วยปูนทรายความหนาแนวปูนทรายไม่เกิน 1.5 ซม. ปูนซีเมนต์ที่ใช้ในการก่อและฉาบเป็นประเภทซีลิก้า ซีเมนต์ของตราเสือหรือ ตรานกอินทรีย์ผิวผนังฉาบปูนใช้อัตราส่วน 1 ต่อ 4 ระหว่างปูนซีเมนต์กับทรายละเอียดปูนฉาบผสมด้วยน้ำยาผสมปูนฉาบในอัตราส่วนตามข้อกำหนดของผู้ผลิตวัสดุผิวต ามแบบกำหนด หรือ ตามผู้ว่าจ้างกำหนด งานสีอาคาร ผิววัสดุที่เป็นปูน ทาด้วยสีกันเชื้อรา 1 ครั้ง และทาสีพลาสติกทับ 2 ครั้ง (ผนังภายนอกใช้สีพลาสติกภายนอก , ผนังภายในใช้สีพลาสติกภายใน) ใช้สีกัปตันหรือเทียบเท่าผิววัสดุที่เป็นหลัก ทาด้วยสีรองพื้นกันสนิม 1 ครั้ง และทาสีน้ำมันทับ 2 ชั้นผิววัสดุที่เป็นไม้ ทารองพื้นด้วยสีรองพื้นไม้กันเชื้อรา 1 ชั้น สีน้ำมัน 1 ชั้น หรือสีธรรมชาติการป้องกันปลวก ใช้น้ำยาเคมีอัดและราดพื้น โดยรอบคานคอดินสีใช้ของ กัปตัน หรือ เทียบเท่า	หมายเหตุ รายการประกอบแบบก่อสร้างมาตรฐานดังกล่าวข้างต้น หากมิได้ระบุไว้ ให้ถือตามที่ระบุไว้ในแบบพิมพ์เขียวรายการต่าง ๆ หากมีปัญหาให้ปรึกษาสถาปนิกออกแบบ หรือวิศวกรผู้ออกแบบเสียก่อน หมายเหตุสำคัญ : การก่อสร้างให้เป็นไปตามมาตรฐานของวิศวกรรมสถานและ มาตรฐานทางสถาปัตยกรรมให้ถือว่ารายละเอียดประกอบแบบปะหน้านี้เป็นส่วนหนึ่งของสัญญา โดยหารายละเอียดต่างๆ ไม่สมบูรณ์ ให้พิจารณารายการ(ข้อกำหนด)ประกอบแบบก่อสร้างซึ่งเป็นเล่มขนาด A3 ที่ประกอบแนบมา (กรณีที่มีการแนบในสัญญา) กรณีไม่มีให้ยึดถือ รายการประกอบแบบก่อสร้างนี้เป็นส่วนหนึ่งในสัญญา หากมีข้อสงสัยในแบบก่อสร้าง ผู้รับเหมาต้องสอบถาม เพื่อขอความชัดเจนจากสถาปนิกเจ้าของแบบและวิศวกรและแจ้งให้เจ้าของโครงการทราบก่อนการก่อสร้างจริง มีฉะนั้นจะถือเป็นความรับผิดชอบของผู้รับเหมา ซึ่งจะต้องแก้ไขให้ถูกต้อง สมบูรณ์ก่อนการส่งมอบงานซึ่งจะถือเป็นค่าใช้จ่ายเพิ่มเติมมิได้	โครงการก่อสร้าง อาคารพักอาศัย คสล. 1 ชั้น
		เจ้าของโครงการ
		คุณปรินทร เรืองรัตนวานิช
		สถาปนิก
		 นายนิกร สุขแสง ภสธ.10581 ถ.แจ้งวัฒนะซอย6 แขวงตลาดบางเขน. เขตหลักสี่. กรุงเทพฯ
		วิศวกรโครงสร้าง
		 นายปฐวี เชื้อชม ภย.33663 92 ม. 1 ต.ท่าโพธิ์ศรี อ.เดชอุดม จ.อุบลราชธานี
		วิศวกรไฟฟ้า
		-
		วิศวกรเครื่องกล
		-
		ผู้เขียน
		นายปฐวี เชื้อชม ภย.33663 92 ม. 1 ต.ท่าโพธิ์ศรี อ.เดชอุดม จ.อุบลราชธานี
		ที่ตั้ง
		บ้านไม้จ้าว ตำบล ป่าตอง อำเภอ กะตุ จังหวัด ภูเก็ต
		แบบแสดง
		รายการประกอบแบบสถาปัตย์
		FILE NO
		DRAWING NO
		4
		SUB TOTAL
		GRAND TOTAL
		DATE
		--

แบบแสดงวิธีการติดตั้งแนวผ้าใบป้องกันวัสดุก่อสร้างตกหล่นโดยรอบอาคาร

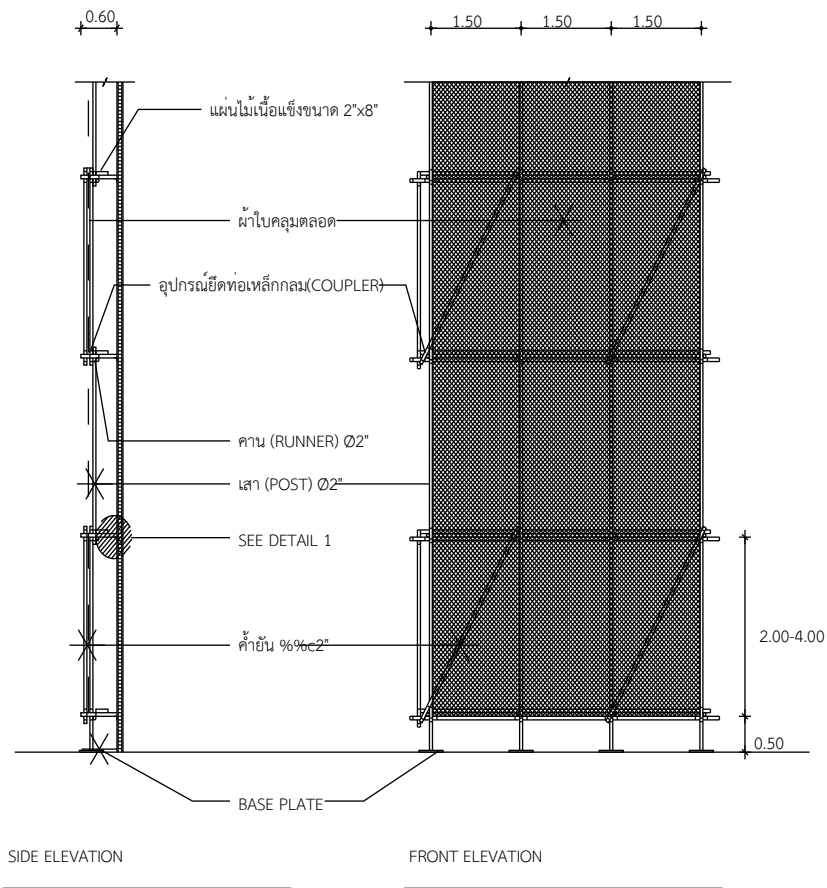

หลักเกณฑ์ วิธีการและเงื่อนไขในการก่อสร้าง ดัดแปลง รื้อถอน เคลื่อนย้าย ใช้หรือเปลี่ยนการใช้อาคาร ให้เป็นไปตามที่กำหนดในกฎกระทรวงนี้

กฎกระทรวง ฉบับที่ 4 (พ.ศ. 2526)

- 1.ในการก่อสร้างอาคาร ผู้ได้รับใบอนุญาตหรือผู้ดำเนินการต้องดำเนินการให้เป็นไปตามเงื่อนไขแห่งการอนุญาต
- 2.ในการก่อสร้างอาคารที่ติดต่อกับที่สาธารณะ ผู้ดำเนินการจะก่อสร้างได้เมื่อได้จัดให้มีสิ่งป้องกันวัสดุร่วงหล่นที่อาจเป็นอันตรายต่อสุขภาพ ชีวิต ร่างกาย หรือทรัพย์สินแล้ว
- 3.ผู้ดำเนินการต้องตรวจสอบและบำรุงรักษาเครื่องมือเครื่องใช้ในการก่อสร้างให้อยู่ในสภาพที่เหมาะสมและปลอดภัยกับการใช้งานอยู่เสมอ
- 4.ผู้ดำเนินการจะต้องไม่ระทำการใด ๆ อันอาจเป็นอันตรายต่อสุขภาพ ชีวิต ร่างกาย หรือทรัพย์สิน
- 5.ผู้ได้รับใบอนุญาตหรือผู้ดำเนินการต้องจัดให้มีรั้วชั่วคราวสูงไม่น้อยกว่า 2.00 เมตร ปิดกันตามแนวเขตที่ติดต่อกับที่สาธารณะหรือที่ดินต่างเจ้าของหรือผู้ครอบครอง และมีสิ่งป้องกันวัสดุร่วงหล่นที่อาจเป็นอันตรายต่อสุขภาพ ชีวิต ร่างกาย หรือทรัพย์สินด้วย
- 6.ในระหว่างการก่อสร้างอาคาร ผู้ดำเนินการต้องตรวจสอบความแข็งแรงและความปลอดภัยของนั่งร้านที่สร้างขึ้นเป็นประจำ โดยบันทึกผลการตรวจสอบและลงลายมือชื่อไว้ทุกเดือน เก็บไว้ ณ สถานที่ที่ก่อสร้าง เพื่อให้นายช่างหรือนายตรวจตรวจดูได้ การสร้างนั่งร้านต้องอยู่ภายใต้เงื่อนไข ดังต่อไปนี้

(ก) นั่งร้านที่ใช้สำหรับการก่อสร้างอาคารที่สูงเกินห้าชั้นหรือมีความสูงเกิน 21.00 เมตร ผู้ดำเนินการต้องยื่นแผนผัง บริเวณ แบบแปลนและรายการประกอบแบบแปลนของนั่งร้าน ซึ่งออกแบบคำนวณโดยผู้ได้รับใบอนุญาตให้เป็นผู้ประกอบวิชาชีพอวิศวกรควบคุมตามกฎหมายว่าด้วยวิชาชีพวิศวกรรมต่อเจ้าพนักงานท้องถิ่น เพื่อเป็นหลักฐานก่อน จึงจะสร้างนั่งร้านดังกล่าวได้

(ข) นั่งร้านที่สร้างด้วยโลหะรวมทั้งฐานรองรับนั่งร้านต้องรับน้ำหนักได้ไม่น้อยกว่าสองเท่าของน้ำหนักบรรทุกทุกสูงสุดที่บรรทุกบนนั่งร้านนั้น และไม่น้อยกว่าสี่เท่าสำหรับนั่งร้านที่สร้างด้วยไม้
7. ก่อนเริ่มลงมือก่อสร้างอาคาร ผู้ดำเนินการต้องสำรวจรายละเอียดตำแหน่ง ความลึก และขนาดของโครงสร้างได้ดิน ฐานรากอาคารข้างเคียง หรือสิ่งก่อสร้างอื่น ๆ เช่น ท่อประปา สายเคเบิล เป็นต้น
- 8.เมื่อมีการขุดดินในบริเวณที่ติดต่อกับที่สาธารณะหรือในที่สาธารณะ ผู้ดำเนินการต้องจัดให้มีสิ่งกันตกหรือราวกันรอบบริเวณนั้นและติดตั้งป้ายเตือนอันตรายเพื่อความปลอดภัยของประชาชน
- 9.เมื่อมีการขุดดินในบริเวณที่ใกล้หรือติดต่อกับที่สาธารณะห้ามผู้ดำเนินการกองดินบนที่สาธารณะและขุดเจาะดินล้ำเขตที่สาธารณะนั้น เว้นแต่จะได้รับอนุญาตเป็นหนังสือจากเจ้าพนักงานท้องถิ่น
- 10.เมื่อมีการขุดดินในบริเวณที่ใกล้หรือชิดอาคาร ถนน หรือกำแพง ลึกจนอาจเป็นอันตรายแก่อาคาร ถนน หรือกำแพงนั้น ผู้ดำเนินการต้องจัดให้มีค้ำยันเข็มพืด หรือฐานรากเสริมตาความจำเป็นเพื่อความปลอดภัย และต้องตรวจสอบแก้ไขค้ำยัน เข็มพืด และฐานรากให้มีสภาพมั่นคง
- 11.การกองวัสดุ เช่น หิน หวาย หรือดิน เป็นต้น ในบริเวณที่ใกล้หรือชิดขอบบ่อที่ขุด ผู้ดำเนินการต้องกองห่างจากขอบบ่อพอสมควร เพื่อป้องกันมิให้ผนังบ่อเสียหายและมีให้วัสดุร่วงหล่นที่จะเป็นอันตรายแก่ผู้ขุดได้
12. ผู้ดำเนินการต้องจัดให้มีหมวกแข็ง ภายในหมวกต้องมีธงในหมวกที่ทำด้วยหนัง พลาสติก ผ้า หรือวัสดุอื่น เพื่อป้องกันอันตรายต่อศีรษะให้แก่ผู้ซึ่งได้รับอนุญาตให้เข้าไปอยู่ในบริเวณที่ก่อสร้างอาคาร

13.ห้ามผู้ดำเนินการนำเครื่องมือที่เป็นสื่อไฟฟ้าไปใช้ปฏิบัติงานใกล้สายไฟฟ้าแรงสูงหรืออุปกรณ์ไฟฟ้าแรงสูง เว้นแต่จะได้รับกระทำการอย่างหนึ่งอย่างใด ดังต่อไปนี้

- (ก) มีแผนฉนวนกันระหว่างส่วนที่มีกระแสไฟฟ้าแรงสูงกับเครื่องมือนั้น
- (ข) เครื่องมือนั้นได้ต่อสายดินไว้เรียบร้อยแล้ว
- (ค) สายไฟฟ้าแรงสูงหรืออุปกรณ์ไฟฟ้าแรงสูงนั้นได้หุ้มฉนวนอย่างดีแล้ว
- (ง) ได้ตัดกระแสไฟฟ้าออกจากสายไฟฟ้าแรงสูงหรืออุปกรณ์ไฟฟ้าแรงสูงนั้นแล้ว




14.ผู้ดำเนินการต้องใช้โซ่ เชือก ลวดสะลิง รอกที่ใช้งานปั้นจั่นหรือลิฟต์ส่งของที่มีสภาพแข็งแรงและมีขนาดพอที่จะใช้ในการยก การวาง และยกน้ำหนักสิ่งของให้ลอยตัวอยู่ที่จุดหนึ่งจุดใดได้โดยปลอดภัย

15.เมื่อหยุดการใช้ปั้นจั่นหรือลิฟต์ส่งของประจำวัน ผู้ดำเนินการต้องจัดให้มีการป้องกันมิให้ปั้นจั่น หรือลิฟต์ส่งของนั้นเลื่อน ล้มหรือหมุน อันอาจเป็นอันตรายต่อสุขภาพ ชีวิต ร่างกาย หรือทรัพย์สิน

16. ผู้ดำเนินการต้องจัดให้มีผู้ควบคุมที่มีความชำนาญควบคุมการใช้เครื่องมือกล เครื่องจักร หรือเครื่องจักรกล และต้องตรวจสอบและบำรุงรักษาให้อยู่ในสภาพที่เหมาะสมและปลอดภัยกับการใช้งานอยู่เสมอ

17.ในกรณีที่มีการติดตั้งลูกกรง เหล็กตัด หรือสิ่งอื่นที่มีลักษณะทำนองเดียวกันที่ประตู หน้าต่างหรือที่ด้านนอกหรือด้านในของอาคารตั้งแต่ชั้นที่สองขึ้นไป อันเป็นการกีดขวางการหนีออกจากอาคารหรือการช่วยเหลือผู้ที่อยู่ในอาคารเมื่อเกิดอัคคีภัยโดยไม่มีช่องทางอื่นที่จะออกสู่ภายนอกได้ ให้ผู้ได้รับใบอนุญาตหรือผู้ดำเนินการจัดให้มีช่องทางที่เปิดออกสู่ภายนอกได้ทันที ขนาดกว้างไม่น้อยกว่า 0.60 เมตร ยาวไม่น้อยกว่า 0.80 เมตร อย่างน้อยหนึ่งช่องทางในแต่ละชั้นของอาคารหรือของคูหา"

ชื่อโครงการ	
โครงการก่อสร้างอาคารพักอาศัย คสล. 1 ชั้น	
เจ้าของโครงการ	
คุณปรินทร์ เรืองรัตนวานิช	
สถาปนิก	
นายนิกร สุขแสง ภสธ.10581 ถ.แจ้งวัฒนะซอย6 แขวงตลาดบางเขน. เขตหลักสี่. กรุงเทพฯ	
วิศวกรโครงสร้าง	
นายปฐวี เชื้อชม ภย.33663 92 ม. 1 ต.ท่าโพธิ์ศรี อ.เดชอุดม จ.อุบลราชธานี	
วิศวกรไฟฟ้า	
-	
วิศวกรเครื่องกล	
-	
ผู้เขียน	
นายปฐวี เชื้อชม ภย.33663 92 ม. 1 ต.ท่าโพธิ์ศรี อ.เดชอุดม จ.อุบลราชธานี	
ที่ตั้ง	
บ้านไม้จ้าว ตำบล ป่าตอง อำเภอ กะตุ จังหวัด ภูเก็ต	
แบบแสดง	
การติดตั้งแนวผ้าใบป้องกันวัสดุ	
FILE NO	DRAWING NO
	5
SUB TOTAL	GRAND TOTAL
DATE	--

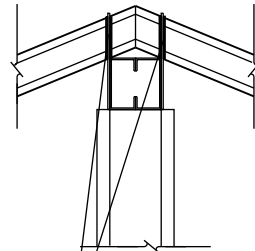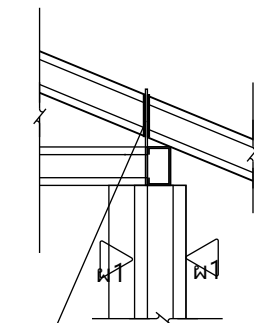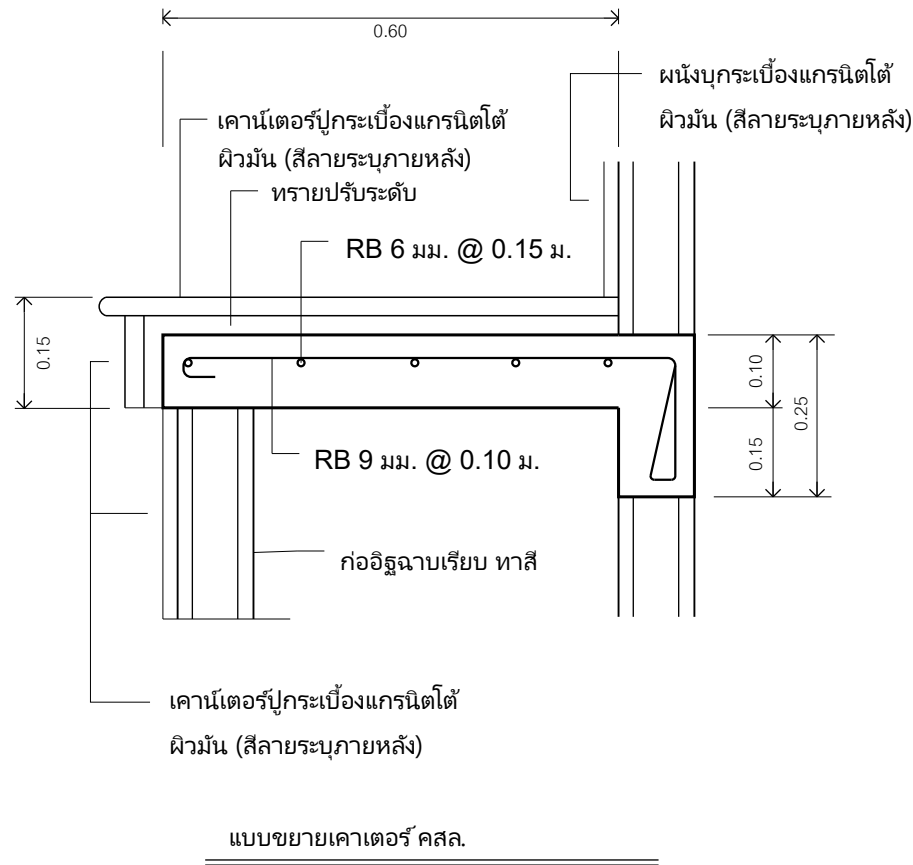

เหล็กกล่อง 1"×1"×1.5 มม. ยาว 0.30 ม.
เชื่อมยึดติดจันทัน,อะเส ทุกๆระยะตามมาตรฐาน

เหล็กกล่อง 1"×1"×1.5 มม. ยาว 0.30 ม.
เชื่อมยึดติดจันทัน,อะเส ทุกๆระยะตามมาตรฐาน

แบบขยายทั่วไป


No scale

วัดดุมงหลังคา (ตามแบบ)

เหล็กแบนปิดหัว ขนาด 50x50 ทน 2 มม.


เชิงชาย+ปิดลอนไม้เขอร์รา 1"x 8" ทับด้วย1"x 6"

เหล็กกล่อง 1"×1"×1.5 มม. ยาว 0.30 ม.
เชื่อมยึดติดจันทัน,อะเส ทุกๆระยะตามมาตรฐาน


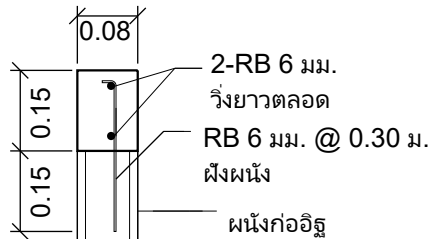


แบบขยายเอ็นทับหลัง คสล.


No scale

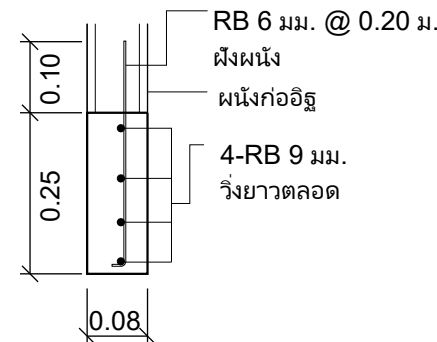

ขยายเอ็นทับหลัง กรณีเกิน 2 ม.

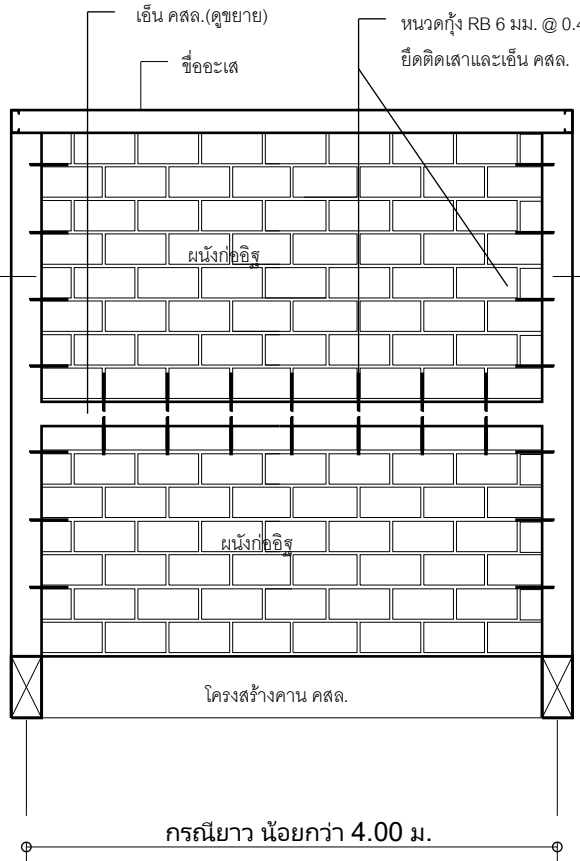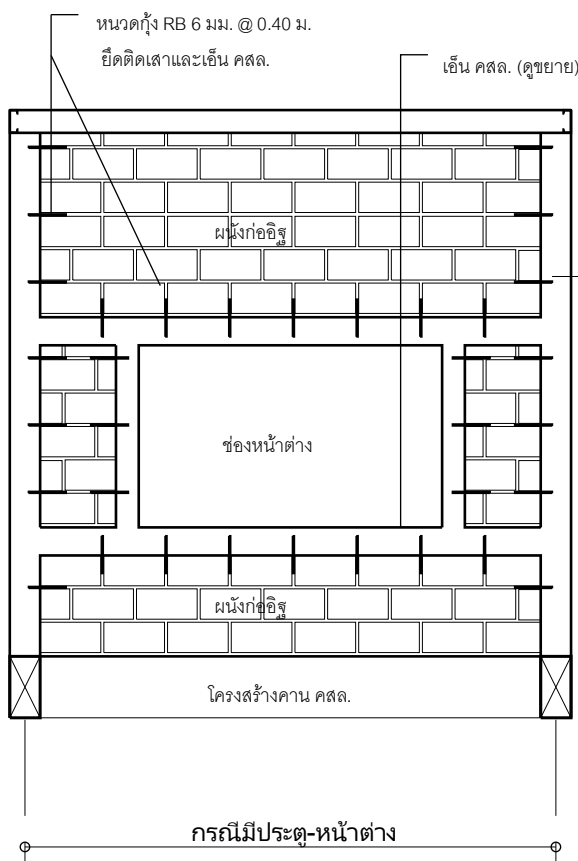

ขยายเหล็กเสริมหนวดกึ่งยึดผนัง

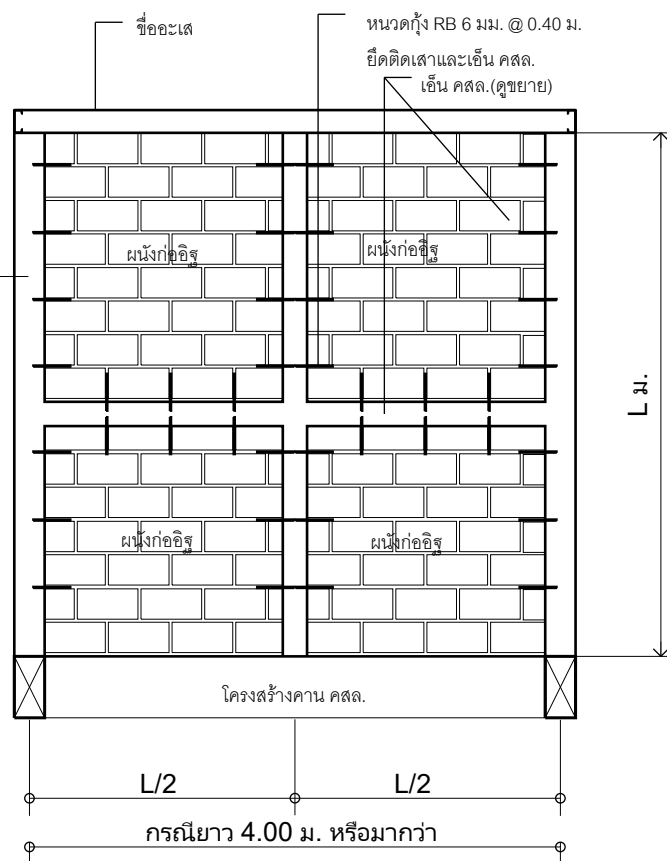

ชื่อโครงการ

โครงการก่อสร้าง
อาคารพักอาศัย
คสล. 1 ชั้น

เจ้าของโครงการ

คุณปรินทร์ เรืองรัตนวานิช

สถาปนิก

นายนิกร สุขแสง
ภสธ.10581
ถ.แจ้งวัฒนะซอย6
แขวงตลาดบางเขน.
เขตหลักสี่. กรุงเทพฯ

วิศวกรโครงสร้าง

นายปฐวี เชื้อชม
ภย.33663

92 ม. 1 ต.ท่าโพธิ์ศรี

อ.เดชอุดม จ.อุบลราชธานี

วิศวกรไฟฟ้า

วิศวกรเครื่องกล

ผู้เขียน

นายปฐวี เชื้อชม
ภย.33663
92 ม. 1 ต.ท่าโพธิ์ศรี
อ.เดชอุดม จ.อุบลราชธานี

ที่ตั้ง

บ้านไม้จ้าว
ตำบล ป่าตอง
อำเภอ กะตุ
จังหวัด ภูเก็ต

แบบแสดง

เสาเอ็น-ทับหลัง

FILE NO

SUB TOTAL

DATE

DRAWING NO


6

GRAND TOTAL

--

	ชื่อโครงการ	
	โครงการก่อสร้าง อาคารพักอาศัย คสล. 1 ชั้น	
	เจ้าของโครงการ	
	คุณปรินทร์ เรืองรัตนวานิช	
	สถาปนิก	
	 นายนิกร สุขแสง ภสธ.10581 ถ.แจ้งวัฒนะซอย6 แขวงตลาดบางเขน. เขตหลักสี่. กรุงเทพฯ	
	วิศวกรโครงสร้าง	
	 นายปฐวี เชื้อชม ภย.33663 92 ม. 1 ต.ท่าโพธิ์ศรี อ.เดชอุดม จ.อุบลราชธานี	
	วิศวกรไฟฟ้า	
	-	
วิศวกรเครื่องกล		
-		
ผู้เขียน		
นายปฐวี เชื้อชม ภย.33663 92 ม. 1 ต.ท่าโพธิ์ศรี อ.เดชอุดม จ.อุบลราชธานี		
ที่ตั้ง		
บ้านไม้จาว ตำบล ป่าตอง อำเภอ กะทู้ จังหวัดภูเก็ต		
แบบแสดง		
แผนที่		
FILE NO	DRAWING NO	
	7	
SUB TOTAL	GRAND TOTAL	
DATE	--	

	ชื่อโครงการ	
	โครงการก่อสร้าง อาคารพักอาศัย คสล. 1 ชั้น	
	เจ้าของโครงการ	
	คุณปรินทร์ เรืองรัตนวานิช	
	สถาปนิก	
	 นายนิกร สุขแสง ภสธ.10581 ถ.แจ้งวัฒนะซอย6 แขวงตลาดบางเขน. เขตหลักสี่. กรุงเทพ	
	วิศวกรโครงสร้าง	
	 นายปฐวี เชื้อชม ภย.33663 92 ม. 1 ต.ท่าโพธิ์ศรี อ.เดชอุดม จ.อุบลราชธานี	
	วิศวกรไฟฟ้า	
	-	
วิศวกรเครื่องกล		
-		
ผู้เขียน		
นายปฐวี เชื้อชม ภย.33663 92 ม. 1 ต.ท่าโพธิ์ศรี อ.เดชอุดม จ.อุบลราชธานี		
ที่ตั้ง		
บ้านไม้จาว ตำบล ป่าตอง อำเภอ กะตุ จังหวัด ภูเก็ต		
แบบแสดง		
ผังบริเวณ		
FILE NO	DRAWING NO	
	8	
SUB TOTAL	GRAND TOTAL	
DATE	--	

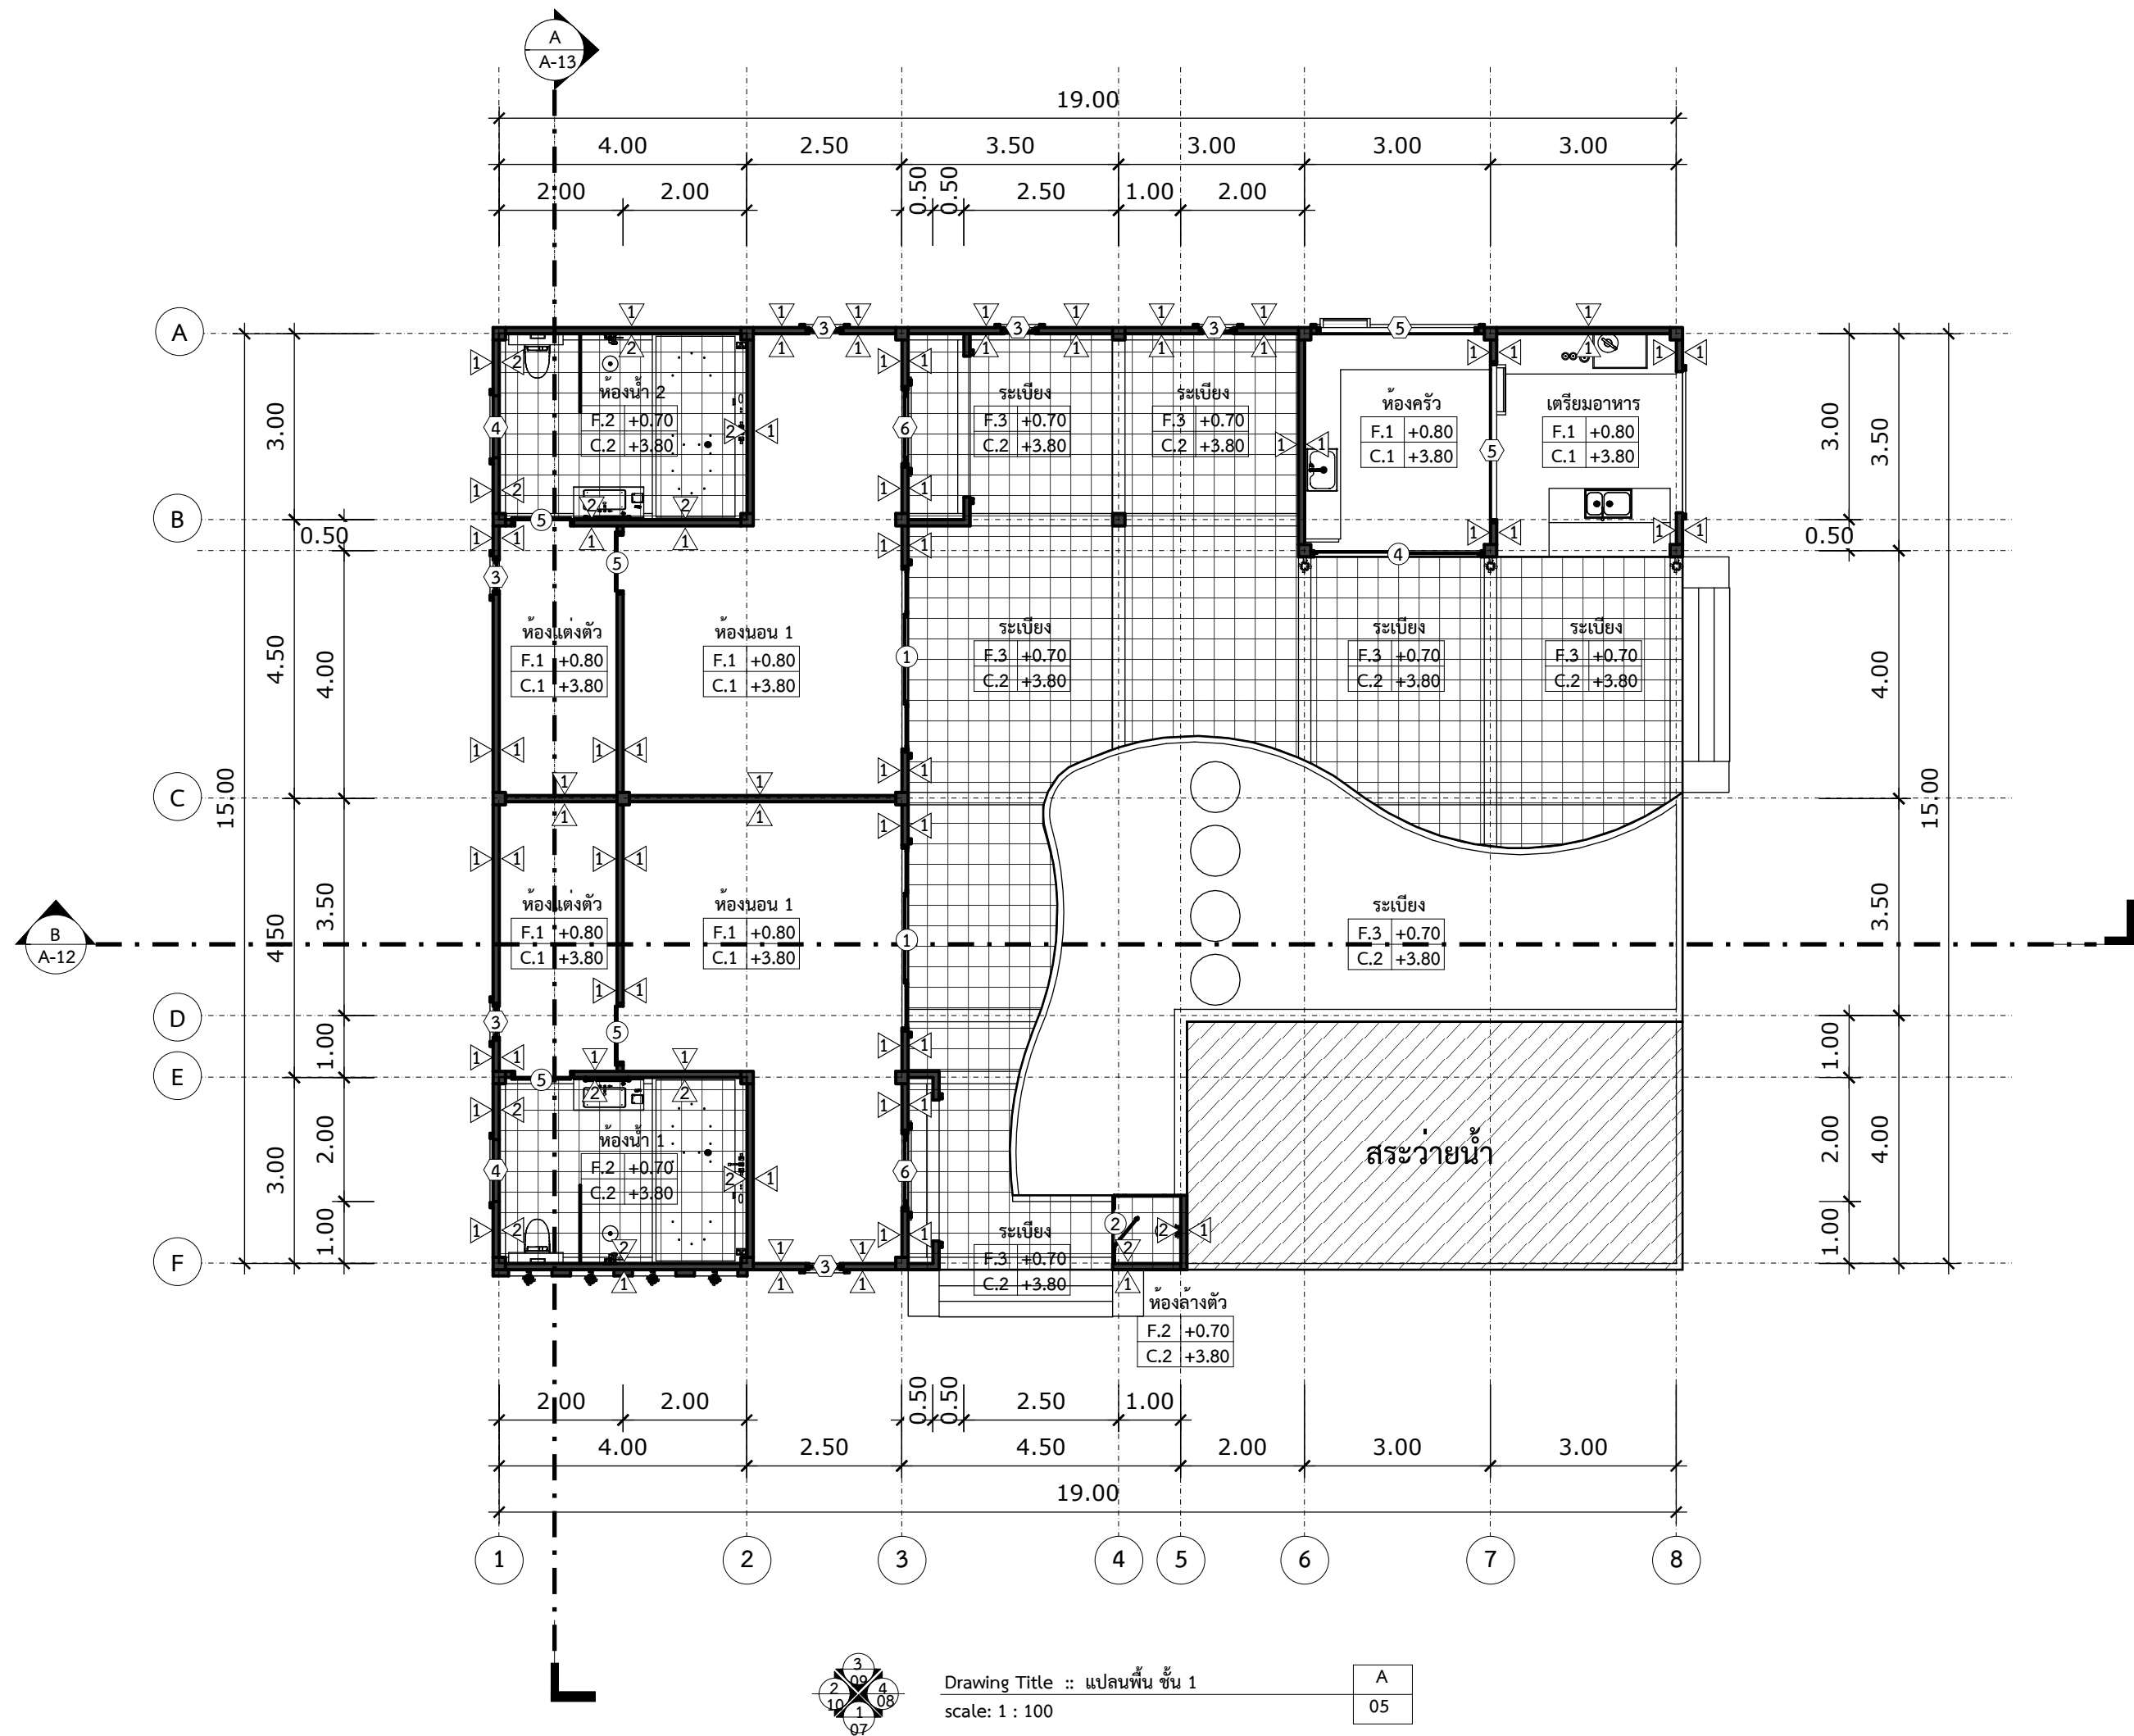

ชื่อโครงการ
โครงการก่อสร้าง
อาคารพักอาศัย
คสล. 1 ชั้น

เจ้าของโครงการ

คุณปรีนทร เรืองรัตนวณิช

สถาปนิก

นายนิกร สุขแสง
ภสศ.10581
ถ.แจ้งวัฒนะซอย6
แขวงตลาดบางเขน.
เขตหลักสี่. กรุงเทพฯ

วิศวกรโครงสร้าง

นายปฐวี เชื้อชม
ภย.33663
92 ม. 1 ต.ท่าโพธิ์ศรี
อ.เดชอุดม จ.อุบลราชธานี

วิศวกรไฟฟ้า
-

วิศวกรเครื่องกล
-

ผู้เขียน


นายปฐวี เชื้อชม
ภย.33663
92 ม. 1 ต.ท่าโพธิ์ศรี
อ.เดชอุดม จ.อุบลราชธานี

ที่ตั้ง
บ้านไม้จ้าว
ตำบล ป่าตอง
อำเภอ กะทู้
จังหวัดภูเก็ต


แบบแสดง

แปลนพื้น ชั้น 1 + 0.80

FILE NO	DRAWING NO
	9
SUB TOTAL	GRAND TOTAL
DATE	--

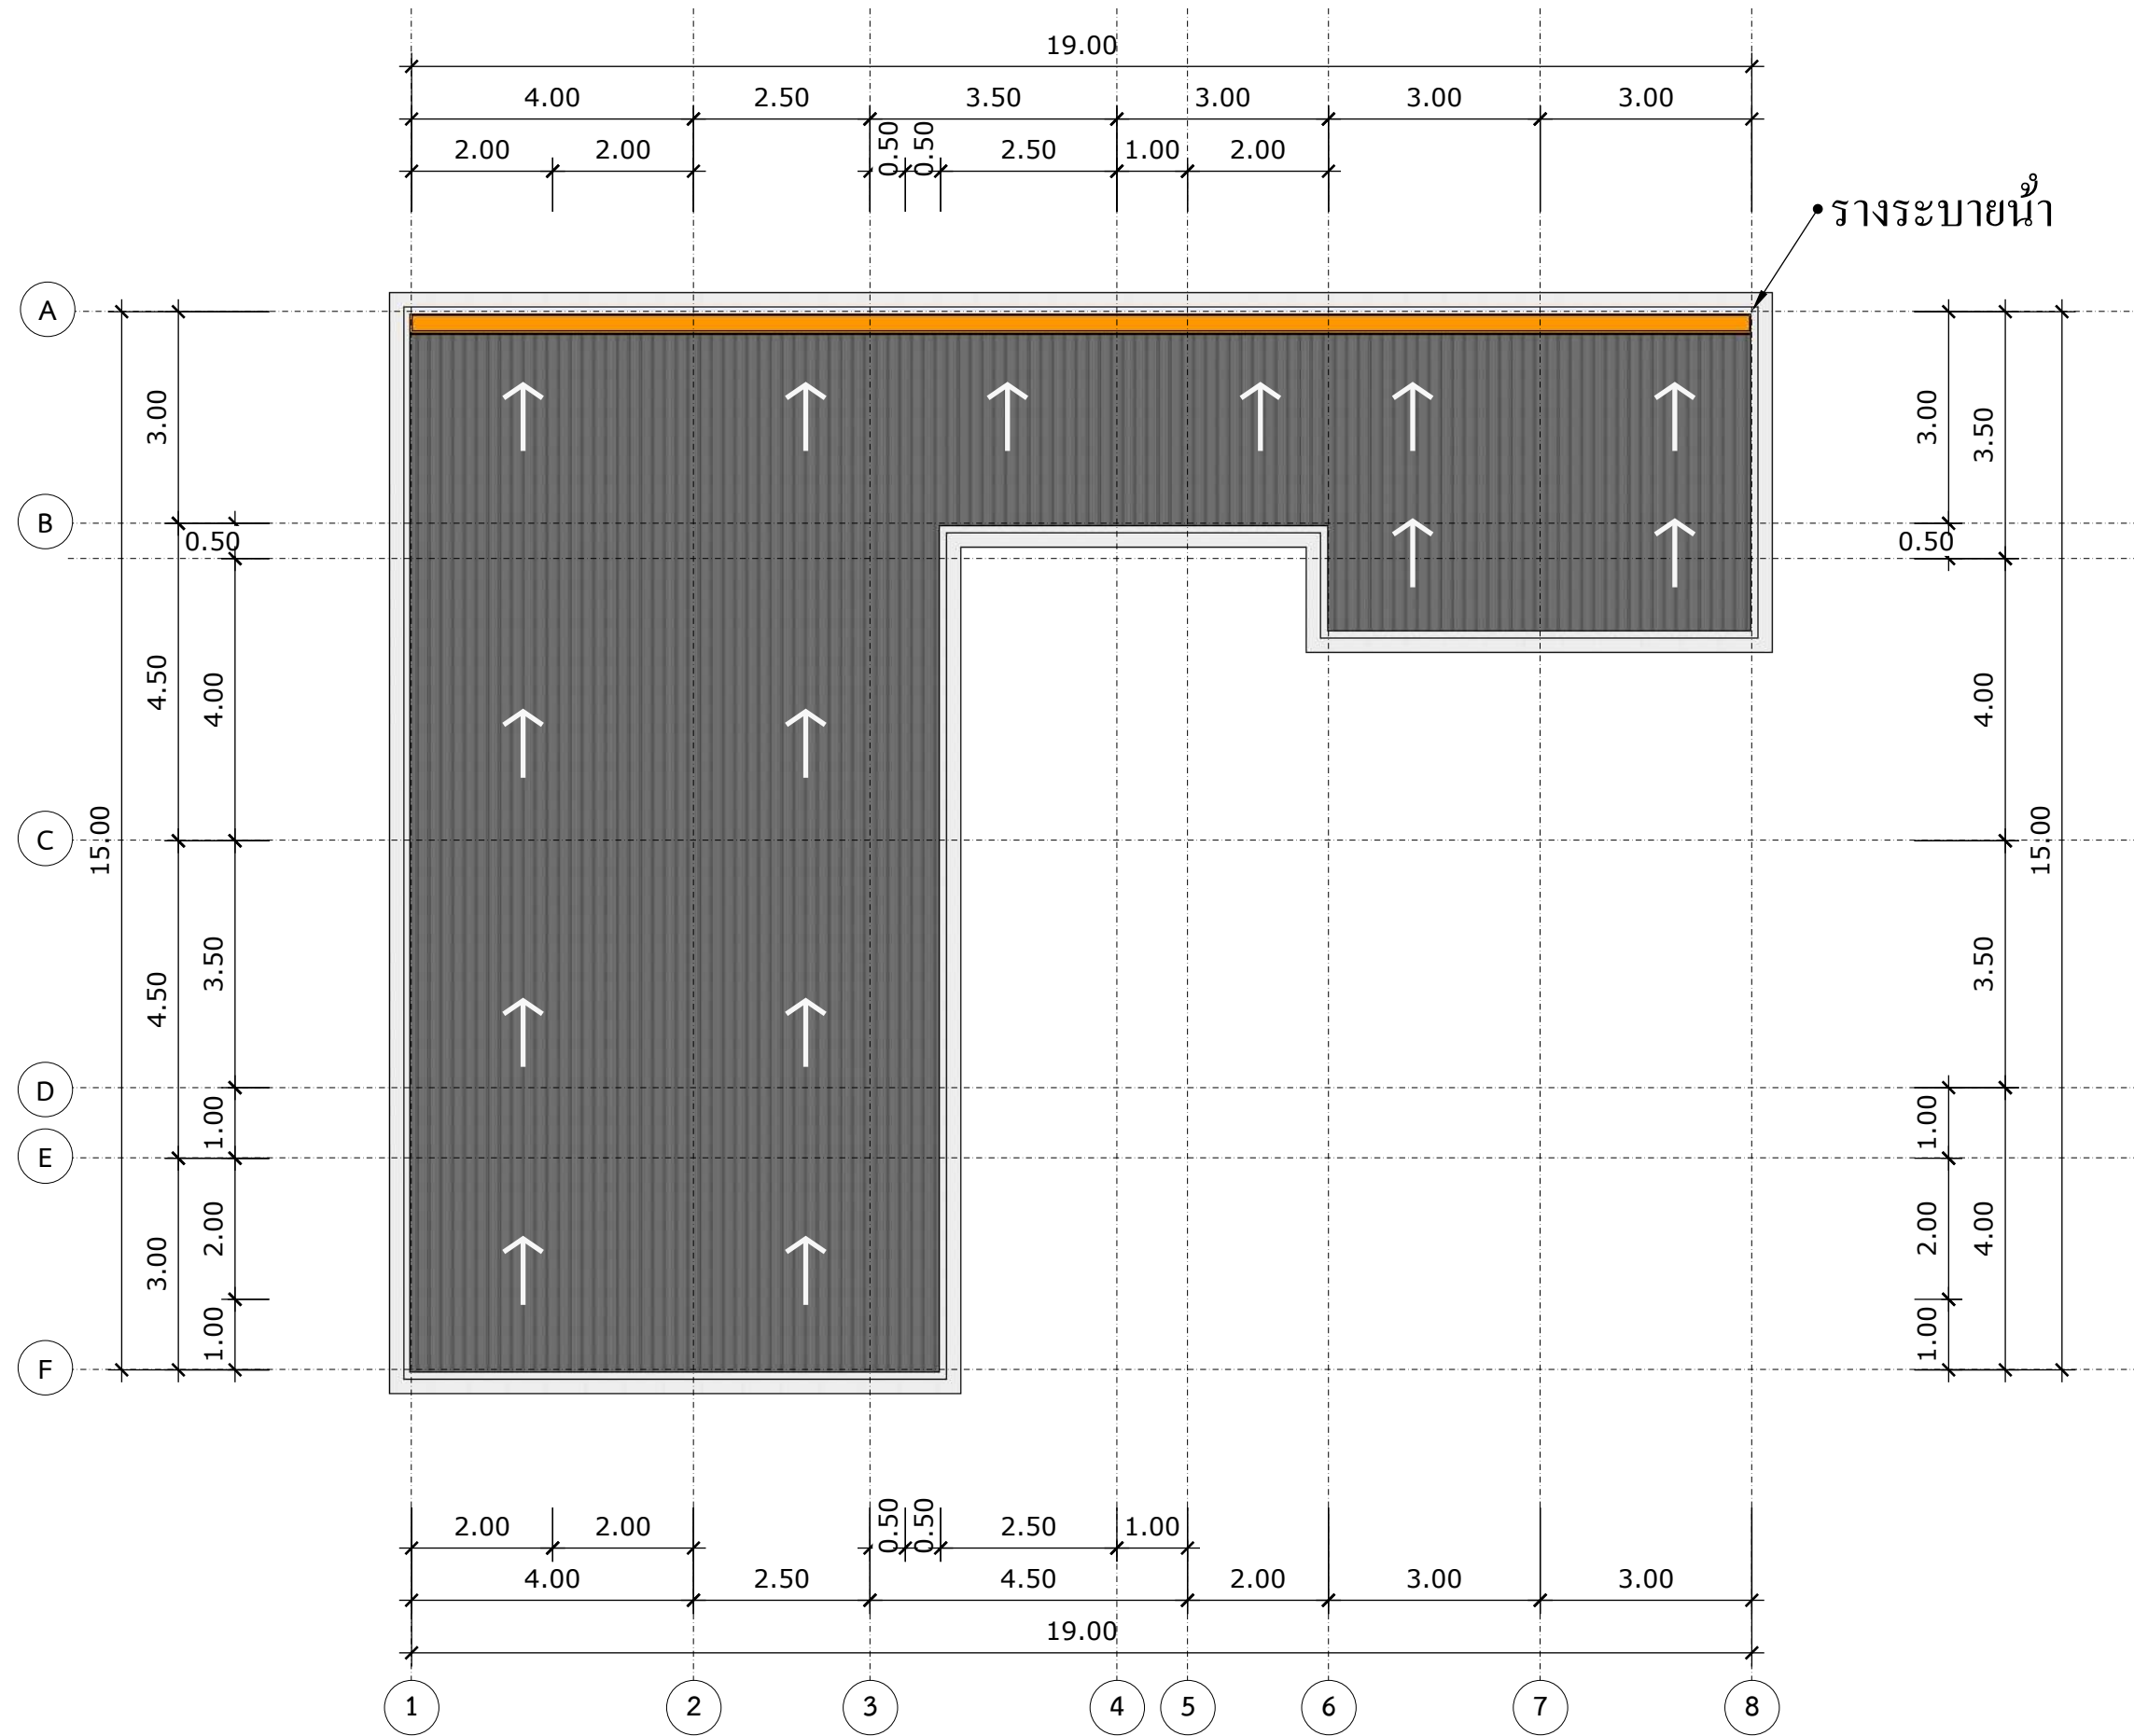


ชื่อโครงการ	
โครงการก่อสร้างอาคารพักอาศัย	
คสล. 1 ชั้น	
เจ้าของโครงการ	
คุณปรินทร์ เรืองรัตนวานิช	
สถาปนิก	
นายนิกร สุขแสง ภสศ.10581 ถ.แจ้งวัฒนะซอย6 แขวงตลาดบางเขน. เขตหลักสี่. กรุงเทพฯ	
วิศวกรโครงสร้าง	
นายปฐวี เชื้อชม ภย.33663 92 ม. 1 ต.ท่าโพธิ์ศรี อ.เดชอุดม จ.อุบลราชธานี	
วิศวกรไฟฟ้า	
-	
วิศวกรเครื่องกล	
-	
ผู้เขียน	
นายปฐวี เชื้อชม ภย.33663 92 ม. 1 ต.ท่าโพธิ์ศรี อ.เดชอุดม จ.อุบลราชธานี	
ที่ตั้ง	
บ้านไม้จ้าว ตำบล ป่าตอง อำเภอ กะทู้ จังหวัด ภูเก็ต	
แบบแสดง	
แปลนหลังคา	
FILE NO	DRAWING NO
	10
SUB TOTAL	GRAND TOTAL
DATE	--

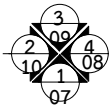



Drawing Title :: แปลนหลังคา
scale: 1 : 100

A
05

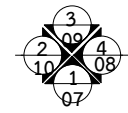


Drawing Title รูปด้าน 1
scale: 1 : 100

A
05

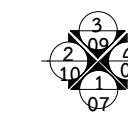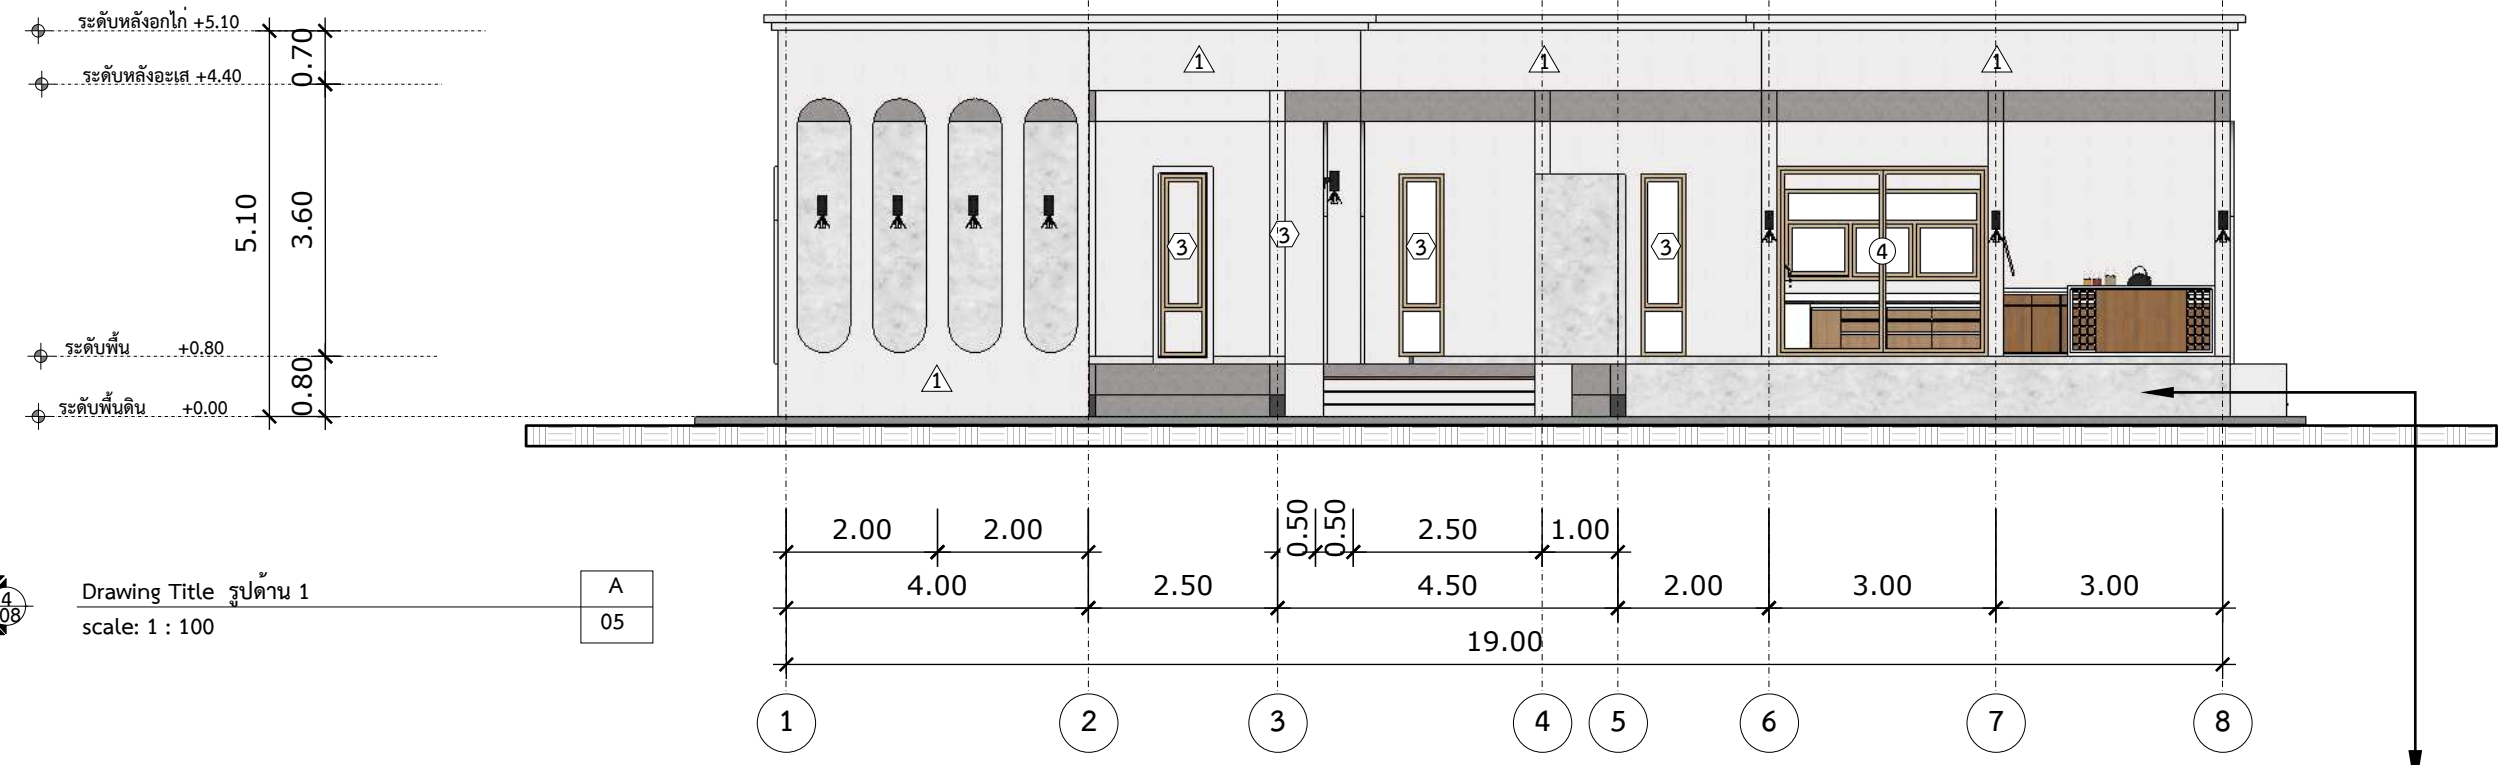


Drawing Title รูปด้าน 2
scale: 1 : 100

A
05


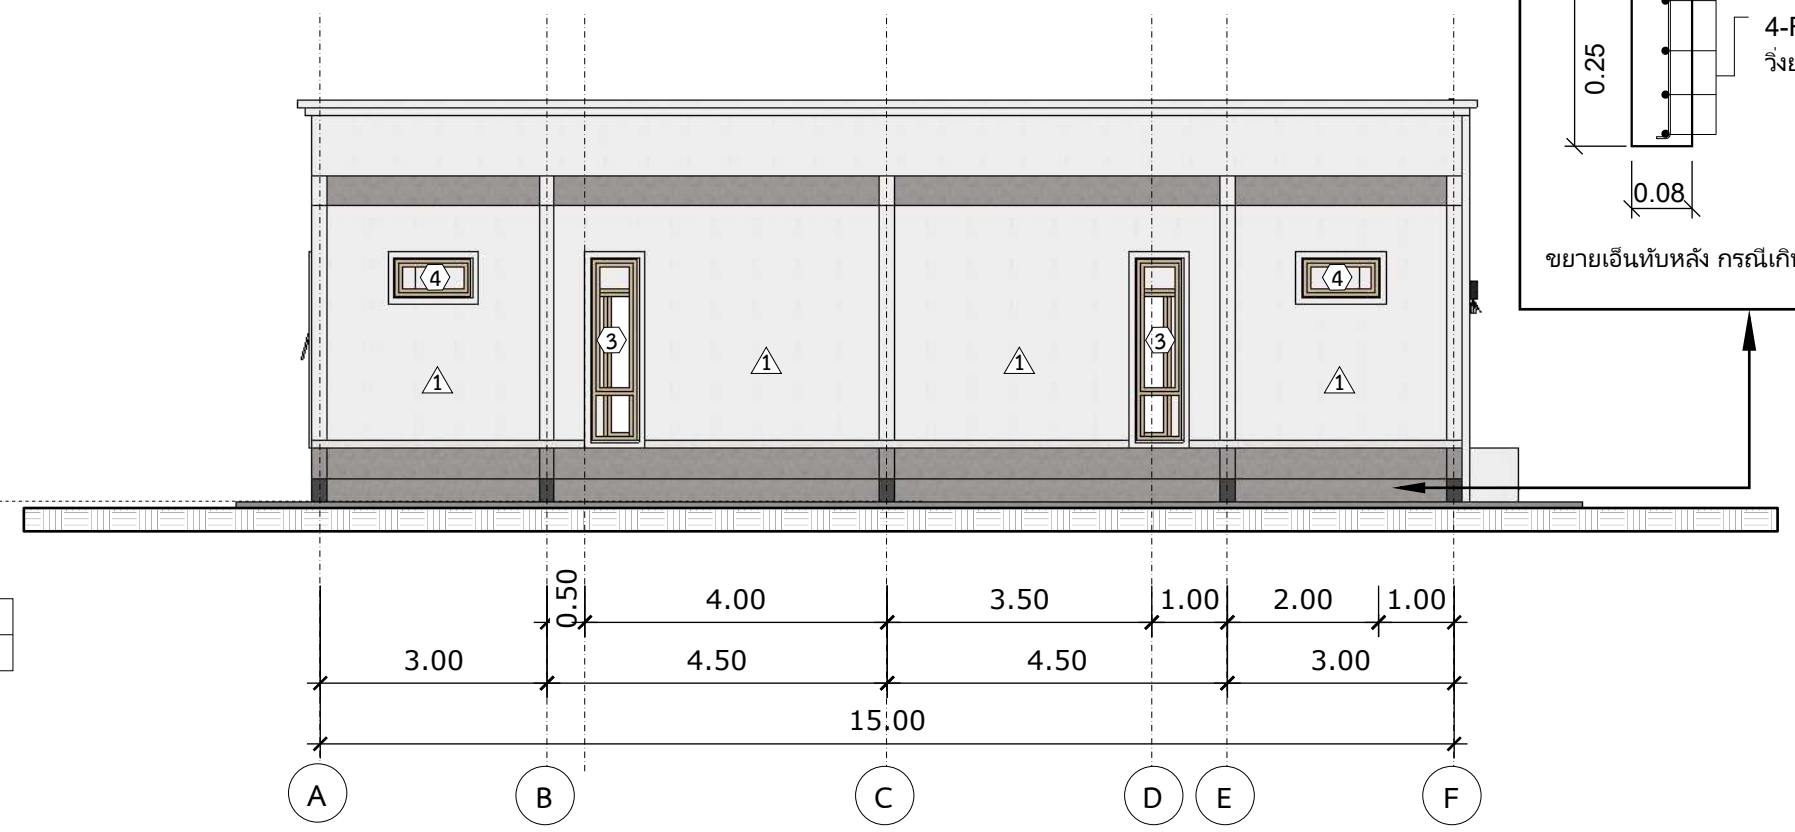


ชื่อโครงการ	
โครงการก่อสร้างอาคารพักอาศัย	
คสล. 1 ชั้น	
เจ้าของโครงการ	
คุณปรินทร์ เรืองรัตนวานิช	
สถาปนิก	
..... นายนิกร สุขแสง ภสธ.10581 ถ.แจ้งวัฒนะซอย6 แขวงตลาดบางเขน. เขตหลักสี่, กรุงเทพฯ	
วิศวกรโครงสร้าง	
..... นายปฐวี เชื้อชม ภย.33663 92 ม. 1 ต.ท่าโพธิ์ศรี อ.เดชอุดม จ.อุบลราชธานี	
วิศวกรไฟฟ้า	-
วิศวกรเครื่องกล	-
ผู้เขียน	นายปฐวี เชื้อชม ภย.33663 92 ม. 1 ต.ท่าโพธิ์ศรี อ.เดชอุดม จ.อุบลราชธานี
ที่ตั้ง	บ้านไม้จ้าว ตำบล ป่าตอง อำเภอ กะตุ จังหวัด ภูเก็ต
แบบแสดง	
รูปด้าน 1+2	
FILE NO	DRAWING NO
	11
SUB TOTAL	GRAND TOTAL
DATE	--

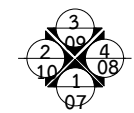



Drawing Title รูปด้าน 3
scale: 1 : 100

A
05

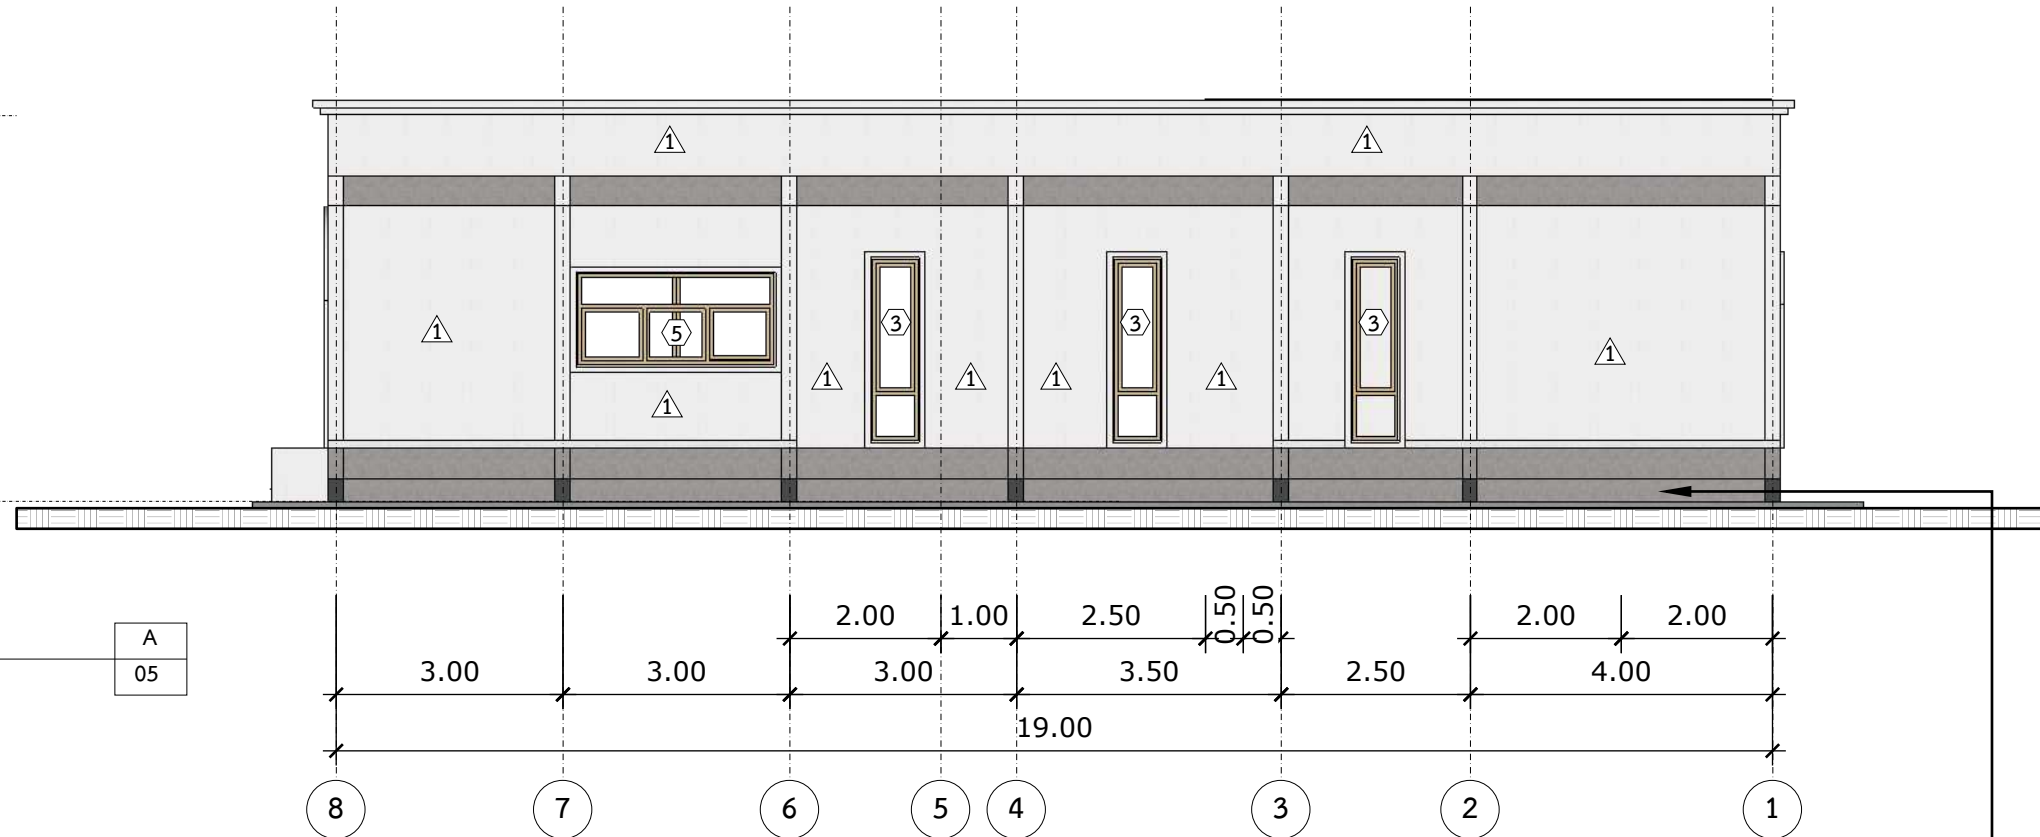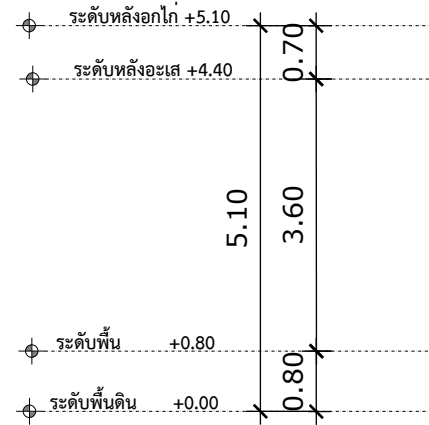


Drawing Title รูปด้าน 4
scale: 1 : 100

A
05

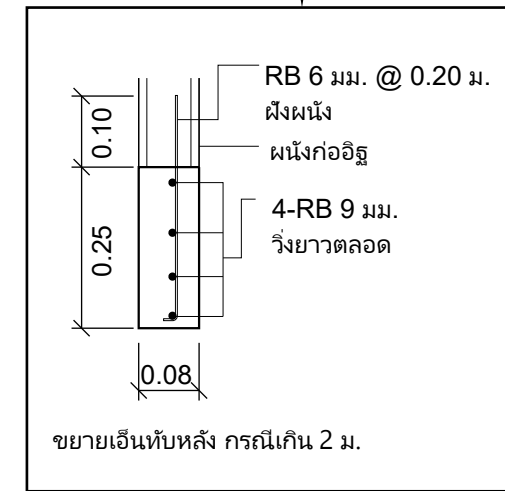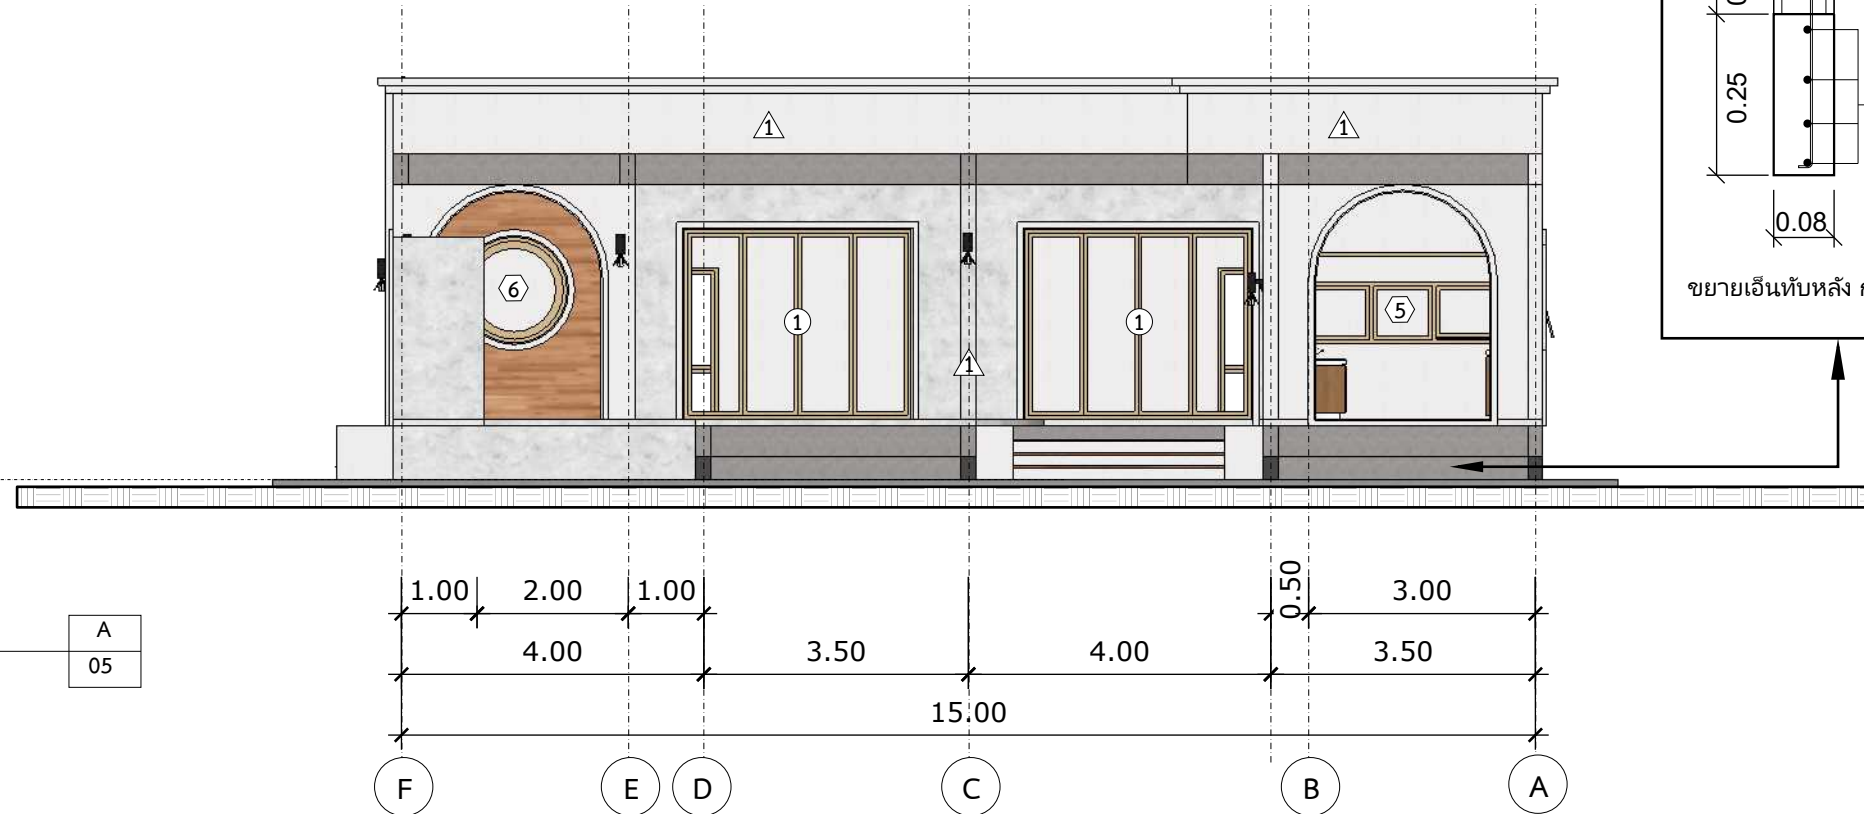


ชื่อโครงการ โครงการก่อสร้าง อาคารพักอาศัย คสล. 1 ชั้น	
เจ้าของโครงการ คุณปรีนทร เรืองรัตนวานิช	
สถาปนิก นายนิกร สุขแสง ภสธ.10581 ถ.แจ้งวัฒนะซอย6 แขวงตลาดบางเขน. เขตหลักสี่. กรุงเทพฯ	
วิศวกรโครงสร้าง นายปฐวี เชื้อชม ภย.33663 92 ม. 1 ต.ท่าโพธิ์ศรี อ.เดชอุดม จ.อุบลราชธานี	
วิศวกรไฟฟ้า	-
วิศวกรเครื่องกล	-
ผู้เขียน นายปฐวี เชื้อชม ภย.33663 92 ม. 1 ต.ท่าโพธิ์ศรี อ.เดชอุดม จ.อุบลราชธานี	
ที่ตั้ง	บ้านไม้จ้าว ตำบล ป่าตอง อำเภอ กะทู้ จังหวัดภูเก็ต
แบบแสดง รูปด้าน 3+4	
FILE NO	DRAWING NO
	12
SUB TOTAL	GRAND TOTAL
DATE	--

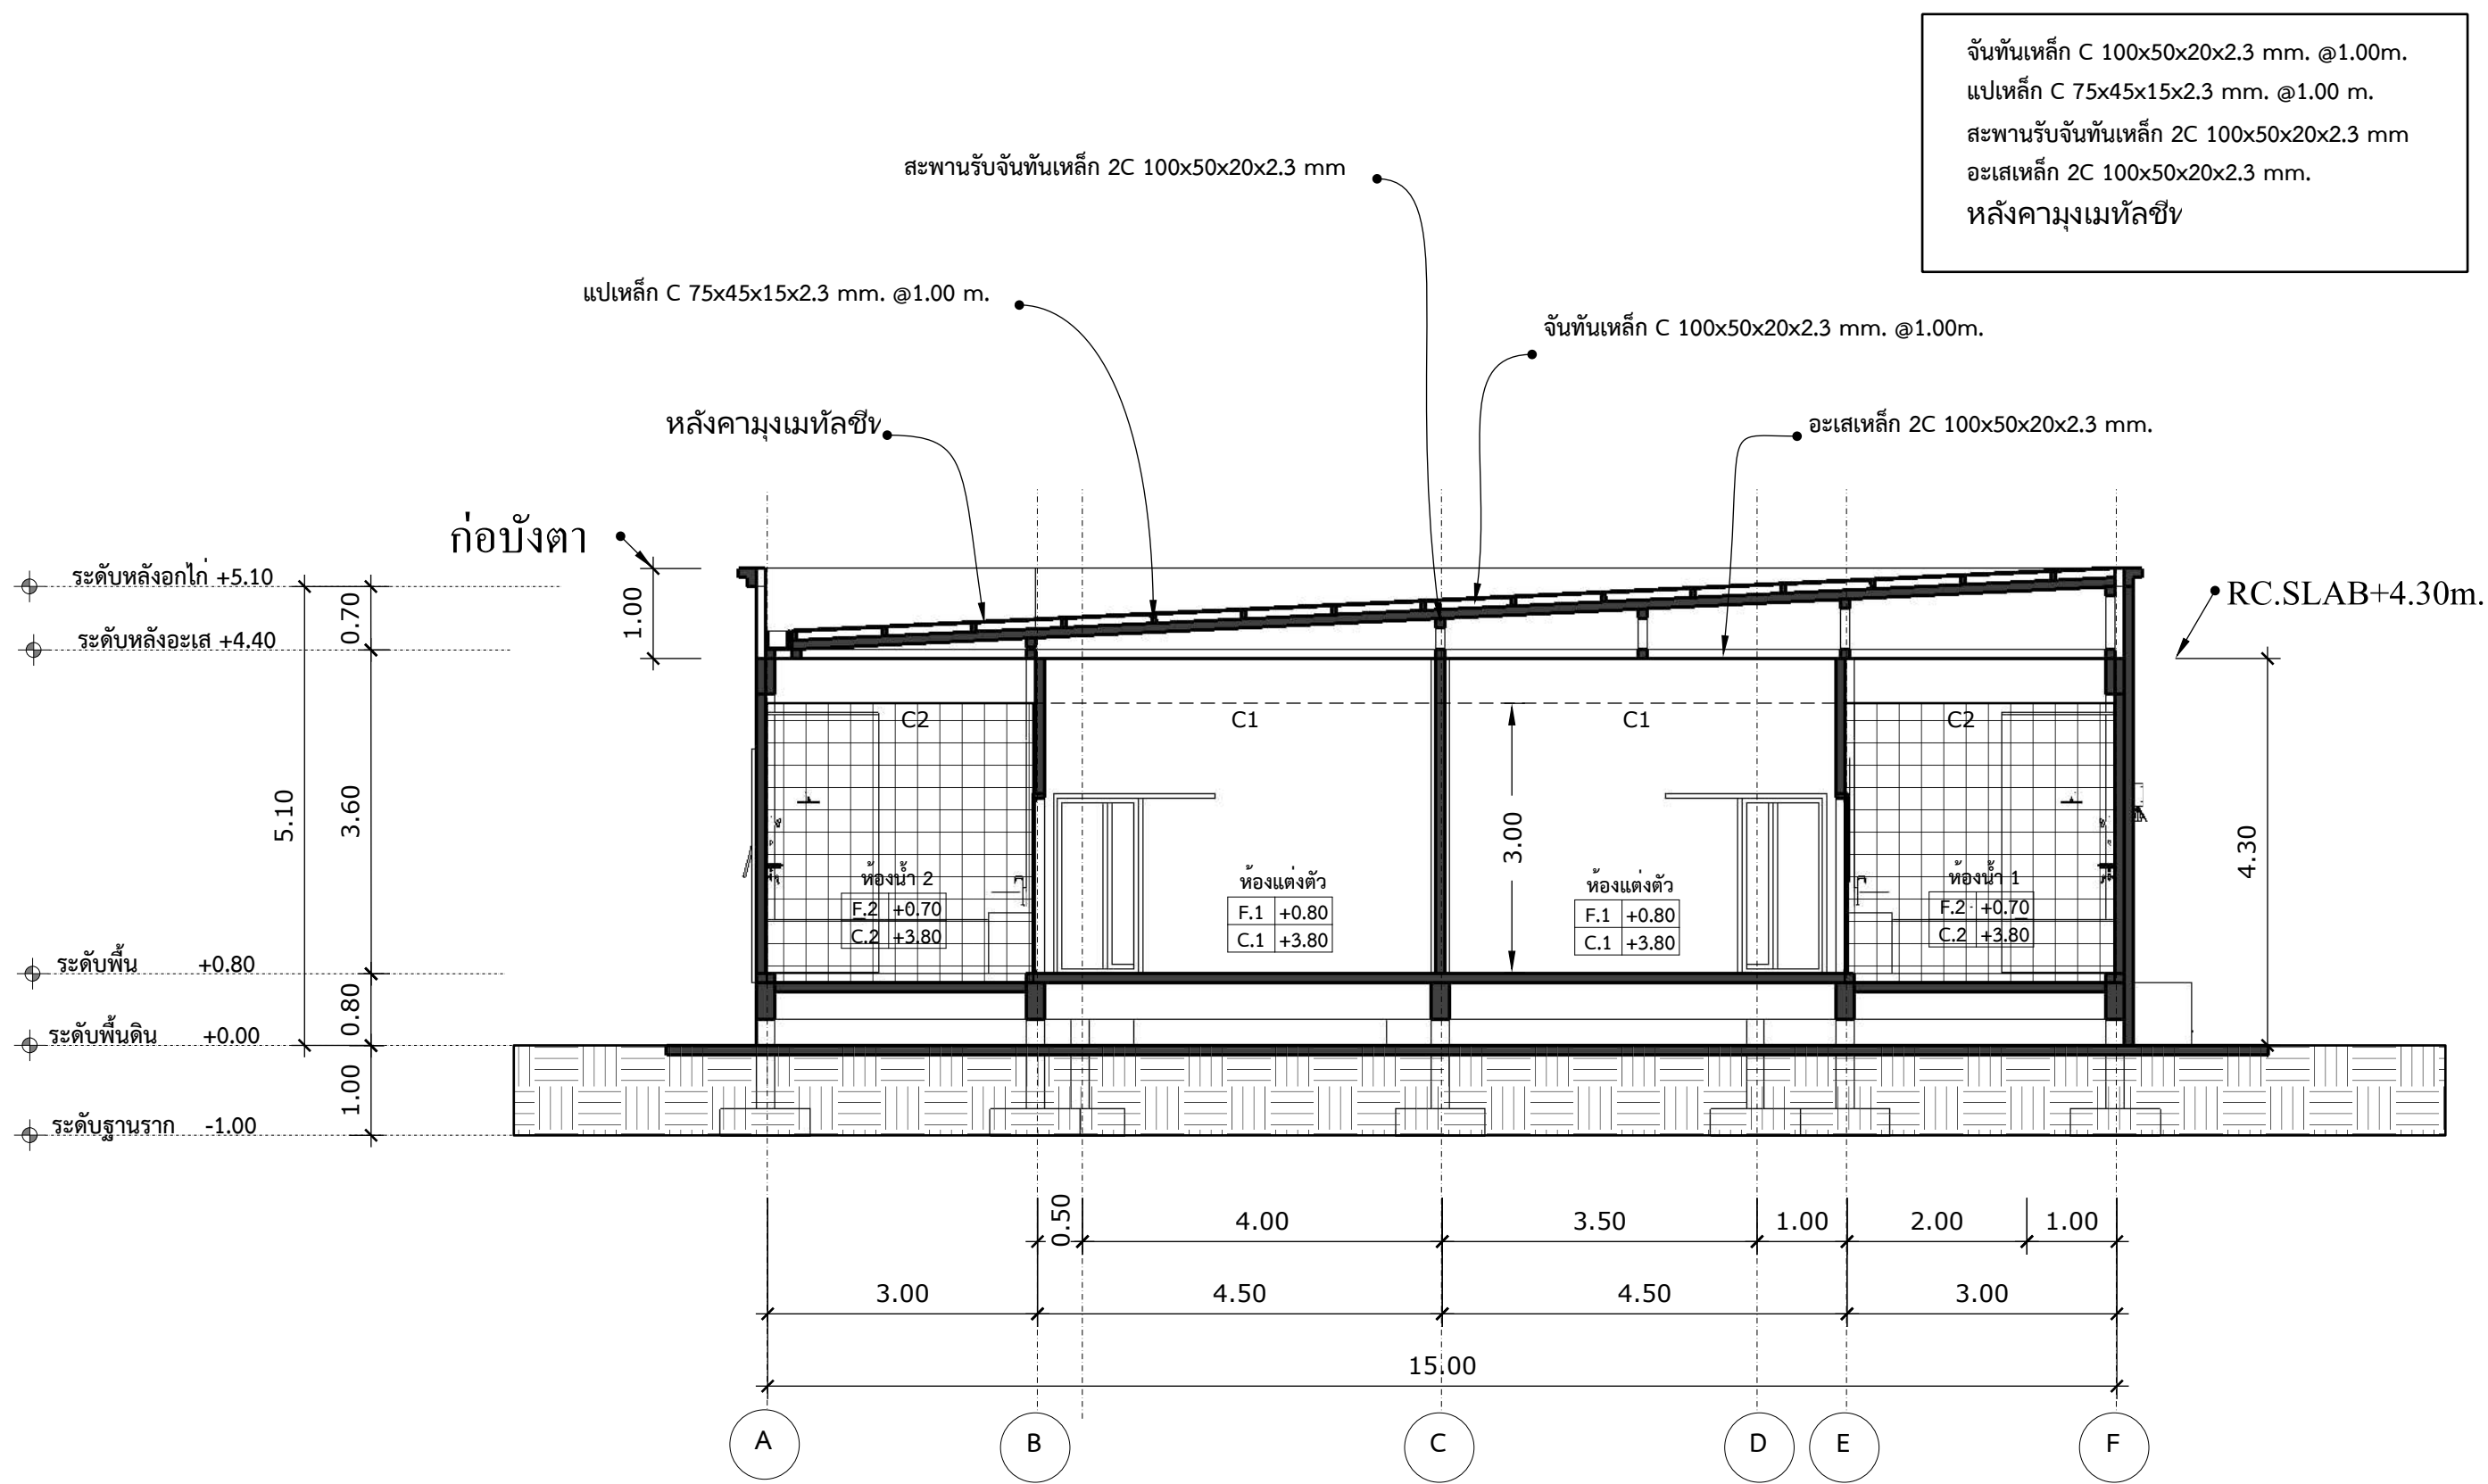


จันทันเหล็ก C 100x50x20x2.3 mm. @1.00m.
แปเหล็ก C 75x45x15x2.3 mm. @1.00 m.
สะพานรับจันทันเหล็ก 2C 100x50x20x2.3 mm
อะเสเหล็ก 2C 100x50x20x2.3 mm.
หลังคามุงเมทัลชีท

ชื่อโครงการ	
โครงการก่อสร้าง อาคารพักอาศัย คสล. 1 ชั้น	
เจ้าของโครงการ	
คุณปรินทร์ เรืองรัตนวนิช	
สถาปนิก	
นายนิกร สุขแสง ภสธ.10581 ถ.แจ้งวัฒนะซอย6 แขวงตลาดบางเขน. เขตหลักสี่. กรุงเทพฯ	
วิศวกรโครงสร้าง	
นายปฐวี เชื้อชม ภย.33663 92 ม. 1 ต.ท่าโพธิ์ศรี อ.เดชอุดม จ.อุบลราชธานี	
วิศวกรไฟฟ้า	
-	
วิศวกรเครื่องกล	
-	
ผู้เขียน	
นายปฐวี เชื้อชม ภย.33663 92 ม. 1 ต.ท่าโพธิ์ศรี อ.เดชอุดม จ.อุบลราชธานี	
ที่ตั้ง	
บ้านไม้จาว ตำบล ป่าตอง อำเภอ กะทู้ จังหวัด ภูเก็ต	
แบบแสดง	
รูปตัด A-A	
FILE NO	DRAWING NO
	13
SUB TOTAL	GRAND TOTAL
DATE	--

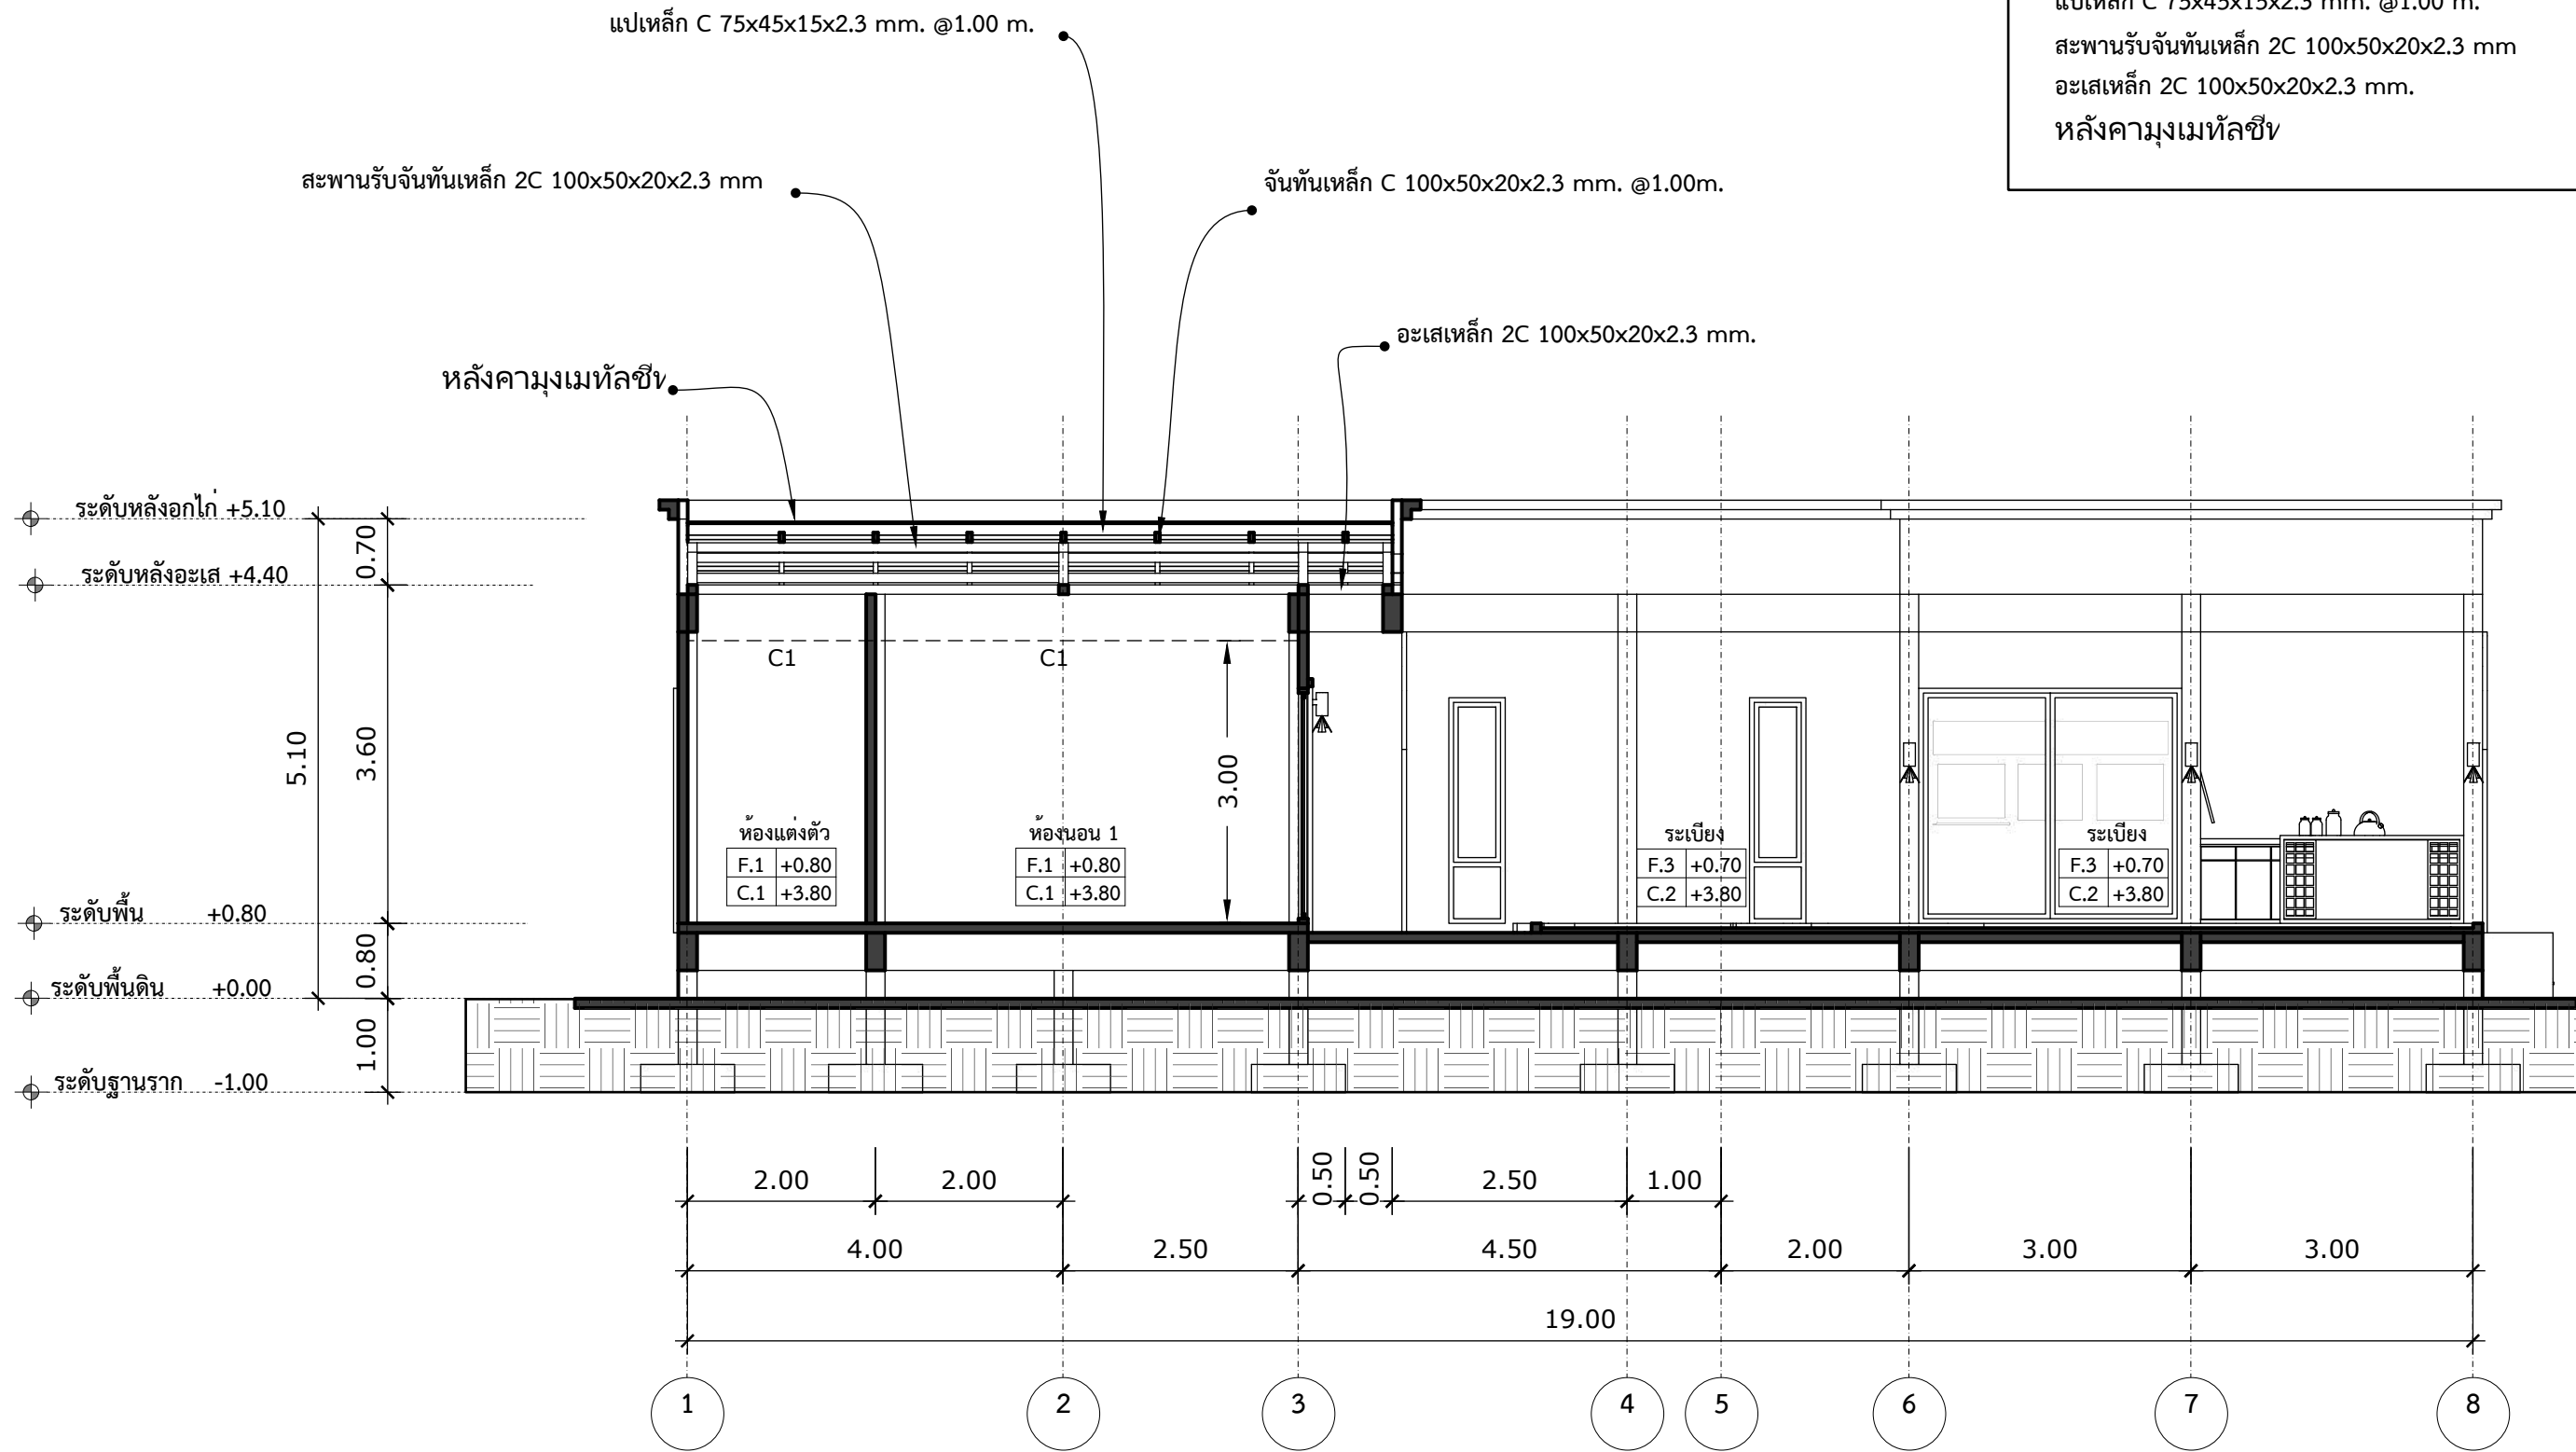






จันทันเหล็ก C 100x50x20x2.3 mm. @1.00m.
แปเหล็ก C 75x45x15x2.3 mm. @1.00 m.
สะพานรับจันทันเหล็ก 2C 100x50x20x2.3 mm
อะเสเหล็ก 2C 100x50x20x2.3 mm.
หลังคามุงเมทัลชีท

ชื่อโครงการ	
โครงการก่อสร้างอาคารพักอาศัย	
คสล. 1 ชั้น	
เจ้าของโครงการ	
คุณปรินทร์ เรืองรัตนวานิช	
สถาปนิก	
นายนิกร สุขแสง ภสธ.10581 ถ.แจ้งวัฒนะซอย6 แขวงตลาดบางเขน. เขตหลักสี่. กรุงเทพฯ	
วิศวกรโครงสร้าง	
นายปฐวี เชื้อชม ภย.33663 92 ม. 1 ต.ท่าโพธิ์ศรี อ.เดชอุดม จ.อุบลราชธานี	
วิศวกรไฟฟ้า	
-	
วิศวกรเครื่องกล	
-	
ผู้เขียน	
นายปฐวี เชื้อชม ภย.33663 92 ม. 1 ต.ท่าโพธิ์ศรี อ.เดชอุดม จ.อุบลราชธานี	
ที่ตั้ง	
บ้านไม้จ้าว ตำบล ป่าตอง อำเภอ กะตุ จังหวัด ภูเก็ต	
แบบแสดง	
รูปตัด B-B	
FILE NO	DRAWING NO
	14
SUB TOTAL	GRAND TOTAL
DATE	--

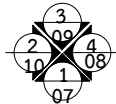

Drawing Title รูปตัด B-B
scale: 1 : 75

A
05

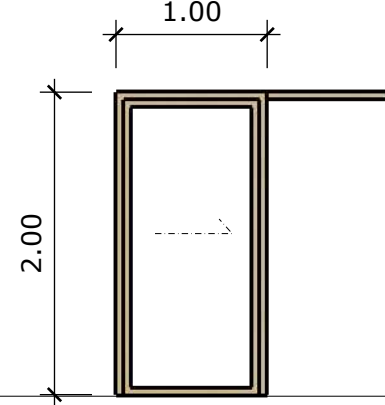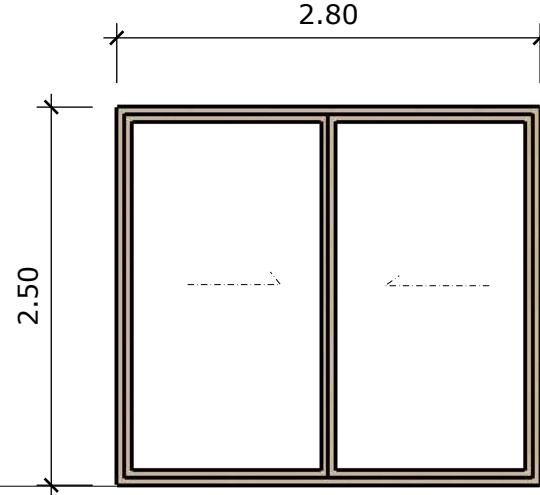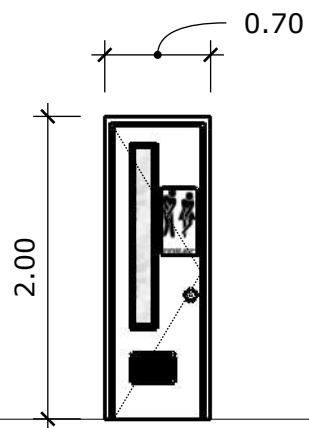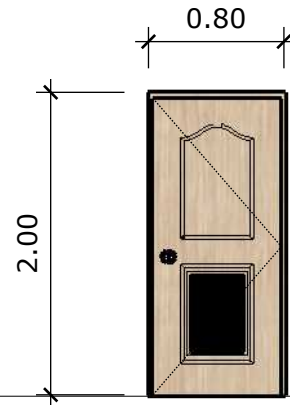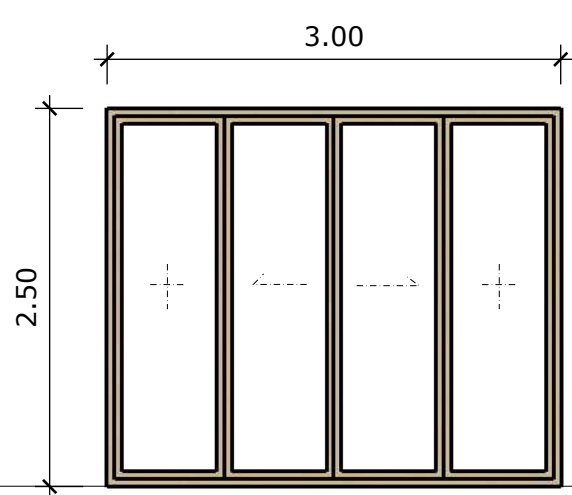

ประตู ①

- | | |
|-------------------|----------------------------|
| ชนิดบาน | - บานเลื่อน |
| วงกบ | - อลูมิเนียมหนา 1.2 มม. |
| กรอบบาน | - อลูมิเนียมหนา 1.2 มม. |
| ลูกฝัก | - กระฉากใส หนา 5 มม. |
| ทำสี/ชนิดผิว | - สีลายไม้ |
| รายละเอียดอุปกรณ์ | - อุปกรณ์ครบชุด ตามผู้ผลิต |

ประตู ②

- | | |
|-------------------|----------------------------|
| ชนิดบาน | - บานเปิดเดียว |
| วงกบ | - UPVC |
| กรอบบาน | - UPVC |
| ลูกฝัก | - |
| ทำสี/ชนิดผิว | - สีทาสี |
| รายละเอียดอุปกรณ์ | - อุปกรณ์ครบชุด ตามผู้ผลิต |

ประตู ③

- | | |
|-------------------|----------------------------|
| ชนิดบาน | - บานเปิดเดียว |
| วงกบ | - UPVC / ไฟเบอร์กลาส |
| กรอบบาน | - UPVC / ไฟเบอร์กลาส |
| ลูกฝัก | - |
| ทำสี/ชนิดผิว | - ตามผู้ผลิต |
| รายละเอียดอุปกรณ์ | - อุปกรณ์ครบชุด ตามผู้ผลิต |

ประตู ④

- | | |
|-------------------|----------------------------|
| ชนิดบาน | - บานเลื่อน |
| วงกบ | - อลูมิเนียมหนา 1.2 มม. |
| กรอบบาน | - อลูมิเนียมหนา 1.2 มม. |
| ลูกฝัก | - กระฉากใส หนา 5 มม. |
| ทำสี/ชนิดผิว | - สีลายไม้ |
| รายละเอียดอุปกรณ์ | - อุปกรณ์ครบชุด ตามผู้ผลิต |

ประตู ⑤





- | | |
|-------------------|----------------------------|
| ชนิดบาน | - บานเลื่อน |
| วงกบ | - อลูมิเนียมหนา 1.2 มม. |
| กรอบบาน | - อลูมิเนียมหนา 1.2 มม. |
| ลูกฝัก | - กระฉากใส หนา 5 มม. |
| ทำสี/ชนิดผิว | - สีลายไม้ |
| รายละเอียดอุปกรณ์ | - อุปกรณ์ครบชุด ตามผู้ผลิต |

Drawing Title :: Door Details

scale: 1 : 50

A

13

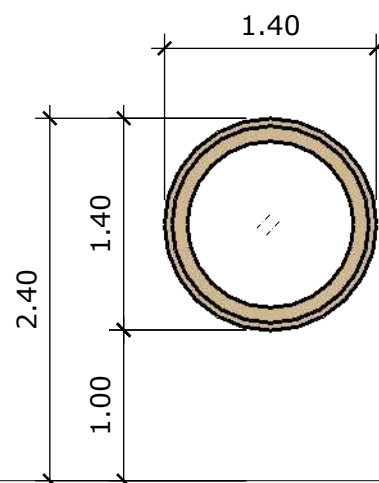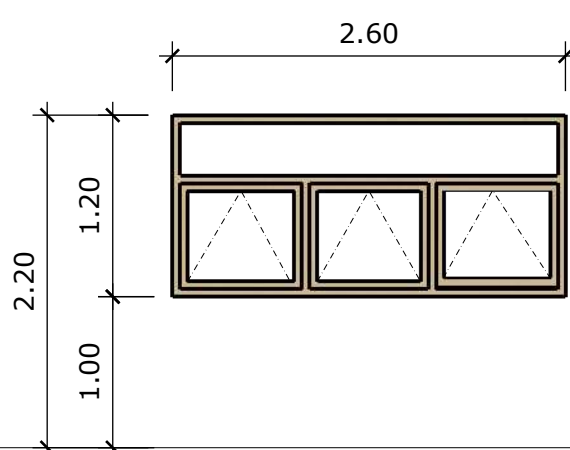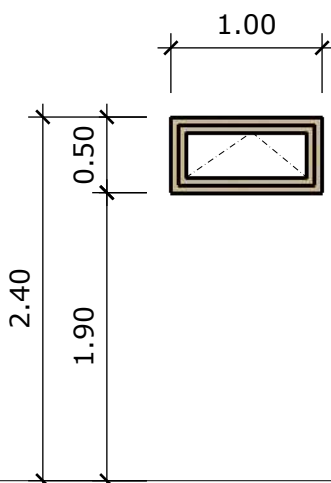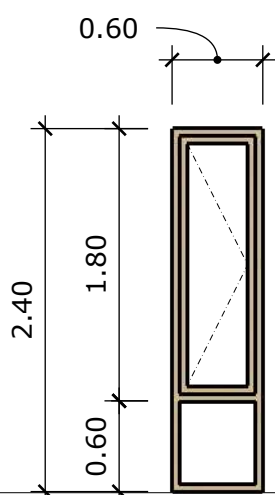

หน้าต่าง ①

- | | |
|-------------------|----------------------------|
| ชนิดบาน | - บานเปิดข้าง |
| วงกบ | - อลูมิเนียมหนา 1.2 มม. |
| กรอบบาน | - อลูมิเนียมหนา 1.2 มม. |
| ลูกฝัก | - กระฉากใส หนา 5 มม. |
| ทำสี/ชนิดผิว | - สีลายไม้ |
| รายละเอียดอุปกรณ์ | - อุปกรณ์ครบชุด ตามผู้ผลิต |

หน้าต่าง ④

- | | |
|-------------------|----------------------------|
| ชนิดบาน | - บานกระทุ้ง |
| วงกบ | - อลูมิเนียมหนา 1.2 มม. |
| กรอบบาน | - อลูมิเนียมหนา 1.2 มม. |
| ลูกฝัก | - กระฉากใส หนา 5 มม. |
| ทำสี/ชนิดผิว | - สีลายไม้ |
| รายละเอียดอุปกรณ์ | - อุปกรณ์ครบชุด ตามผู้ผลิต |

หน้าต่าง ⑤

- | | |
|-------------------|----------------------------|
| ชนิดบาน | - บานกระทุ้ง |
| วงกบ | - อลูมิเนียมหนา 1.2 มม. |
| กรอบบาน | - อลูมิเนียมหนา 1.2 มม. |
| ลูกฝัก | - กระฉากใส หนา 5 มม. |
| ทำสี/ชนิดผิว | - สีลายไม้ |
| รายละเอียดอุปกรณ์ | - อุปกรณ์ครบชุด ตามผู้ผลิต |

หน้าต่าง ⑥

- | | |
|-------------------|----------------------------|
| ชนิดบาน | - บานปิดตาย |
| วงกบ | - อลูมิเนียมหนา 1.2 มม. |
| กรอบบาน | - อลูมิเนียมหนา 1.2 มม. |
| ลูกฝัก | - กระฉากใส หนา 5 มม. |
| ทำสี/ชนิดผิว | - สีลายไม้ |
| รายละเอียดอุปกรณ์ | - อุปกรณ์ครบชุด ตามผู้ผลิต |

Drawing Title :: Window Details

scale: 1 : 50

A

13

ชื่อโครงการ

โครงการก่อสร้าง
อาคารพักอาศัย
คสล. 1 ชั้น

เจ้าของโครงการ

คุณปรินทร์ เรืองรัตนวานิช

สถาปนิก

นายนิกร สุขแสง
ภสธ.10581
ถ.แจ้งวัฒนะซอย6
แขวงตลาดบางเขน.
เขตหลักสี่. กรุงเทพฯ

วิศวกรโครงสร้าง

นายปฐวี เชื้อชม
ภย.33663

92 ม. 1 ต.ท่าโพธิ์ศรี
อ.เดชอุดม จ.อุบลราชธานี

วิศวกรไฟฟ้า

วิศวกรเครื่องกล

ผู้เขียน

นายปฐวี เชื้อชม
ภย.33663

92 ม. 1 ต.ท่าโพธิ์ศรี
อ.เดชอุดม จ.อุบลราชธานี

ที่ตั้ง

บ้านไม้จ้าว
ตำบล ป่าตอง
อำเภอ กะทู้
จังหวัด ภูเก็ต

แบบแสดง

ขยายประตู-ขยายหน้าต่าง

FILE NO


SUB TOTAL

DATE

DRAWING NO


GRAND TOTAL

--

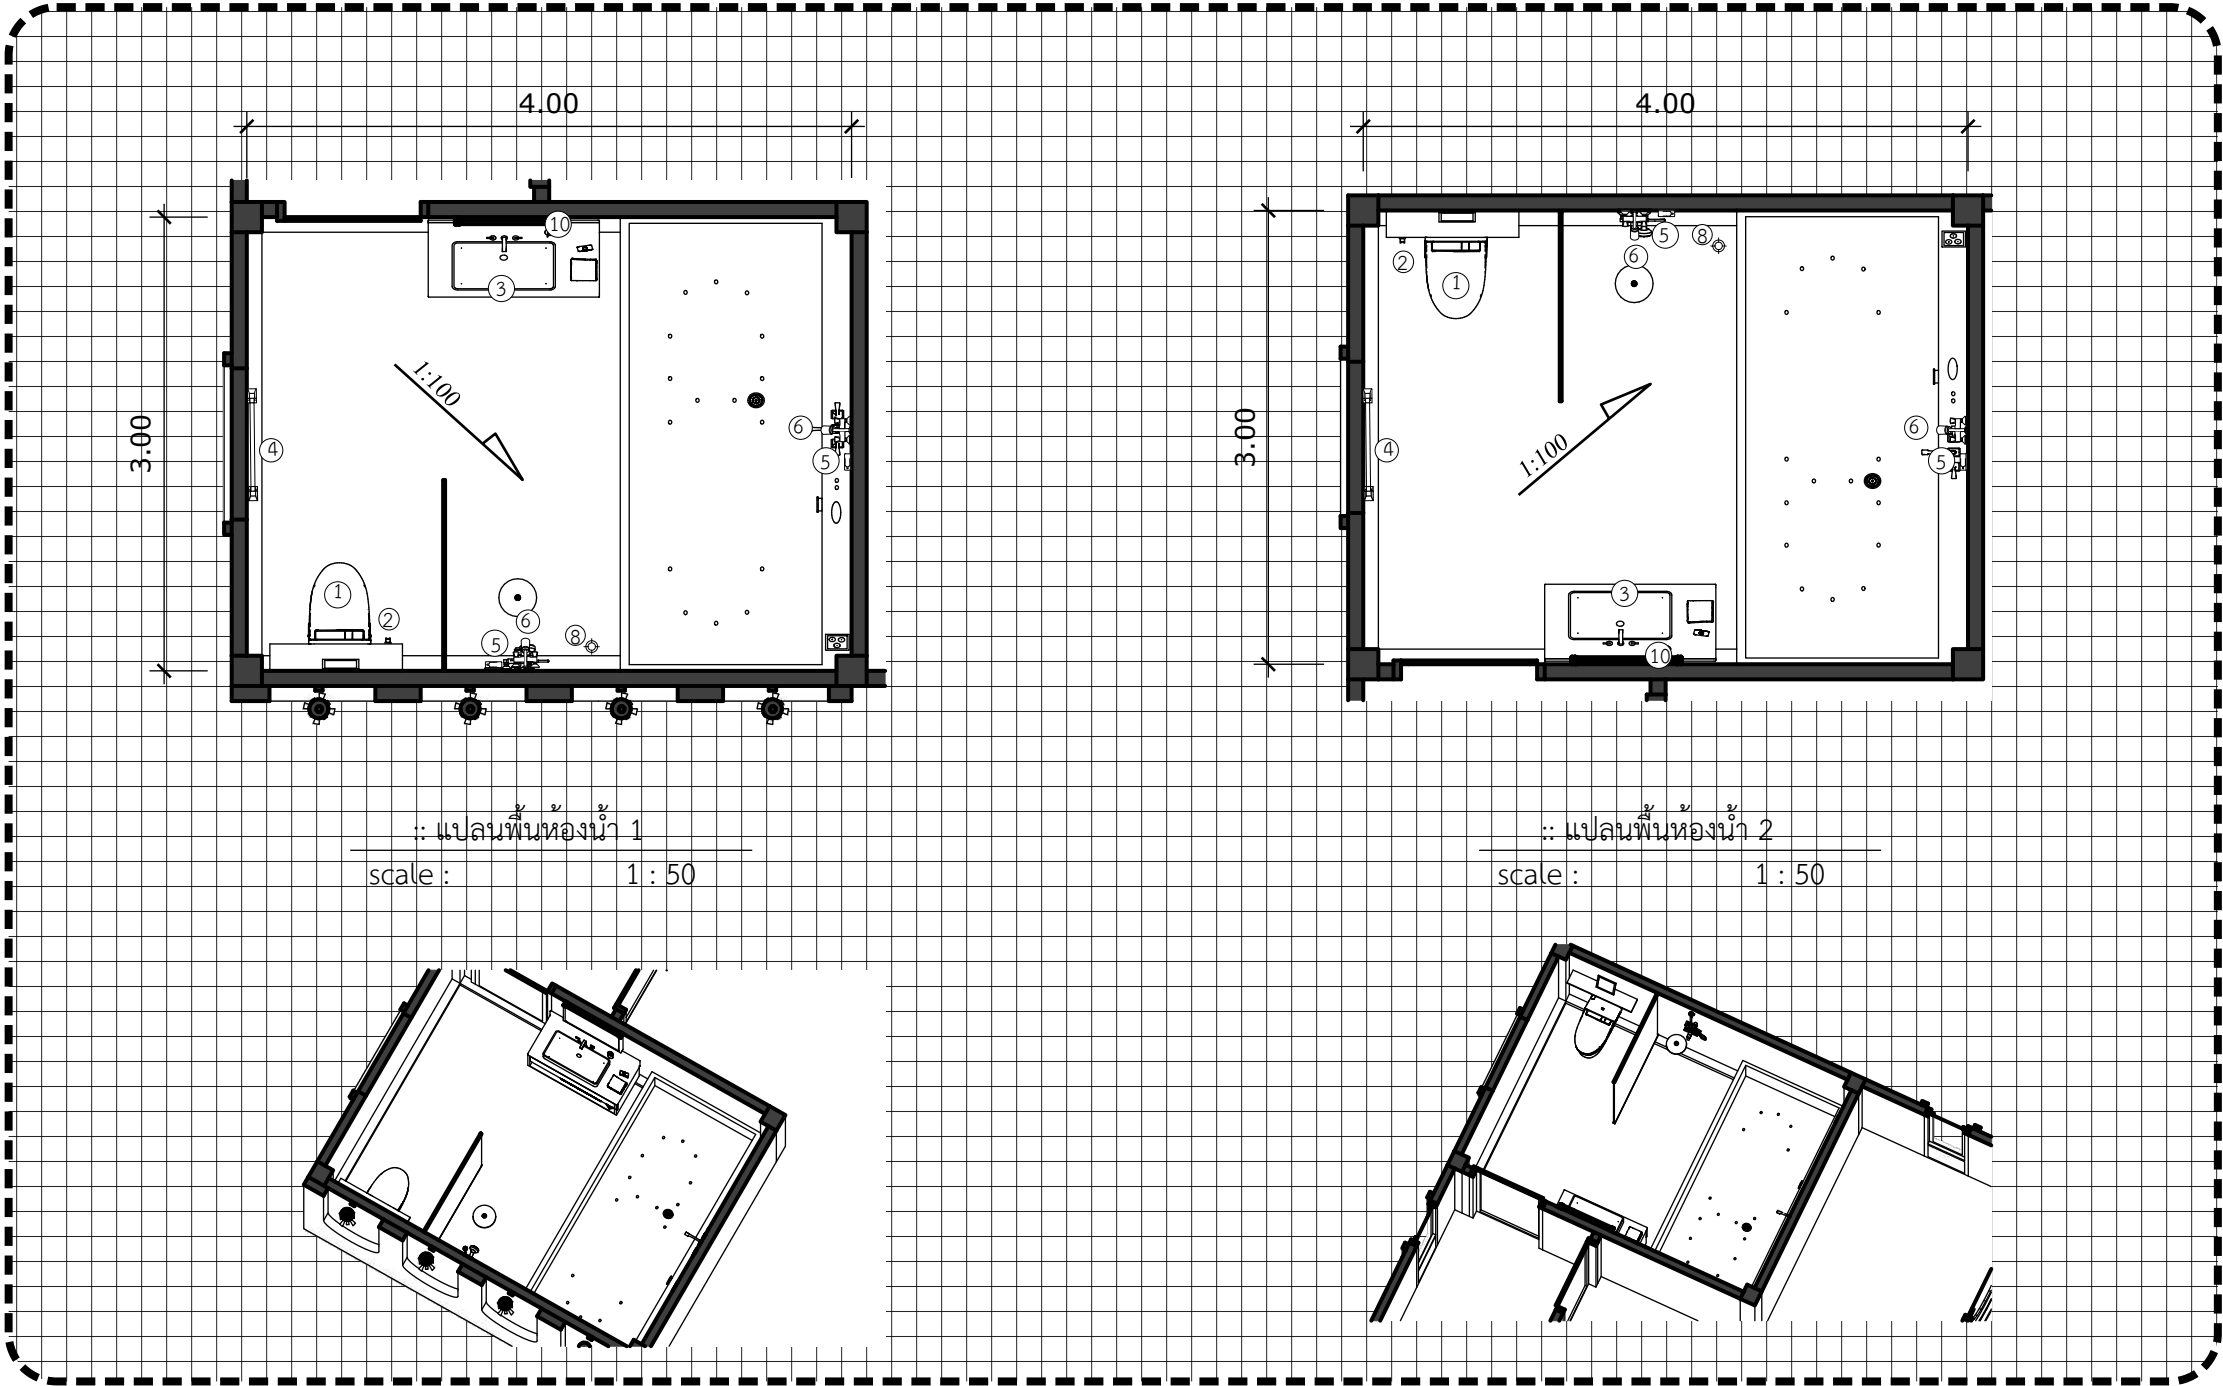

สัญลักษณ์	รายการห้องน้ำ
①	- ชักโครก
②	- ผักบัวฉีดชำระ
③	- อ่างล้างหน้าแขวนผนัง
④	- ราวแขวนสแตนเลส
⑤	- ที่วางสบู่แบบเดี่ยว

สัญลักษณ์	รายการห้องน้ำ
⑥	- ผักบัวพร้อมสาย
⑦	- ที่ใส่กระดาษชำระ
⑧	- ตะแกรงกันก่ลื่นสแตนเลส
⑨	- ก๊อกล้างพื้น
⑩	- กระเบื้อง ขนาด 0.40x0.60 m

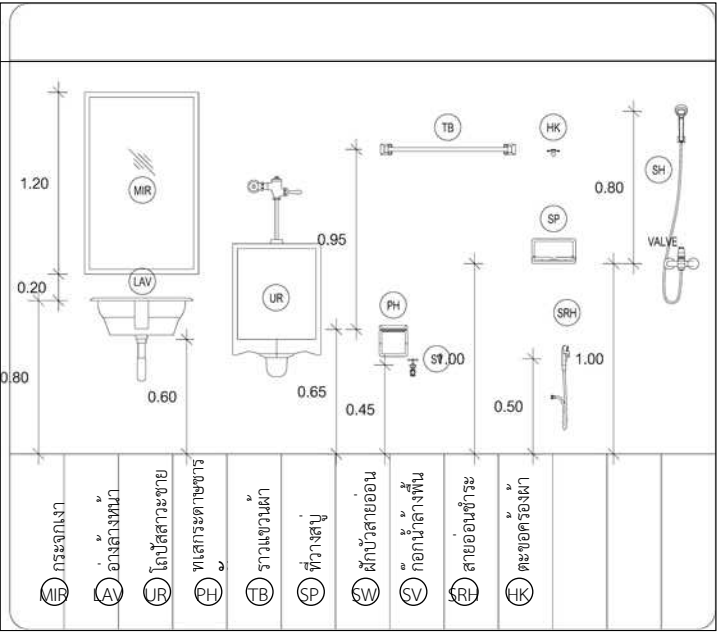

ชื่อโครงการ

โครงการก่อสร้าง
อาคารพักอาศัย
คสล. 1 ชั้น

เจ้าของโครงการ

คุณปรินทร์ เรืองรัตนวานิช

สถาปนิก

.....
นายนิกร สุขแสง
ภสธ.10581
ถ.แจ้งวัฒนะซอย6
แขวงตลาดบางเขน.
เขตหลักสี่. กรุงเทพฯ

วิศวกรโครงสร้าง

.....
นายปฐวี เชื้อชม
ภย.33663

92 ม. 1 ต.ท่าโพธิ์ศรี
อ.เดชอุดม จ.อุบลราชธานี

วิศวกรไฟฟ้า

วิศวกรเครื่องกล

ผู้เขียน

นายปฐวี เชื้อชม
ภย.33663
92 ม. 1 ต.ท่าโพธิ์ศรี
อ.เดชอุดม จ.อุบลราชธานี

ที่ตั้ง

บ้านไม้จ้าว
ตำบล ป่าตอง
อำเภอ กะทู้
จังหวัด ภูเก็ต

แบบแสดง

ขยายห้องน้ำ

FILE NO

DRAWING NO

SUB TOTAL

GRAND TOTAL


DATE

--

รายการประกอบแบบ	
โครงการ	:
สถานที่ตั้งโครงการ	:
เจ้าของโครงการ	:
สถาปนิกออกแบบ	:
วิศวกรออกแบบโครงสร้าง	: นายปฐวี เชื้อชม ทย.33663
ผู้ออกแบบ	อันหมายถึง สถาปนิกและวิศวกรผู้ออกแบบ
มีสิทธิที่จะเข้าทำการตรวจตราการก่อสร้างตามหน้าที่รับผิดชอบเพื่อให้เป็นไปตามรูปแบบและรายการทั้งมีหน้าที่พิจารณาเลือกใช้และตัดสินความถูกต้องของวัสดุอุปกรณ์ที่นำมาใช้ก่อสร้างตลอดจนพิจารณาตัดสินชี้ขาดปัญหาขัดแย้งเกี่ยวกับรูปแบบและรายการเมื่อผู้ออกแบบตัดสินประการใดให้ถือเป็นถูกต้องผู้ว่าจ้างต้องปฏิบัติตามโดยไม่มีเงื่อนไขใดๆผู้ออกแบบมีสิทธิที่จะส่งแบบรายละเอียดเพิ่มเติมให้สมบูรณ์ขึ้นได้ต่องานอันจำเป็นต้องการทำตามวิธีการ และหลักการวิชาช่างอันจะขาดเสียมิได้โดยจะต้องผ่านผู้ออกแบบเสียก่อนและเมื่อผู้ออกแบบเห็นชอบแล้วผู้ว่าจ้างต้องปฏิบัติตาม โดยถือเป็นงานเพิ่มเติมให้กับผู้รับจ้าง	
ลักษณะงาน	อาคารพักอาศัยชั้นเดียวปลูกสร้างในที่ดิน
ระดับอ้างอิง	ค่าระดับ ระยะและขนาดต่าง ๆ ในแบบกำหนดหน่วยเป็นเมตร
นอกจากกำหนดไว้เป็นอย่างอื่น ค่าระดับ +0.00 ม. ให้ยึดตามแบบแปลนคือ ระดับทางเท้า คสล.	
ภายในโครงการหากมีข้อขัดแย้งกันหรือไม่ละเอียดแจ่มชัด ให้ถือตามรูปแบบก่อสร้างนี้เป็นข้อยุติ	
หรือให้อยู่ในดุลยพินิจของสถาปนิกหรือวิศวกรเป็นผู้วินิจฉัย ให้ผู้รับจ้างจัดหาแรงงาน	
วัสดุก่อสร้างและอุปกรณ์เครื่องมือเครื่องใช้ที่ดีมีคุณภาพ	
ลักษณะอาคาร	ฐานรากขนาดและจำนวนตามที่แสดงในแบบแปลน
ฐานราก เป็นฐานคอนกรีตเสริมเหล็ก ขนาดและระดับตามที่แสดงในแบบ	
คาน เป็นคานคอนกรีตเสริมเหล็ก	
เสา เป็นเสาคอนกรีตเสริมเหล็ก	
พื้น พื้นหล่อในที่ หรือพื้นสำเร็จรูป ตามที่แสดงในแบบแปลน	
รายการมาตรฐานก่อสร้าง	
งานฐานราก	ก่อนทำฐานรากผู้รับจ้างต้องเตรียมพื้นที่ ถม ขุด อัด
และปรับระดับดินให้เรียบร่อยและสถาปนิก วิศวกร	
ตรวจสอบระดับผังความแนอนของดินจนได้เกณฑ์ตามที่กำหนด	
และได้อนุมัติจากผู้ควบคุมงานเสียก่อนจึงจะดำเนินการก่อสร้างต่อไป	
งานคอนกรีตเสริมเหล็ก รายละเอียดเกี่ยวกับงาน ค.ส.ล. ซึ่งไม่ได้ระบุในแบบและบทกำหนดนี้	
ให้ถือปฏิบัติตามมาตรฐานสำหรับงานคอนกรีตเสริมเหล็กของวิศวกรรมสถานแห่งประเทศไทย	
อัตราส่วนผสมคอนกรีต คอนกรีตจะต้องมีกำลังอัดไม่น้อยกว่า 210 กก./ตร.ซม. โดยคิดที่อายุ 28 วัน	
ทั้งนี้ให้ใช้แท่งกระบอกเส้นผ่าศูนย์กลาง 15 ซม. สูง 30 ซม.ปอร์ตแลนด์ ประเภท 1 ตาม มอก.	
16/2524คอนกรีตหยาบ ปูนซีเมนต์ : หวาย : หิน = 1 : 3 : 5	
ปูนซีเมนต์	ใช้ปอร์ตแลนด์ซีเมนต์ ประเภท 1 (ตราช้าง , ตราเพชร)
หิน	ใช้เป็นหินม่ ขนาด 3/4" - 1" โดยใช้ตามความเหมาะสมของสภาพงาน
ตามหลักวิชาช่างที่ดี	
ทราย	ใช้เป็นทรายน้ำจืด มีความสะอาด ปราศจากสิ่งปลอมปนและวัชพืช


รายการประกอบแบบ	
เหล็กเสริม	
- เหล็กเสริมที่มีขนาดเส้นผ่าศูนย์กลาง 6 มม. และ 9 มม. เป็นเหล็กเส้นกลม SR - 24 ที่มีกำลังคลากต่ำสุด (fy) ไม่น้อยกว่า 2,400 กก./ตร.ซม. หรือใช้สัญลักษณ์ RB ... แทน และต้องได้มาตรฐาน มอก. 20/2527	
- เหล็กเสริมที่มีขนาดเส้นผ่าศูนย์กลาง 12 - 32 มม. เป็นเหล็กเส้นข้ออ้อย SD - 30 ที่มีกำลังคลากต่ำสุด (fy) ไม่น้อยกว่า 3,000 กก./ตร.ซม. หรือใช้สัญลักษณ์ DB16 แทน และต้องได้มาตรฐาน มอก. 24 - 2527	
- การต่อเหล็กเสริมในส่วนใด ๆ ของโครงสร้าง ห้ามมิให้ต่อเหล็กในตำแหน่งที่รับแรงดึงสูงสุด	
ให้ต่อตามในแบบหรือตามตำแหน่งต่อไปนี้	
พื้นและผนัง ตามที่เห็นสมควรโดยวิศวกร	
คานและตง เหล็กบนต่อกึ่งกลางช่วงคาน	
เหล็กล่างต่อเหนือเสา หรือที่รองรับจนถึง 1/5 ของช่วงคาน	
เสา 5 ซม. จากพื้นจนถึงครึ่งของความสูงของเสา	
- ระยะทาบของเหล็กเสริมให้ใช้ดังนี้	
เหล็ก SR-24 ระยะทาบไม่น้อยกว่า 48 เท่าของเส้นผ่าศูนย์กลาง = RB6,RB9 และ RB12 mm.	
เหล็ก SD-30 เหล็กบนของคานระยะทาบไม่น้อยกว่า 40 เท่าของเส้นผ่าศูนย์กลาง DB12 mm.ขึ้นไป	
เหล็กล่างของ คาน พื้น ผนัง และระยะทาบไม่น้อยกว่า 38 เท่าของเส้นผ่าศูนย์กลาง	
- ความหนาของคอนกรีตหุ้มเหล็กเสริม นอกจากที่ระบุในแบบไว้เป็นอย่างอื่น ควรจะเป็นไปตามรายการ ดังนี้	
1.5 ซม. สำหรับพื้น	
2.5 ซม. สำหรับคานทั่วไป	
3.0 ซม. สำหรับเสา	
3.5 ซม. สำหรับคานที่ติดกับดิน	
5.0 ซม. สำหรับฐานราก	
- สิ่งต่าง ๆ ที่ต้องการฝังในคอนกรีตเช่น ANCHOR BOLTS,LUGS,PIPES	
ต้องติดตั้งอยู่ในแบบให้เรียบร่อยและมั่นคง ก่อนเทคอนกรีตเสมอ	
- รุและร่องต่าง ๆ ต้องทำช่องหรือใส่ท่อปลอกเหล็กติดกับแบบให้มั่นคงและถูกต้อง ก่อนเทคอนกรีตเสมอ	
แบบหล่อ	
การประกอบต้องได้ตั้งและฉากระดับตามแบบก่อสร้าง	
ทุกมุมต้องสนิทไม่ให้น้ำปูนไหลออกมาได้แบบต้องค้ำยันหนาแน่นแข็งแรงสามารถรับน้ำหนักคอนกรีตได้	
ผิวแบบต้องทาด้วยน้ำยาทาแบบก่อนการวางเหล็กเสริมทุกครั้งการเทคอนกรีตต้องทำให้แน่นทุกจุด	
โดยใช้เหล็กกระทุ้งหรือเขี่ยคอนกรีต คอนกรีตที่ผสมไว้	
การเท	
นานเกิน 30 นาที และตกหล่นตามพื้น ห้ามนำมาใช้ในการก่อสร้าง	
ก่อนเทพื้นบนทรายอัดแน่นให้ปูแผ่นพลาสติกชนิดหนารองพื้นก่อน 1 ชั้น โดยตลอดเพื่อกันความชื้นจากชั้นดิน	
พื้นและผนังที่ต้องบุด้วยวัสดุอื่นนั้น จะคลาดเคลื่อนเกิน 2 มม.ไม่ได้	
และพื้นที่ส่วนใดที่ลาดเอียงให้แต่งให้ได้ตามความลาดเอียงของแบบ	
การบ่มคอนกรีต	
เมื่อหน้าคอนกรีตเริ่มหมาดอยู่ในระยะแข็งตัวจะต้องป้องกันอันตรายจากการถูกแดด ลมร้อน น้ำไหล	
หรือการบรรทุกน้ำหนักที่เกินสมควร เมื่อคอนกรีตพื้นระยะเกิน 24 ชั่วโมง ต้องจัดการให้คอนกรีตเปียกชุ่มน้ำ	
ติดต่อกันอย่างน้อย 7 วัน	

ชื่อโครงการ	
โครงการก่อสร้างอาคารพักอาศัย คสล. 1 ชั้น	
เจ้าของโครงการ	
คุณปรินทร์ เรืองรัตนวานิช	
สถาปนิก	
นายนิกร สุขสว่าง	
ภสธ.10581	
ถ.แจ้งวัฒนะซอย6	
แขวงตลาดบางเขน.	
เขตหลักสี่. กรุงเทพฯ	
วิศวกรโครงสร้าง	
นายปฐวี เชื้อชม	
ทย.33663	
92 ม. 1 ต.ท่าโพธิ์ศรี	
อ.เดชอุดม จ.อุบลราชธานี	
วิศวกรไฟฟ้า	
-	
วิศวกรเครื่องกล	
-	
ผู้เขียน	
นายปฐวี เชื้อชม	
ทย.33663	
92 ม. 1 ต.ท่าโพธิ์ศรี	
อ.เดชอุดม จ.อุบลราชธานี	
ที่ตั้ง	
บ้านไม้จ้าว	
ตำบล ป่าตอง	
อำเภอ กะตุ	
จังหวัด ภูเก็ต	
แบบแสดง	
รายการประกอบแบบโครงสร้าง	
FILE NO	DRAWING NO
	17
SUB TOTAL	GRAND TOTAL
DATE	--

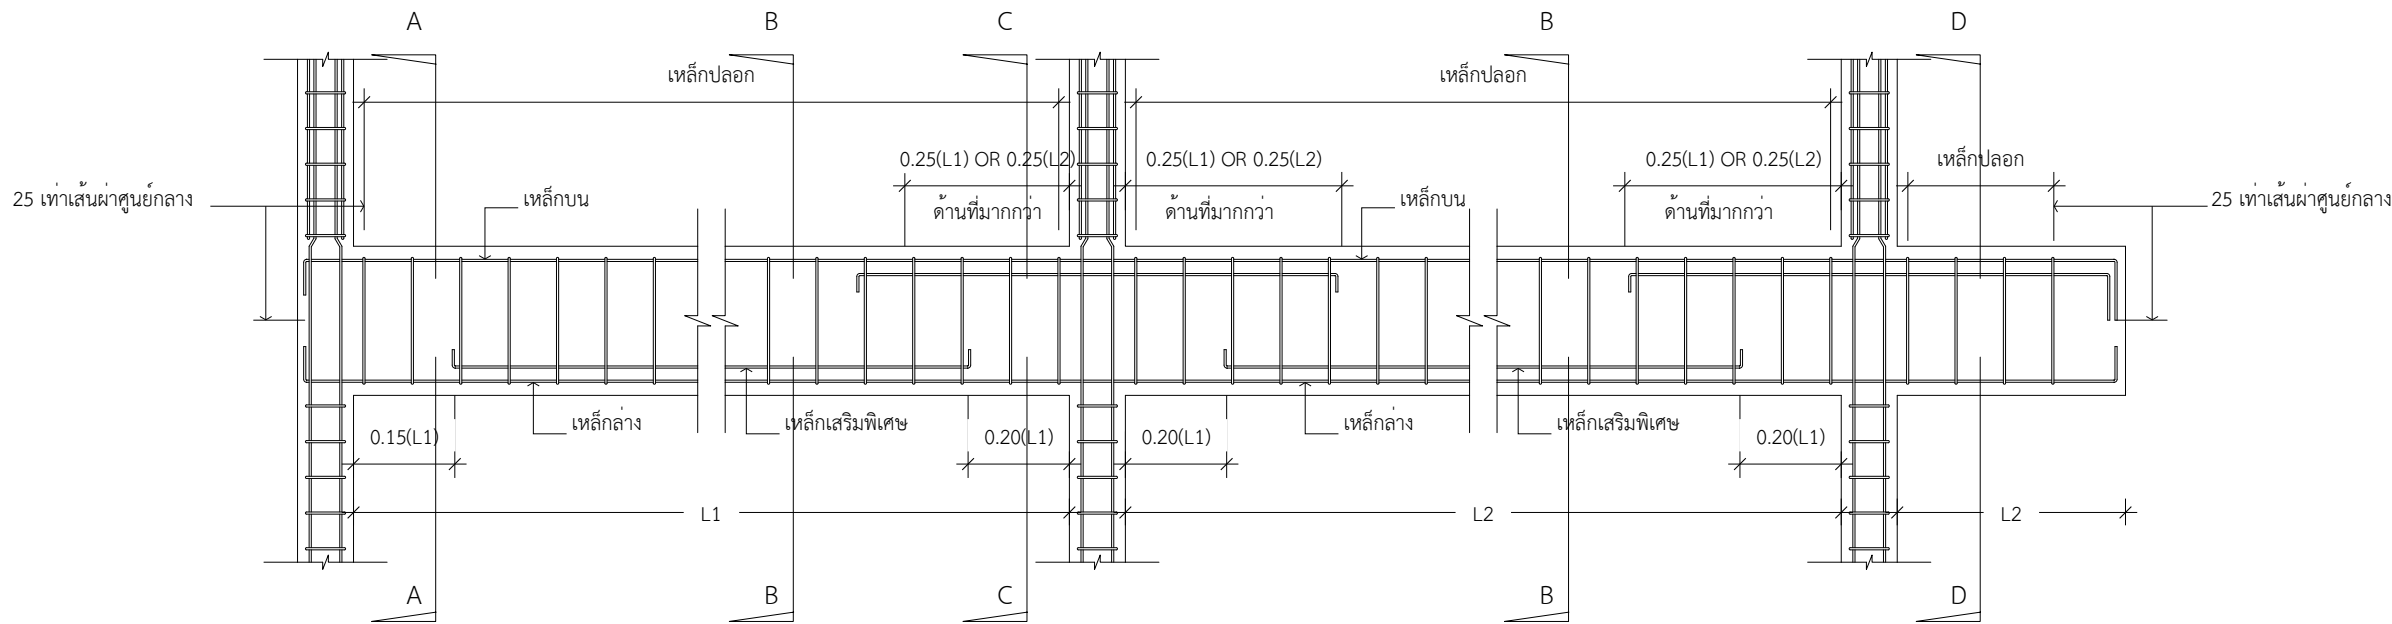


Drawing Title :: มาตรฐานแบบการเปลี่ยนเหล็กเสริมคาน
scale: No Scale

S

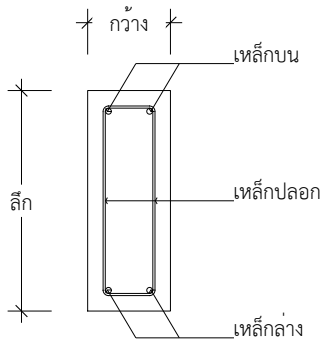


Drawing Title :: รูปตัด A-A
scale: No Scale

S

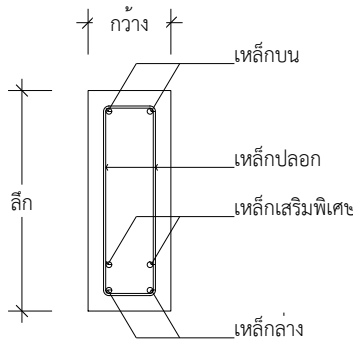


Drawing Title :: รูปตัด B-B
scale: No Scale

S

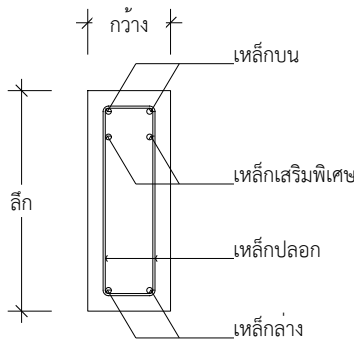


Drawing Title :: รูปตัด C-C
scale: No Scale

S

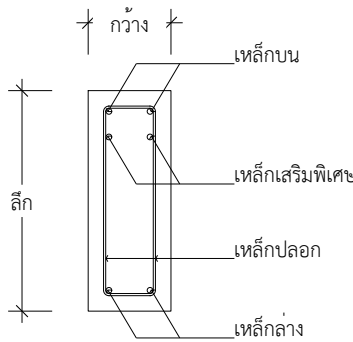

Drawing Title :: รูปตัด D-D
scale: No Scale

S

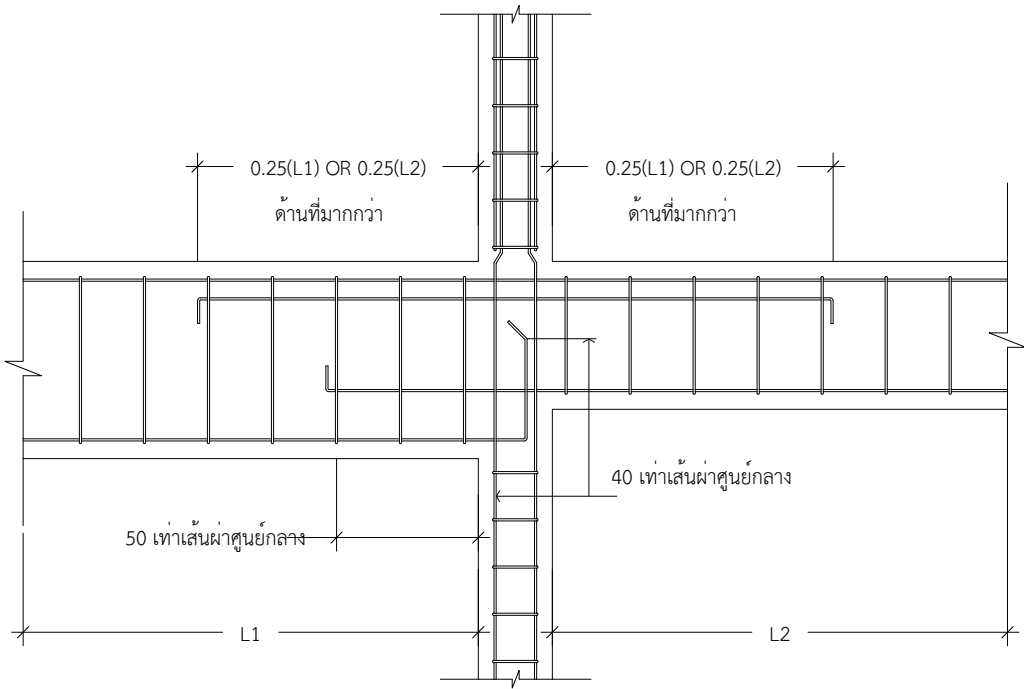

Drawing Title :: มาตรฐานการเปลี่ยนขนาดคาน
scale: No Scale

S

ชื่อโครงการ

โครงการก่อสร้าง
อาคารพักอาศัย
คสล. 1 ชั้น

เจ้าของโครงการ

คุณปรินทร์ เรืองรัตนวานิช

สถาปนิก

นายนิกร สุขแสง
ภสธ.10581
ถ.แจ้งวัฒนะซอย6
แขวงตลาดบางเขน.
เขตหลักสี่. กรุงเทพฯ

วิศวกรโครงสร้าง

นายปฐวี เชื้อชม
ภย.33663

92 ม. 1 ต.ท่าโพธิ์ศรี
อ.เดชอุดม จ.อุบลราชธานี

วิศวกรไฟฟ้า

วิศวกรเครื่องกล

ผู้เขียน

นายปฐวี เชื้อชม
ภย.33663
92 ม. 1 ต.ท่าโพธิ์ศรี
อ.เดชอุดม จ.อุบลราชธานี

ที่ตั้ง

บ้านไม้จ้าว
ตำบล ป่าตอง
อำเภอ กะตุ
จังหวัด ภูเก็ต

แบบแสดง

การเสริมเหล็กโครงสร้างคาน

FILE NO



SUB TOTAL

DATE

DRAWING NO

GRAND TOTAL

--

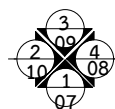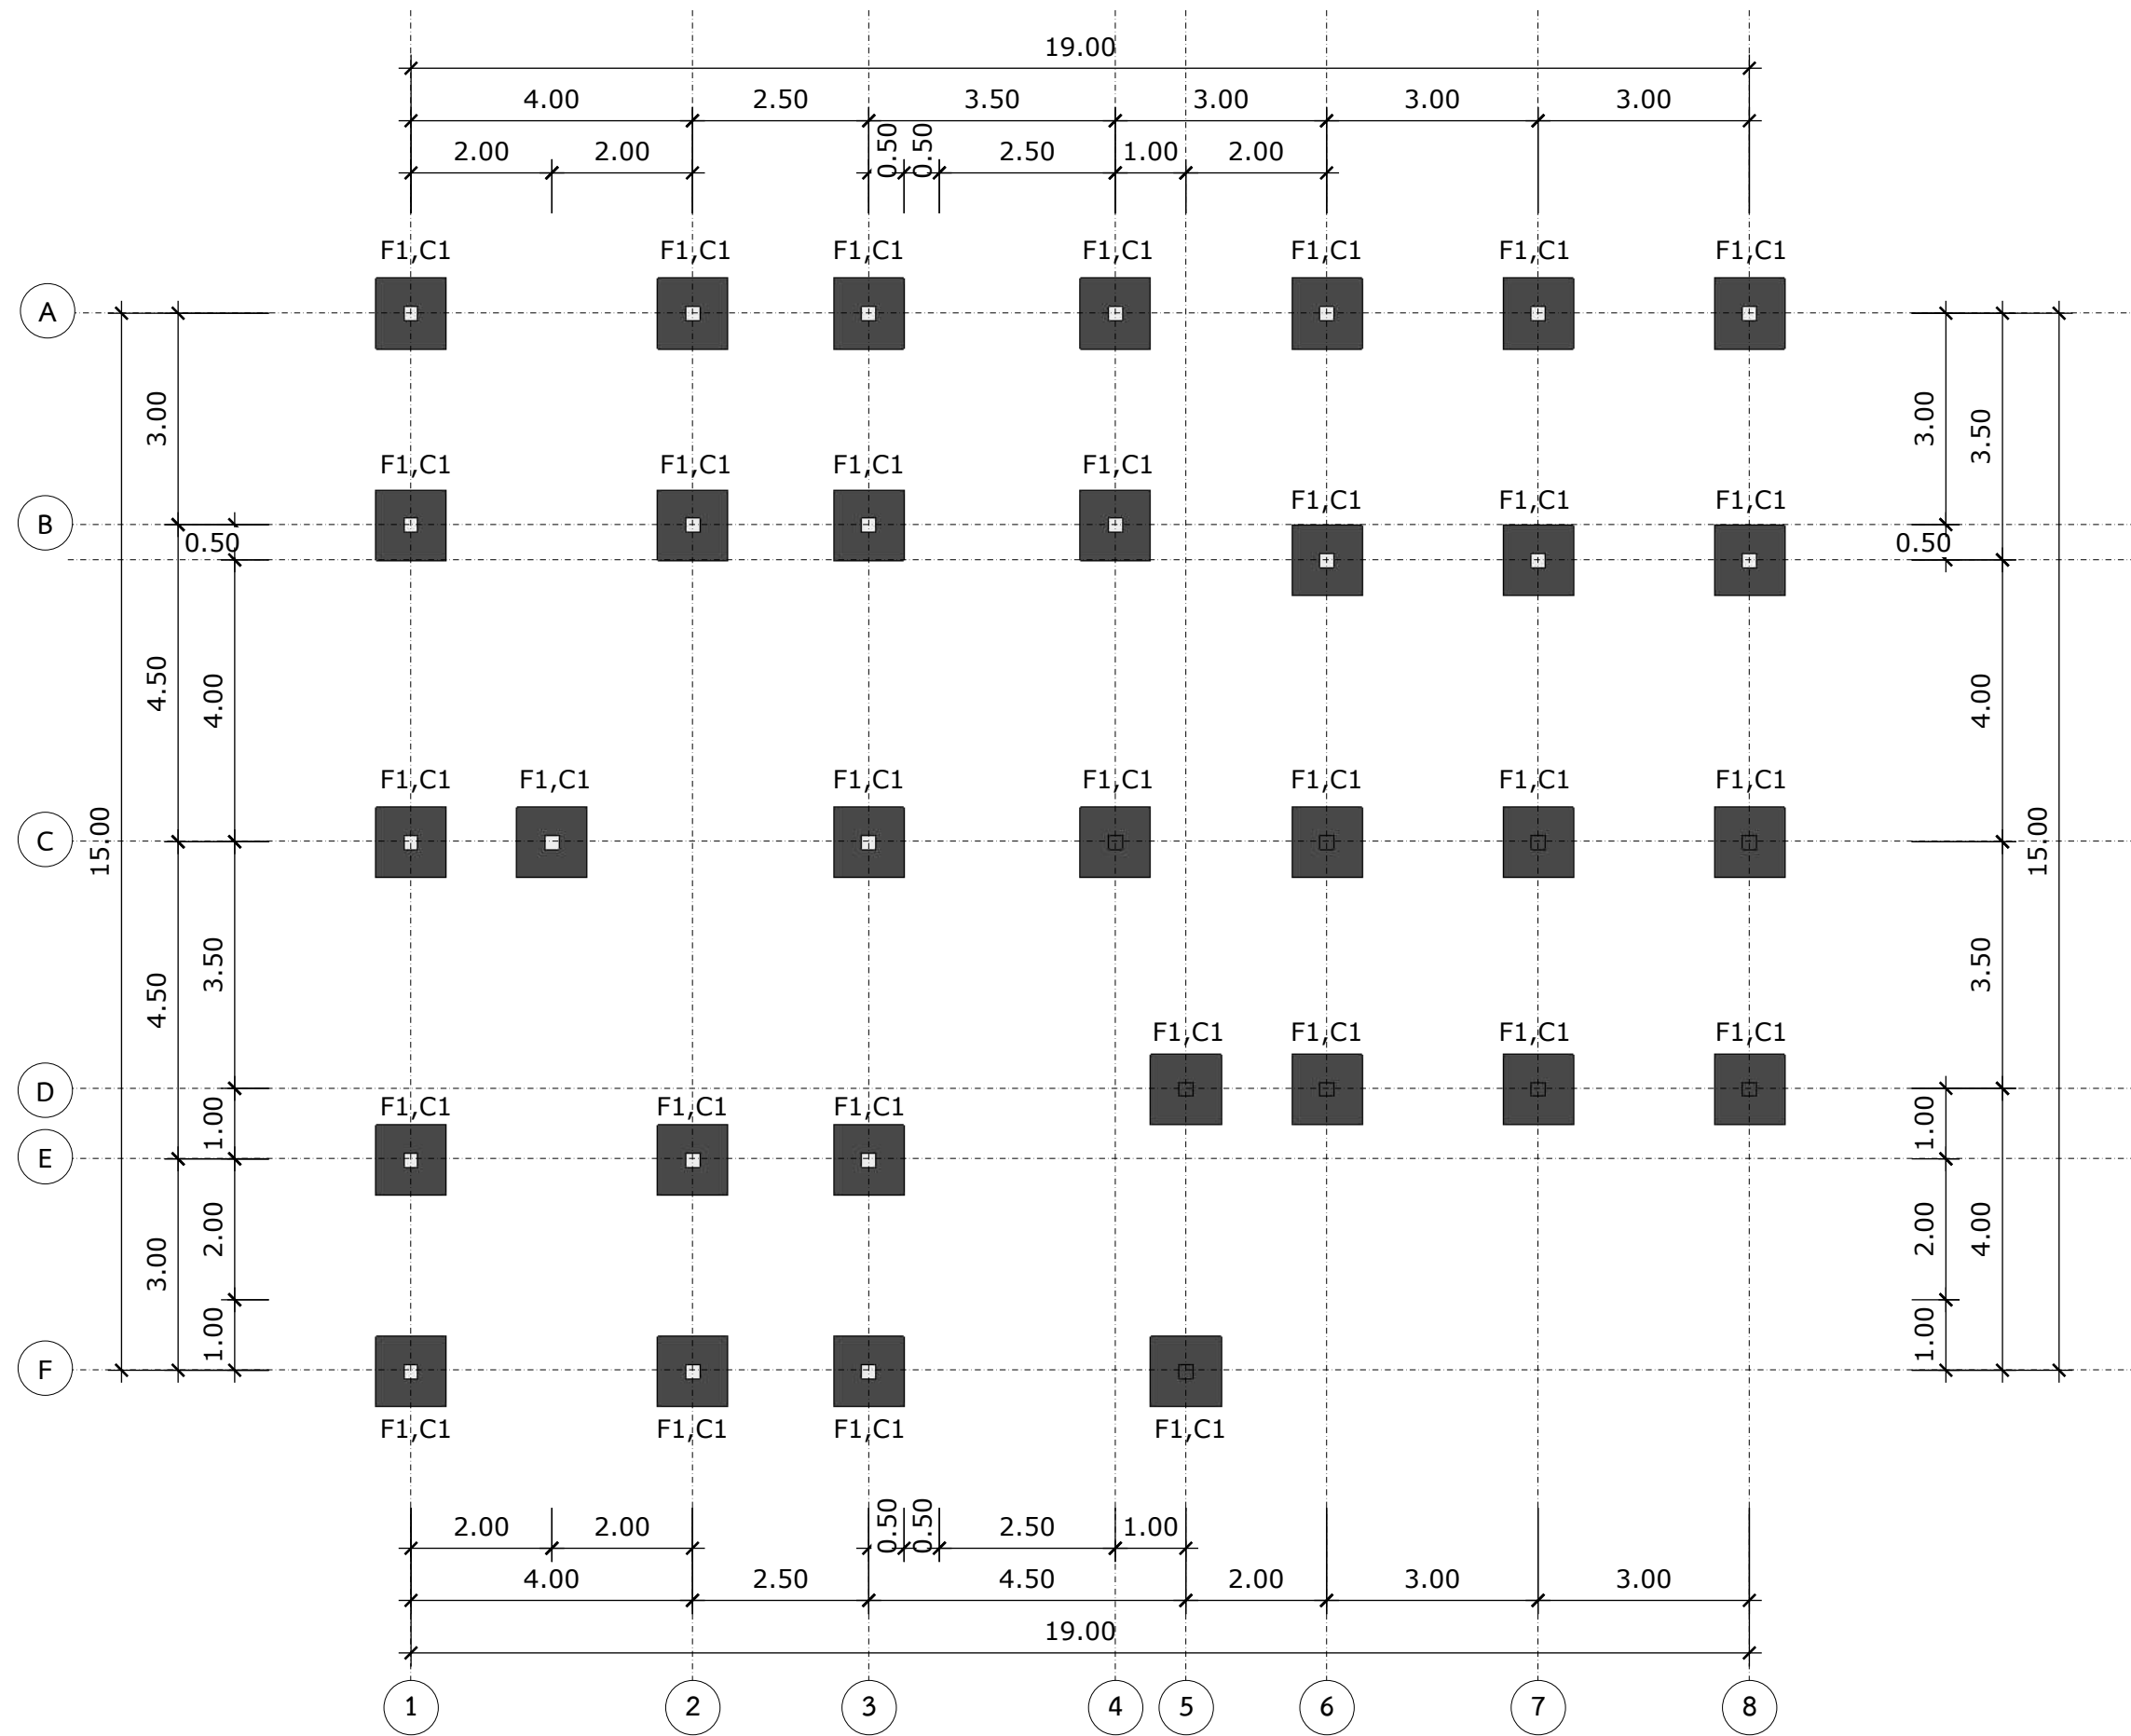

Drawing Title :: แปลนฐานราก,ตอม่อ + คาน + 0.10
scale: 1 : 100

A
05

ชื่อโครงการ
โครงการก่อสร้าง
อาคารพักอาศัย
คสล. 1 ชั้น

เจ้าของโครงการ
คุณปรินทร์ เรืองรัตนวณิช

สถาปนิก
นายนิกร สุขแสง
ภสธ.10581
ถ.แจ้งวัฒนะซอย6
แขวงตลาดบางเขน.
เขตหลักสี่. กรุงเทพฯ

วิศวกรโครงสร้าง
นายปฐวี เชื้อชม
ภย.33663
92 ม. 1 ต.ท่าโพธิ์ศรี
อ.เดชอุดม จ.อุบลราชธานี

วิศวกรไฟฟ้า
-



วิศวกรเครื่องกล
-

ผู้เขียน
นายปฐวี เชื้อชม
ภย.33663
92 ม. 1 ต.ท่าโพธิ์ศรี
อ.เดชอุดม จ.อุบลราชธานี

ที่ตั้ง
บ้านไม้จ้าว
ตำบล ป่าตอง
อำเภอ กะทู้
จังหวัด ภูเก็ต

แบบแสดง
แปลนฐานราก-ตอม่อ

FILE NO	DRAWING NO
	19
SUB TOTAL	GRAND TOTAL
DATE	--

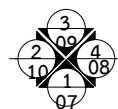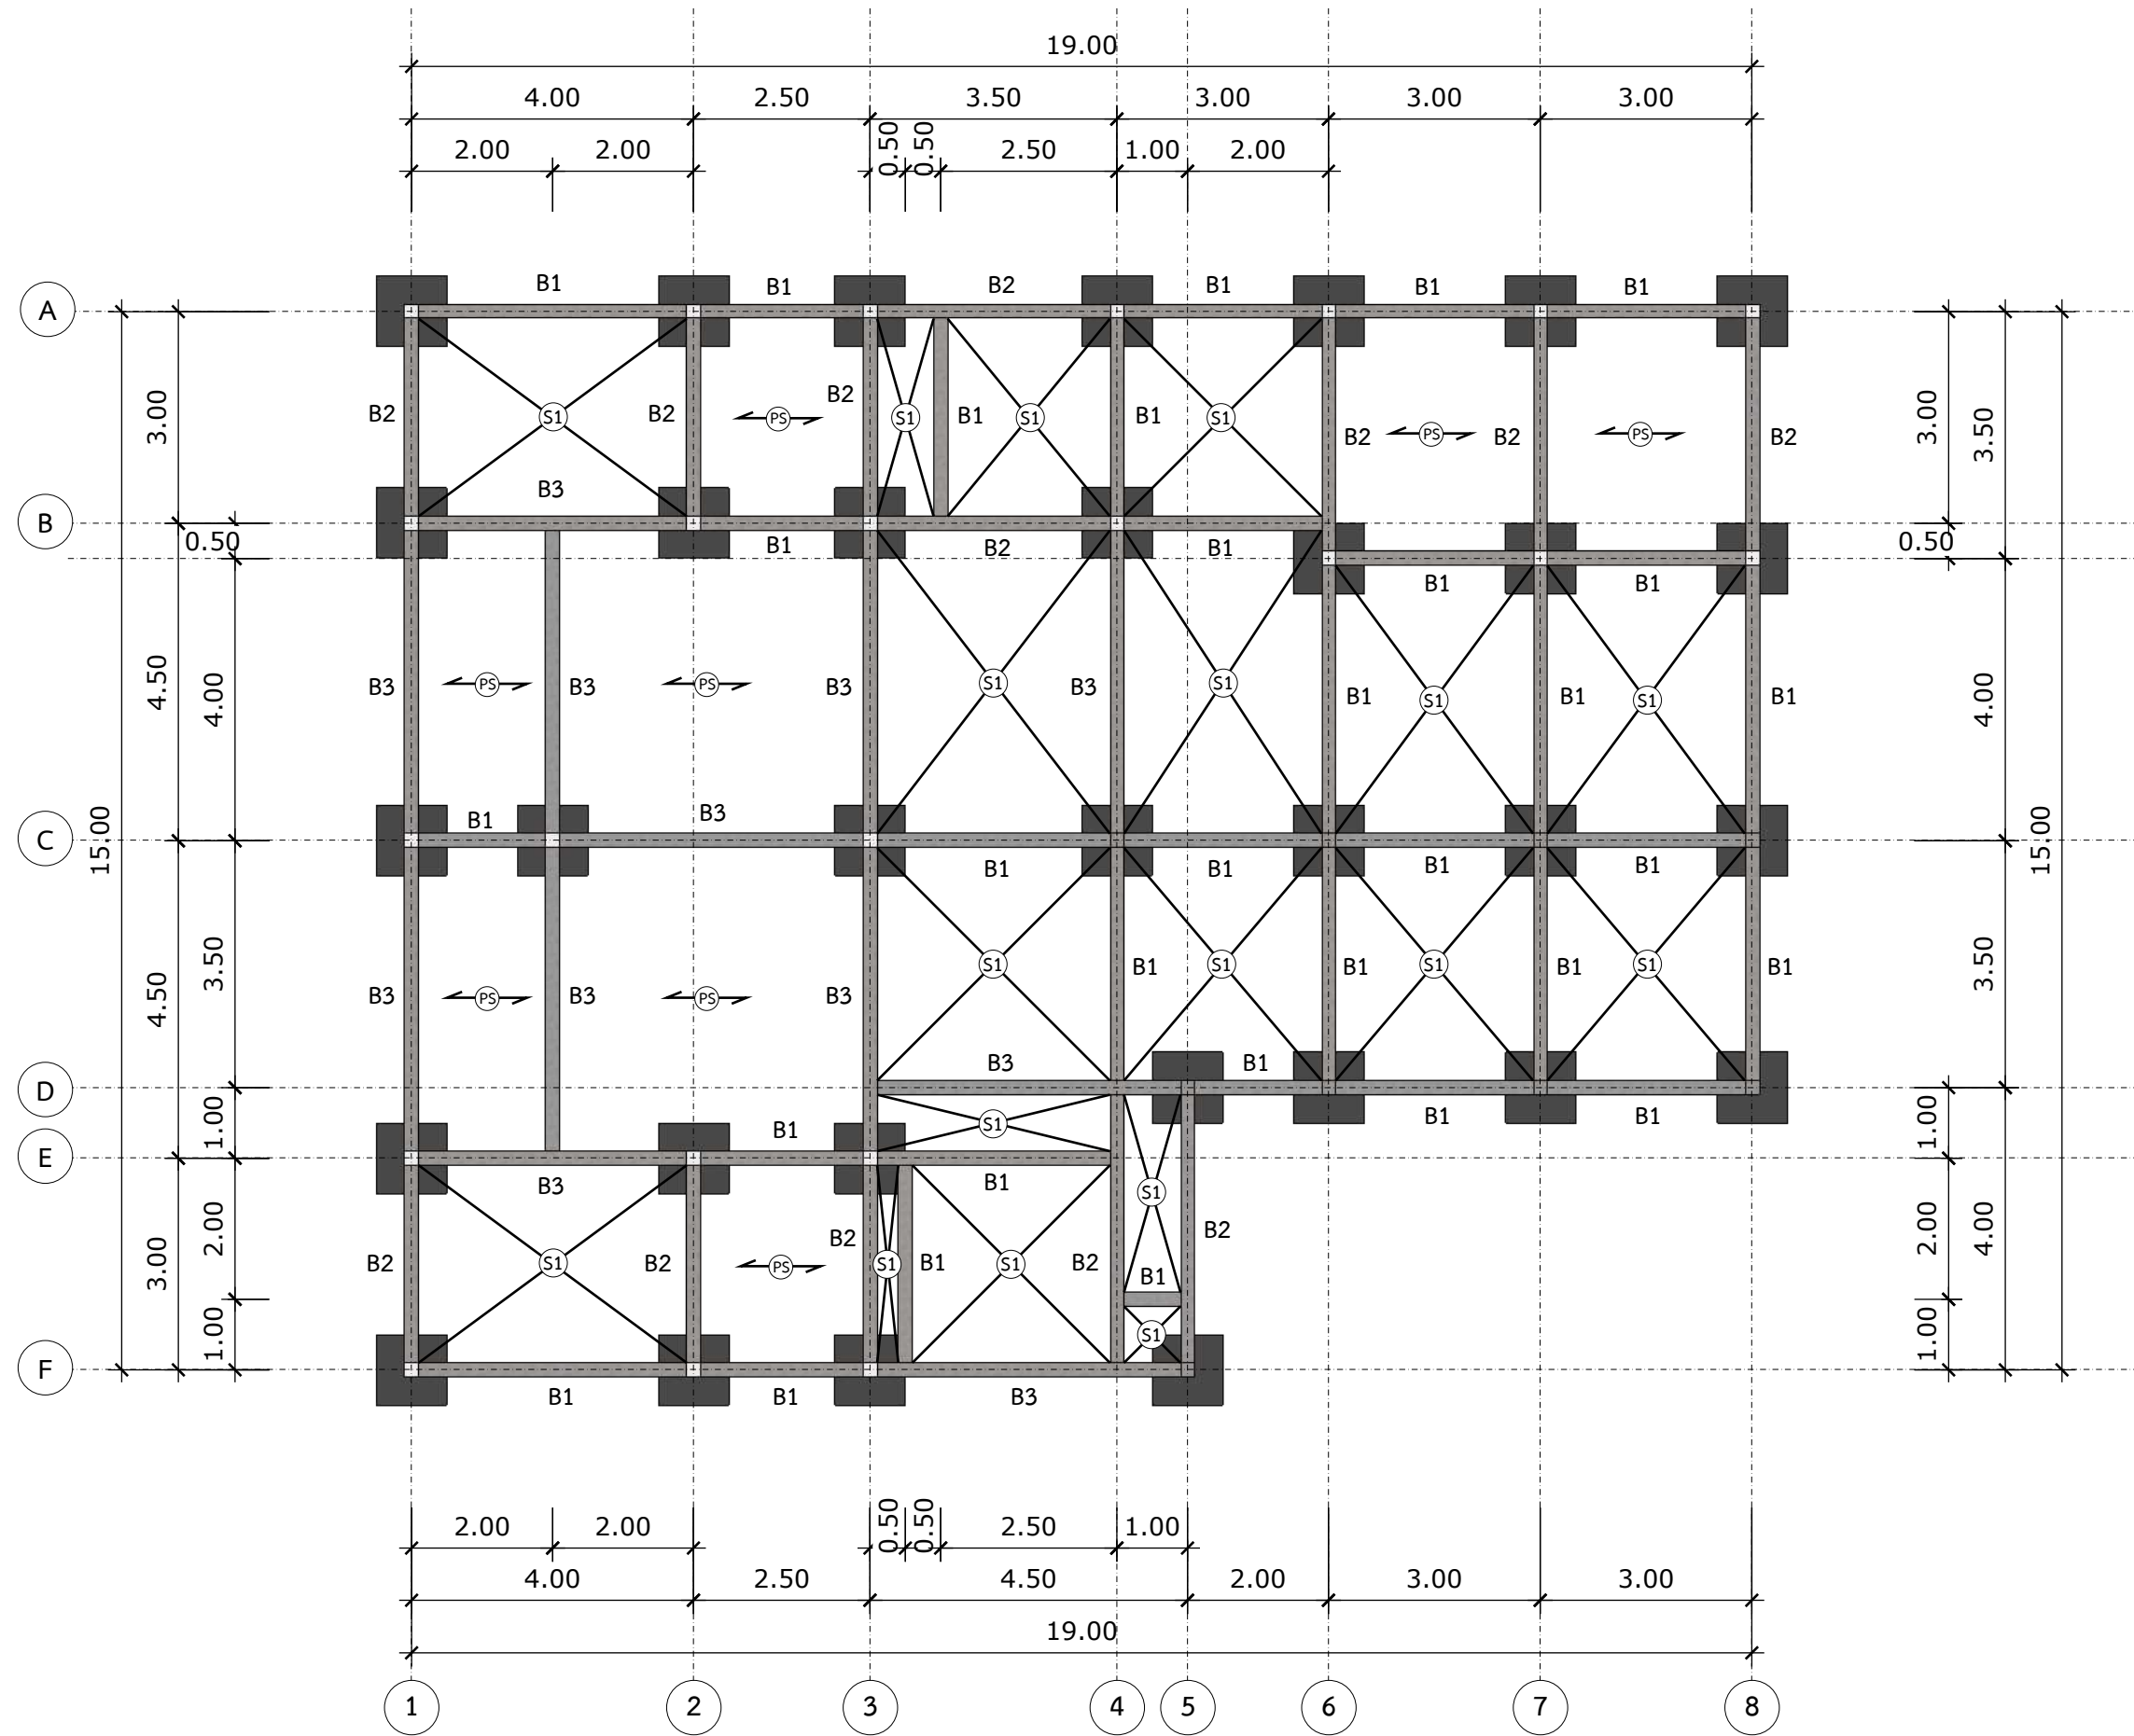

Drawing Title :: แปลนคาน + 0.70 ม.
scale: 1 : 100

A
05

ชื่อโครงการ

โครงการก่อสร้าง
อาคารพักอาศัย
คสล. 1 ชั้น

เจ้าของโครงการ

คุณปรินทร์ เรืองรัตนวณิช

สถาปนิก

นายนิกร สุขแสง
ภสธ.10581
ถ.แจ้งวัฒนะซอย6
แขวงตลาดบางเขน.
เขตหลักสี่. กรุงเทพฯ

วิศวกรโครงสร้าง

นายปฐวี เชื้อชม
ภย.33663

92 ม. 1 ต.ท่าโพธิ์ศรี
อ.เดชอุดม จ.อุบลราชธานี

วิศวกรไฟฟ้า

วิศวกรเครื่องกล

ผู้เขียน

นายปฐวี เชื้อชม
ภย.33663
92 ม. 1 ต.ท่าโพธิ์ศรี
อ.เดชอุดม จ.อุบลราชธานี

ที่ตั้ง

บ้านไม้จ้าว
ตำบล ป่าตอง
อำเภอ กะทู้
จังหวัด ภูเก็ต

แบบแสดง

แปลนคาน + 0.70

FILE NO

DRAWING NO



20

SUB TOTAL

GRAND TOTAL

DATE

--

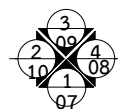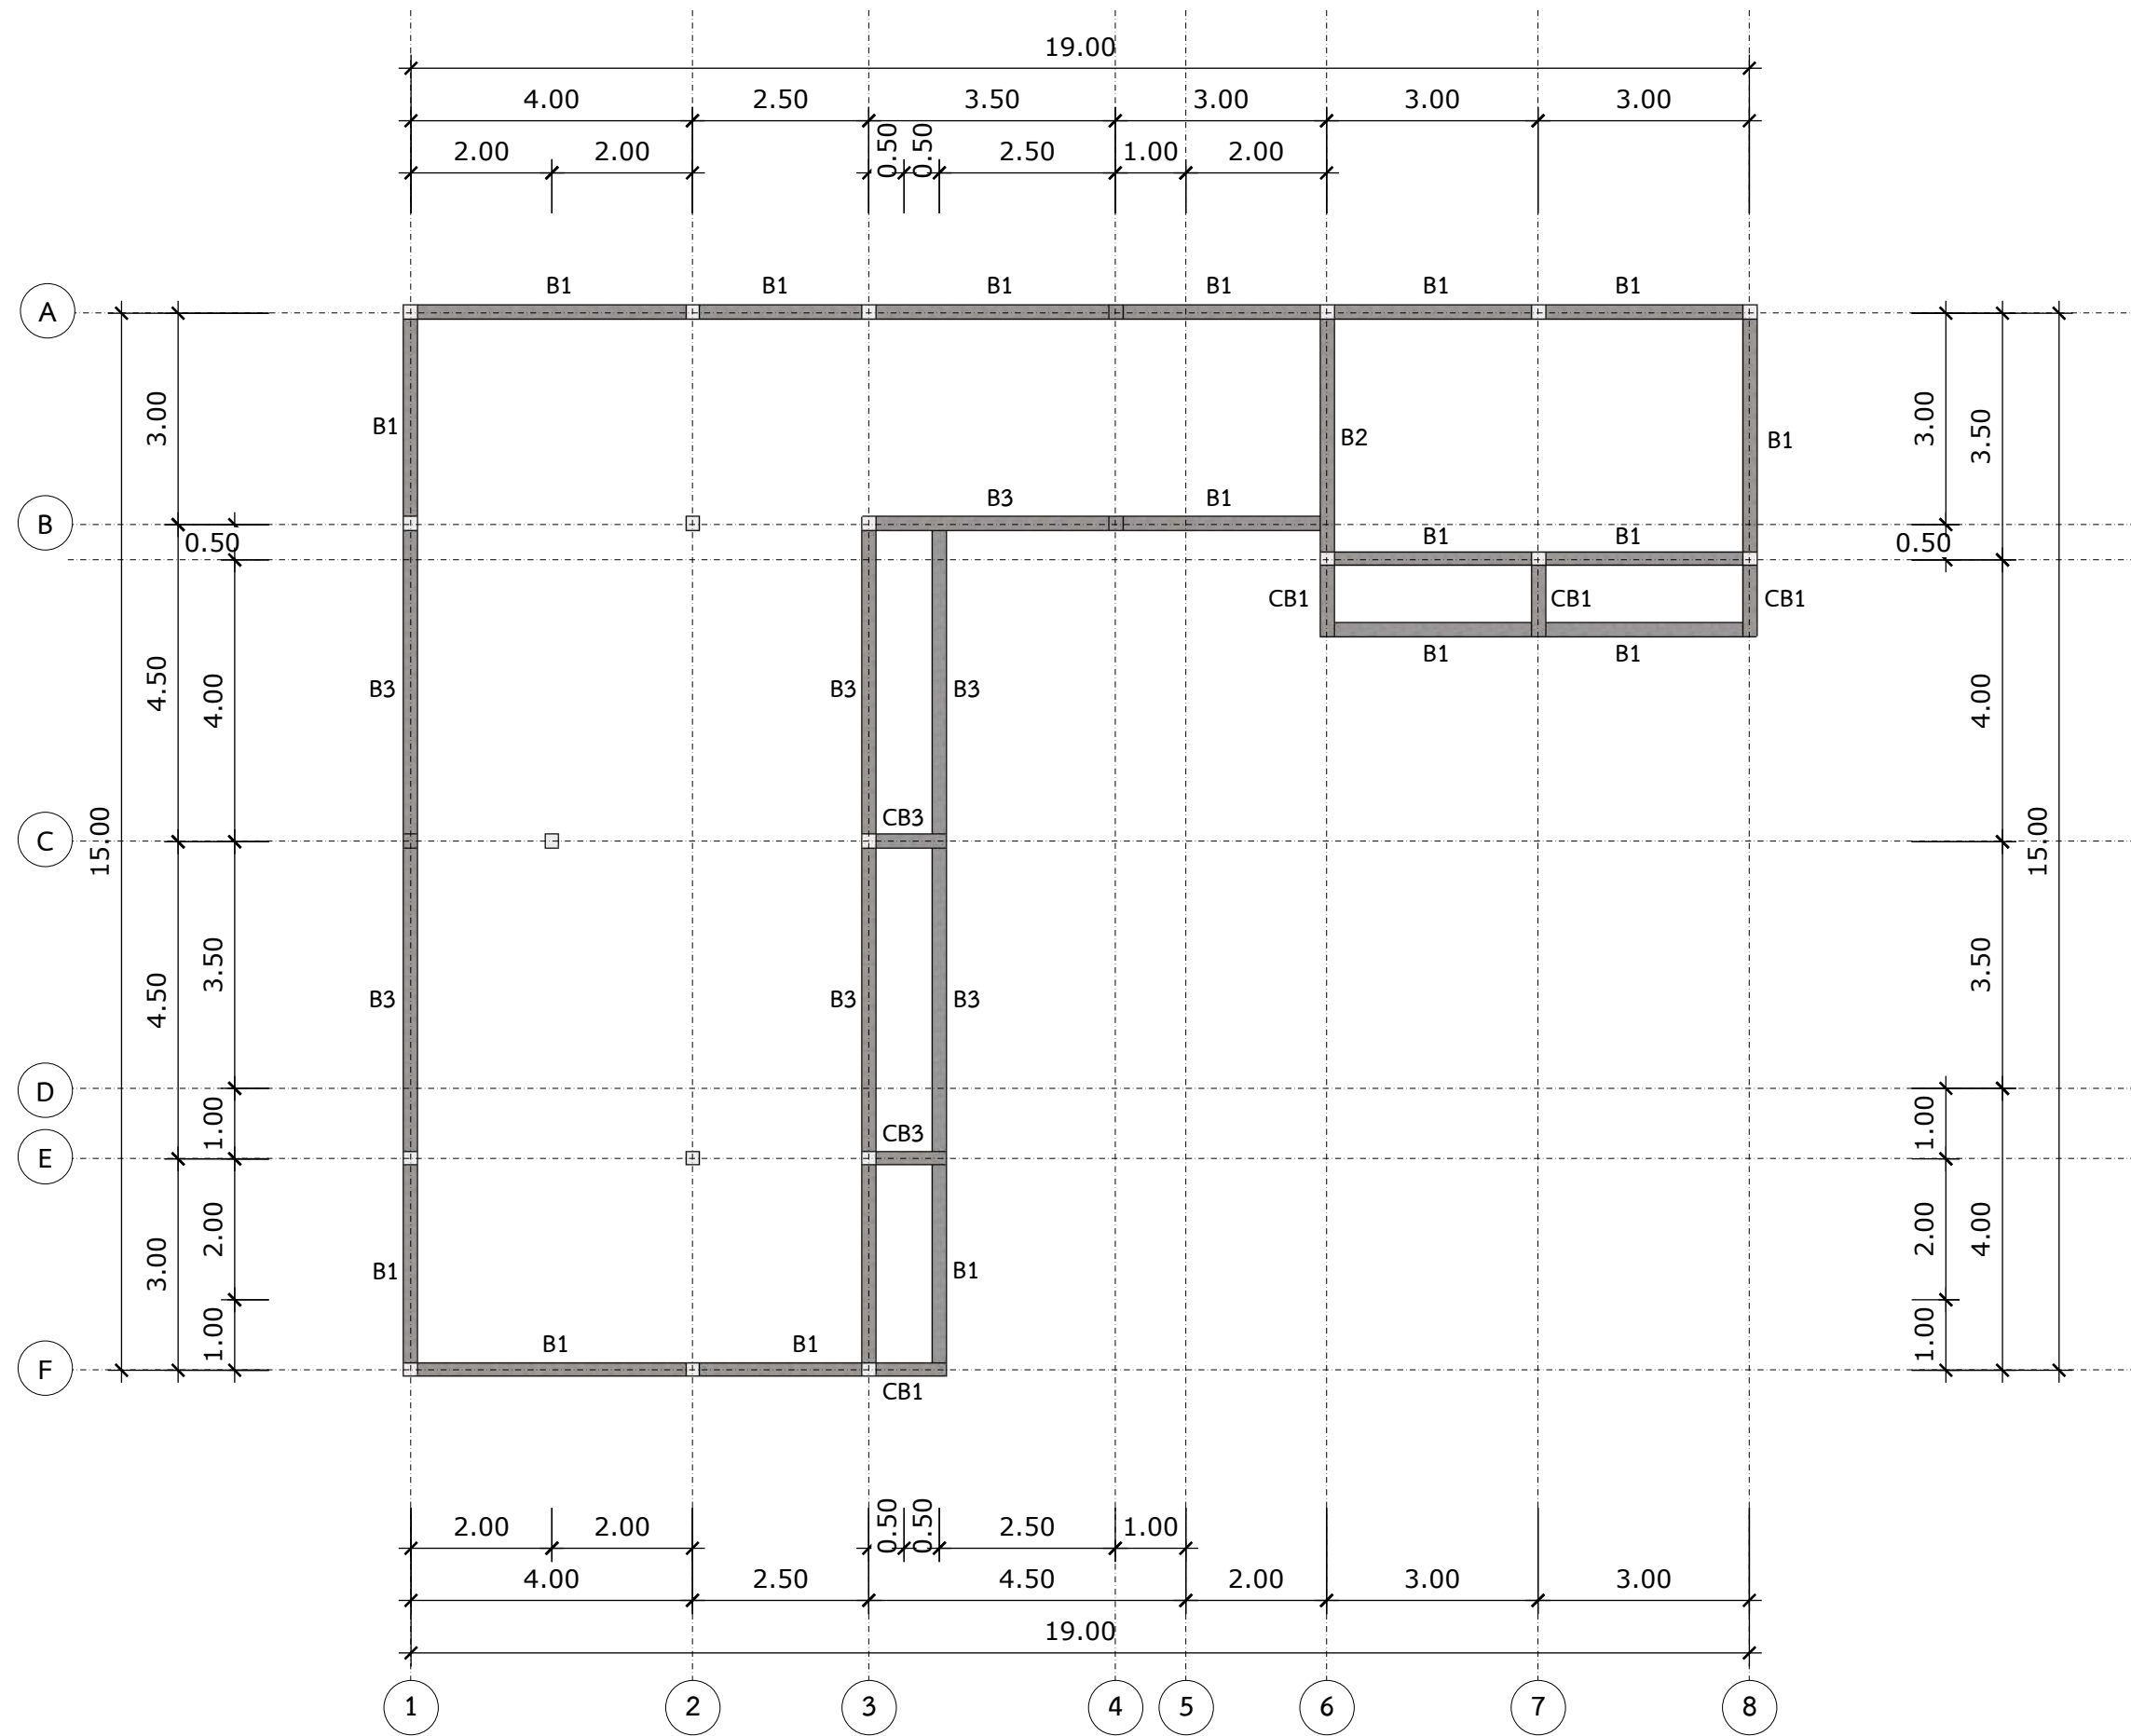

Drawing Title :: แปลนคาน + 4.30 ม.
scale: 1 : 100

A
05

ชื่อโครงการ

โครงการก่อสร้าง
อาคารพักอาศัย
คสล. 1 ชั้น

เจ้าของโครงการ

คุณปรินทร์ เรืองรัตนวานิช

สถาปนิก

.....
นายนิกร สุขแสง
ภสธ.10581
ถ.แจ้งวัฒนะซอย6
แขวงตลาดบางเขน.
เขตหลักสี่. กรุงเทพฯ

วิศวกรโครงสร้าง

.....
นายปฐวี เชื้อชม
ภย.33663
92 ม. 1 ต.ท่าโพธิ์ศรี
อ.เดชอุดม จ.อุบลราชธานี

วิศวกรไฟฟ้า

วิศวกรเครื่องกล

ผู้เขียน

นายปฐวี เชื้อชม
ภย.33663
92 ม. 1 ต.ท่าโพธิ์ศรี
อ.เดชอุดม จ.อุบลราชธานี

ที่ตั้ง

บ้านไม้จ้าว
ตำบล ป่าตอง
อำเภอ กะทู้
จังหวัด ภูเก็ต

แบบแสดง

แปลนคาน + 4.30

FILE NO

SUB TOTAL

DATE


DRAWING NO

21

GRAND TOTAL


--

จันทันเหล็ก C 100x50x20x2.3 mm. @1.00m.
แปเหล็ก C 75x45x15x2.3 mm. @1.00 m.
สะพานรับจันทันเหล็ก 2C 100x50x20x2.3 mm
อะเสเหล็ก 2C 100x50x20x2.3 mm.
หลังคามุงเมทัลชีฟ

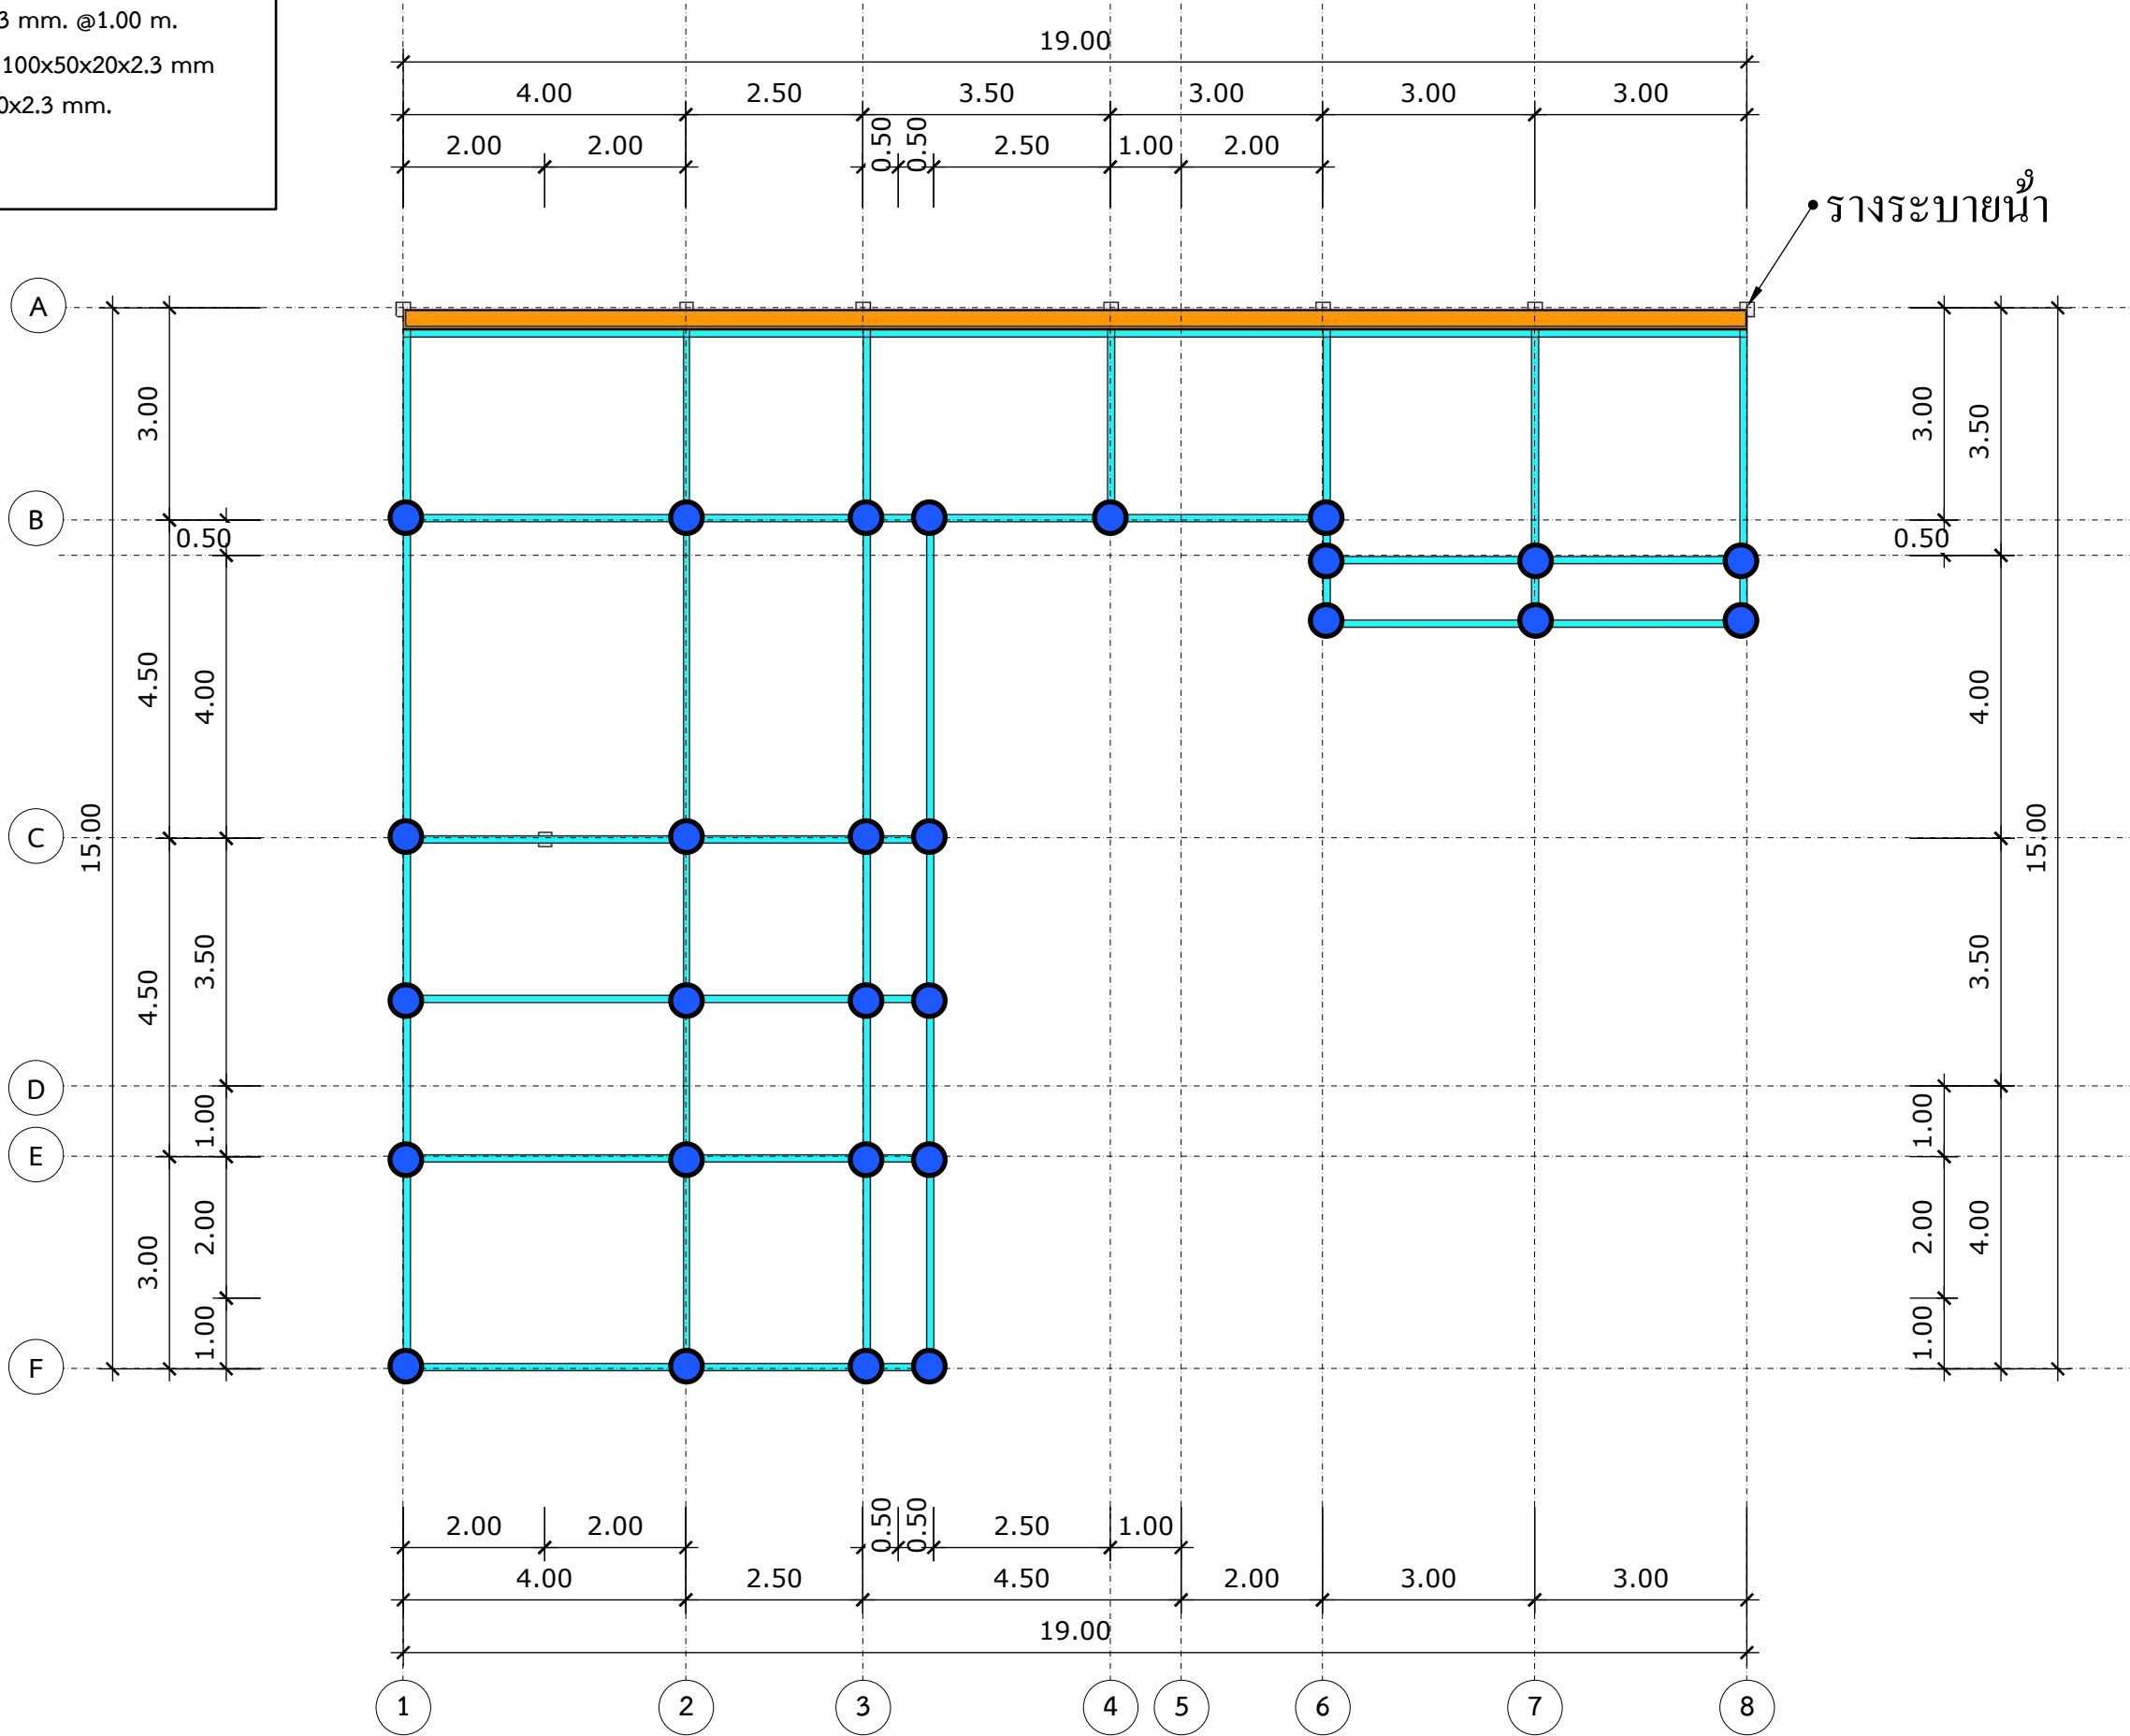

BS1 อะเสเหล็ก 2C 100x50x20x2.3 mm.

ดิ่งเหล็ก 2C 100x50x20x2.3 mm.

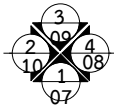

Drawing Title :: แพลน อะเส
scale: 1 : 100

A
05

ชื่อโครงการ

โครงการก่อสร้าง
อาคารพักอาศัย
คสล. 1 ชั้น

เจ้าของโครงการ

คุณปรินทร์ เรืองรัตนวานิช

สถาปนิก

นายนิกร สุขแสง
ภสธ.10581
ถ.แจ้งวัฒนะซอย6
แขวงตลาดบางเขน.
เขตหลักสี่. กรุงเทพฯ

วิศวกรโครงสร้าง

นายปฐวี เชื้อชม
ภย.33663
92 ม. 1 ต.ท่าโพธิ์ศรี
อ.เดชอุดม จ.อุบลราชธานี

วิศวกรไฟฟ้า

วิศวกรเครื่องกล

ผู้เขียน

นายปฐวี เชื้อชม
ภย.33663
92 ม. 1 ต.ท่าโพธิ์ศรี
อ.เดชอุดม จ.อุบลราชธานี

ที่ตั้ง

บ้านไม้จ้าว
ตำบล ป่าตอง
อำเภอ กะทู้
จังหวัด ภูเก็ต

แบบแสดง

แปลนอะเส

FILE NO

DRAWING NO

22


SUB TOTAL

GRAND TOTAL


DATE

--

จันทันเหล็ก C 100x50x20x2.3 mm. @1.00m.
แปเหล็ก C 75x45x15x2.3 mm. @1.00 m.
สะพานรับจันทันเหล็ก 2C 100x50x20x2.3 mm
อะเสเหล็ก 2C 100x50x20x2.3 mm.
หลังคามุงเมทัลชีฟ

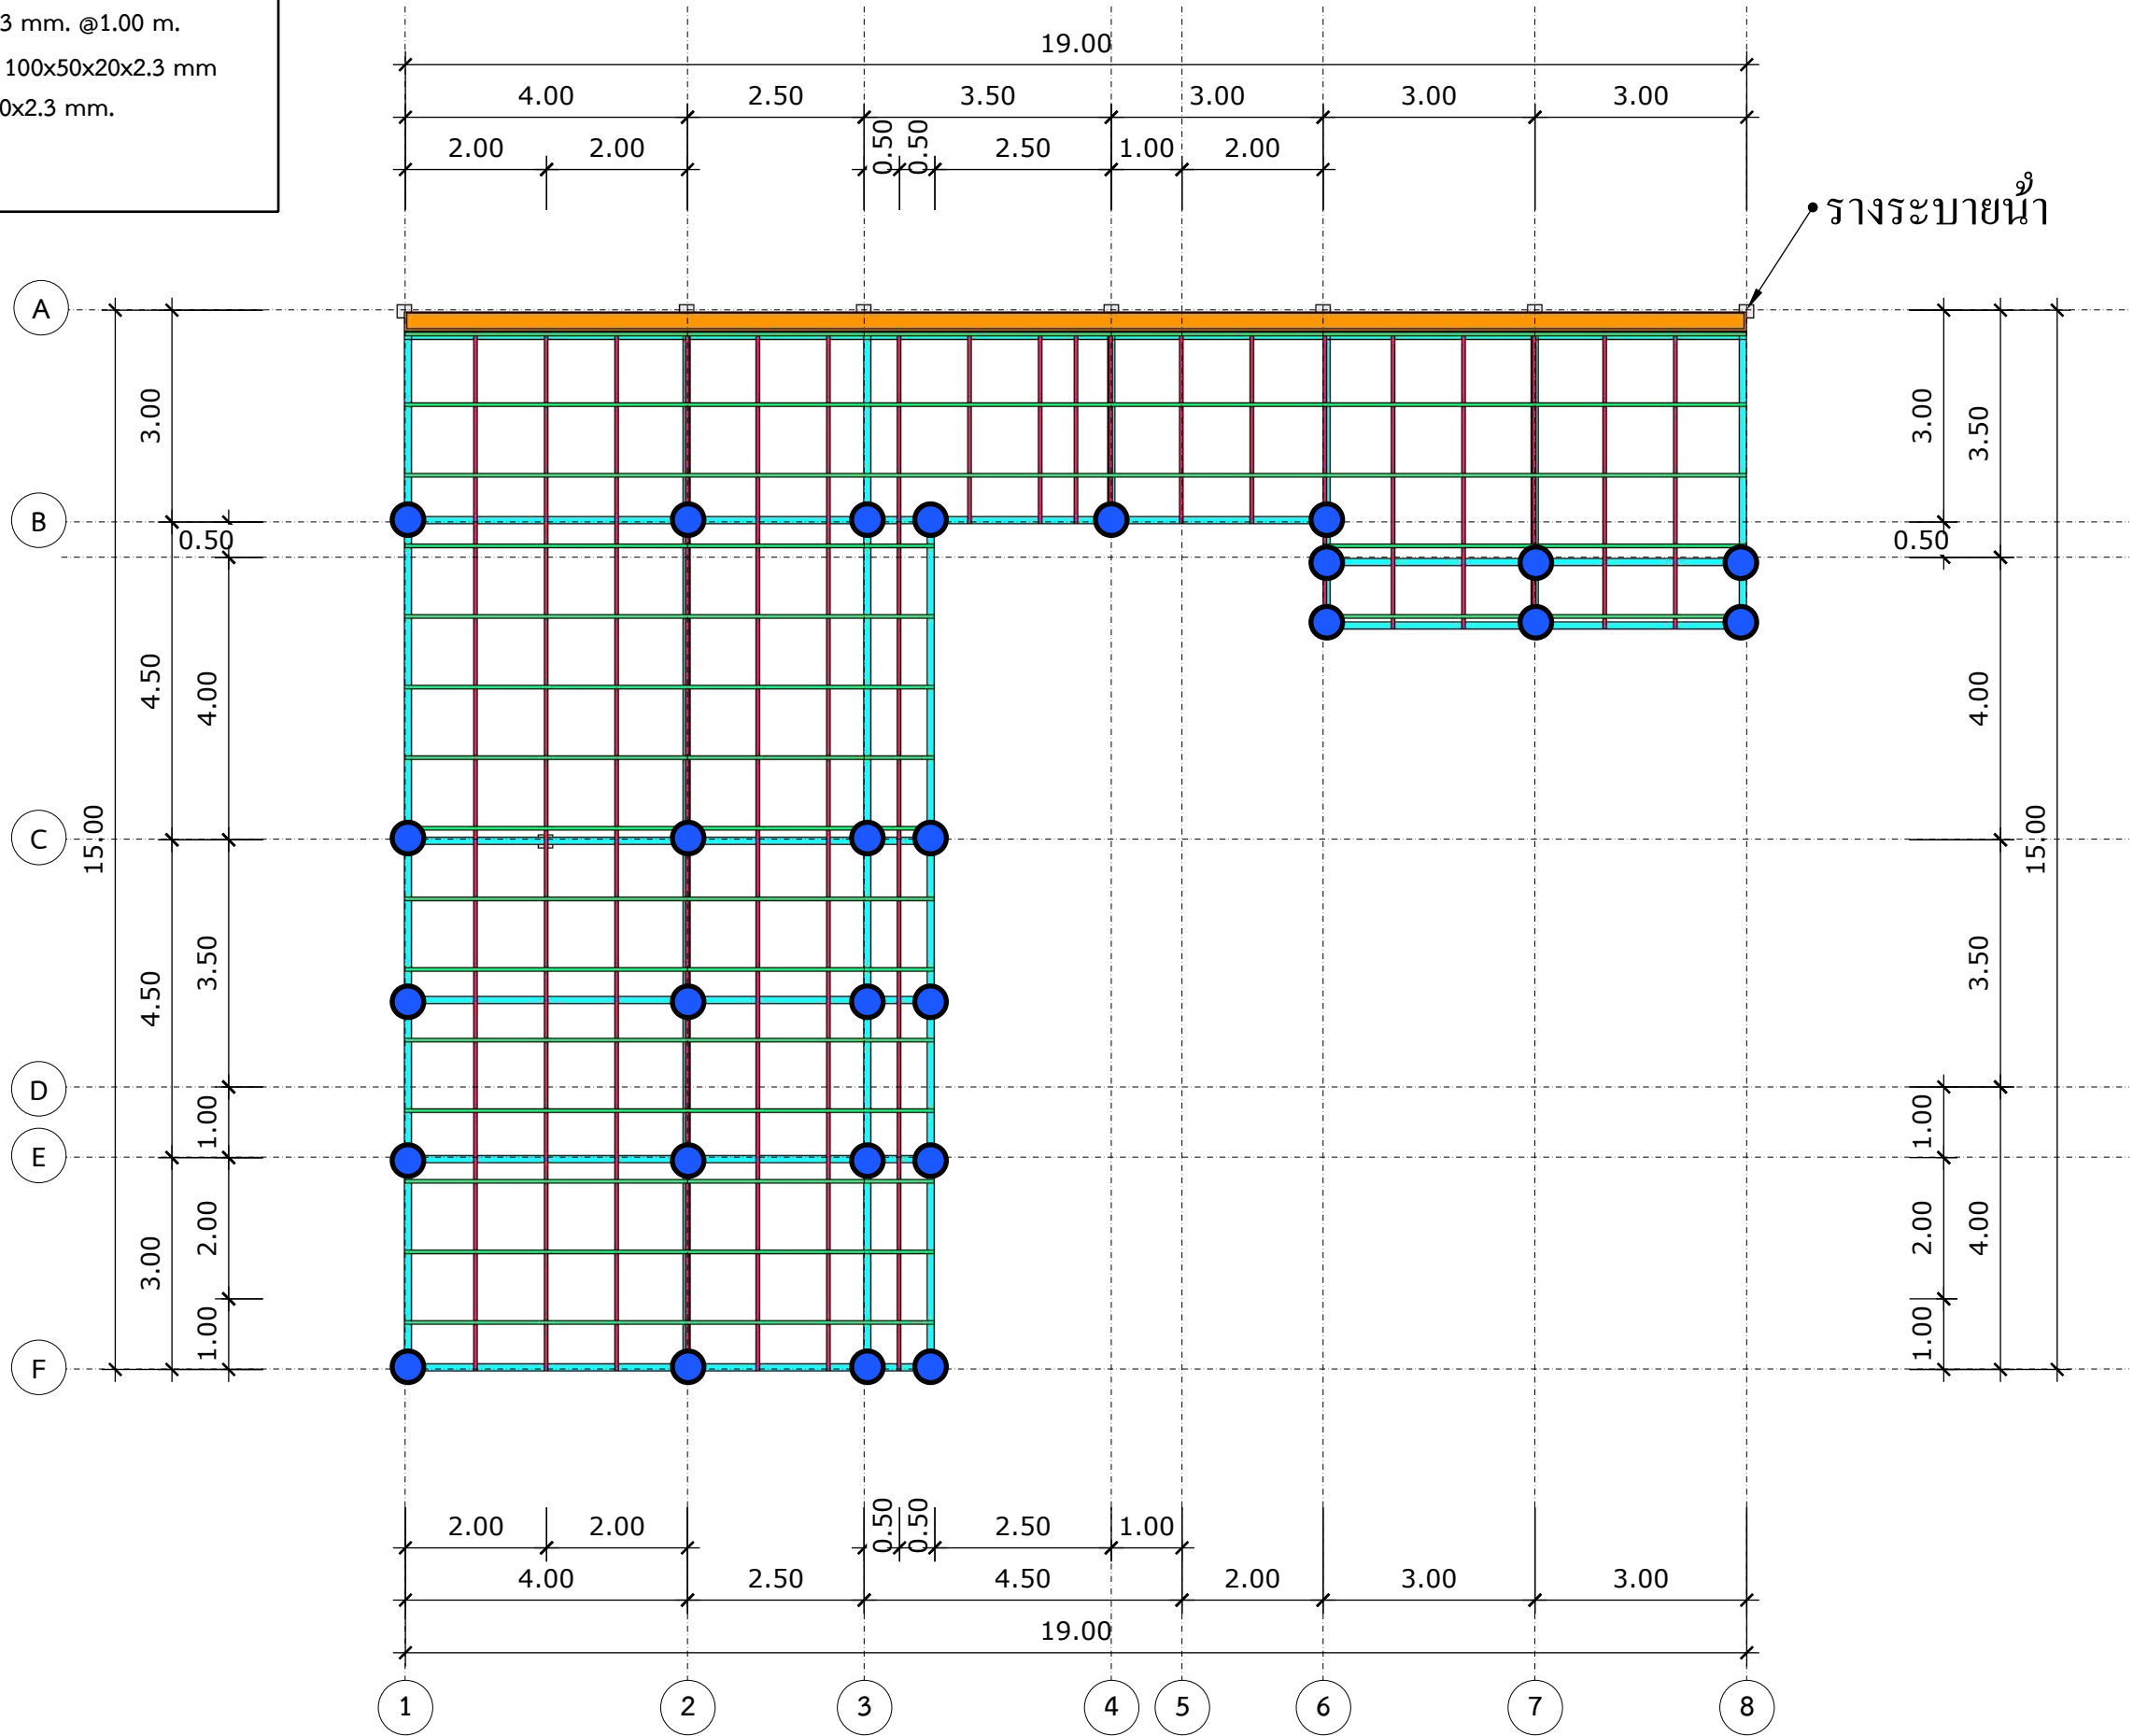

BS1 อะเสเหล็ก 2C 100x50x20x2.3 mm.
ดิ่งเหล็ก 2C 100x50x20x2.3 mm.

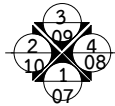

Drawing Title :: แพลนโครงหลังคา จันทัน,แป
scale: 1 : 100

A
05

ชื่อโครงการ

โครงการก่อสร้าง
อาคารพักอาศัย
คสล. 1 ชั้น

เจ้าของโครงการ

คุณปรินทร์ เรืองรัตนวานิช

สถาปนิก

นายนิกร สุขแสง
ภสธ.10581
ถ.แจ้งวัฒนะซอย6
แขวงตลาดบางเขน.
เขตหลักสี่. กรุงเทพฯ

วิศวกรโครงสร้าง

นายปฐวี เชื้อชม
ภย.33663
92 ม. 1 ต.ท่าโพธิ์ศรี
อ.เดชอุดม จ.อุบลราชธานี

วิศวกรไฟฟ้า

วิศวกรเครื่องกล

ผู้เขียน

นายปฐวี เชื้อชม
ภย.33663
92 ม. 1 ต.ท่าโพธิ์ศรี
อ.เดชอุดม จ.อุบลราชธานี

ที่ตั้ง

บ้านไม้จ้าว
ตำบล ป่าตอง
อำเภอ กะทู้
จังหวัด ภูเก็ต

แบบแสดง

แพลนจันทัน+แป

FILE NO

DRAWING NO


23

SUB TOTAL

GRAND TOTAL




DATE

--

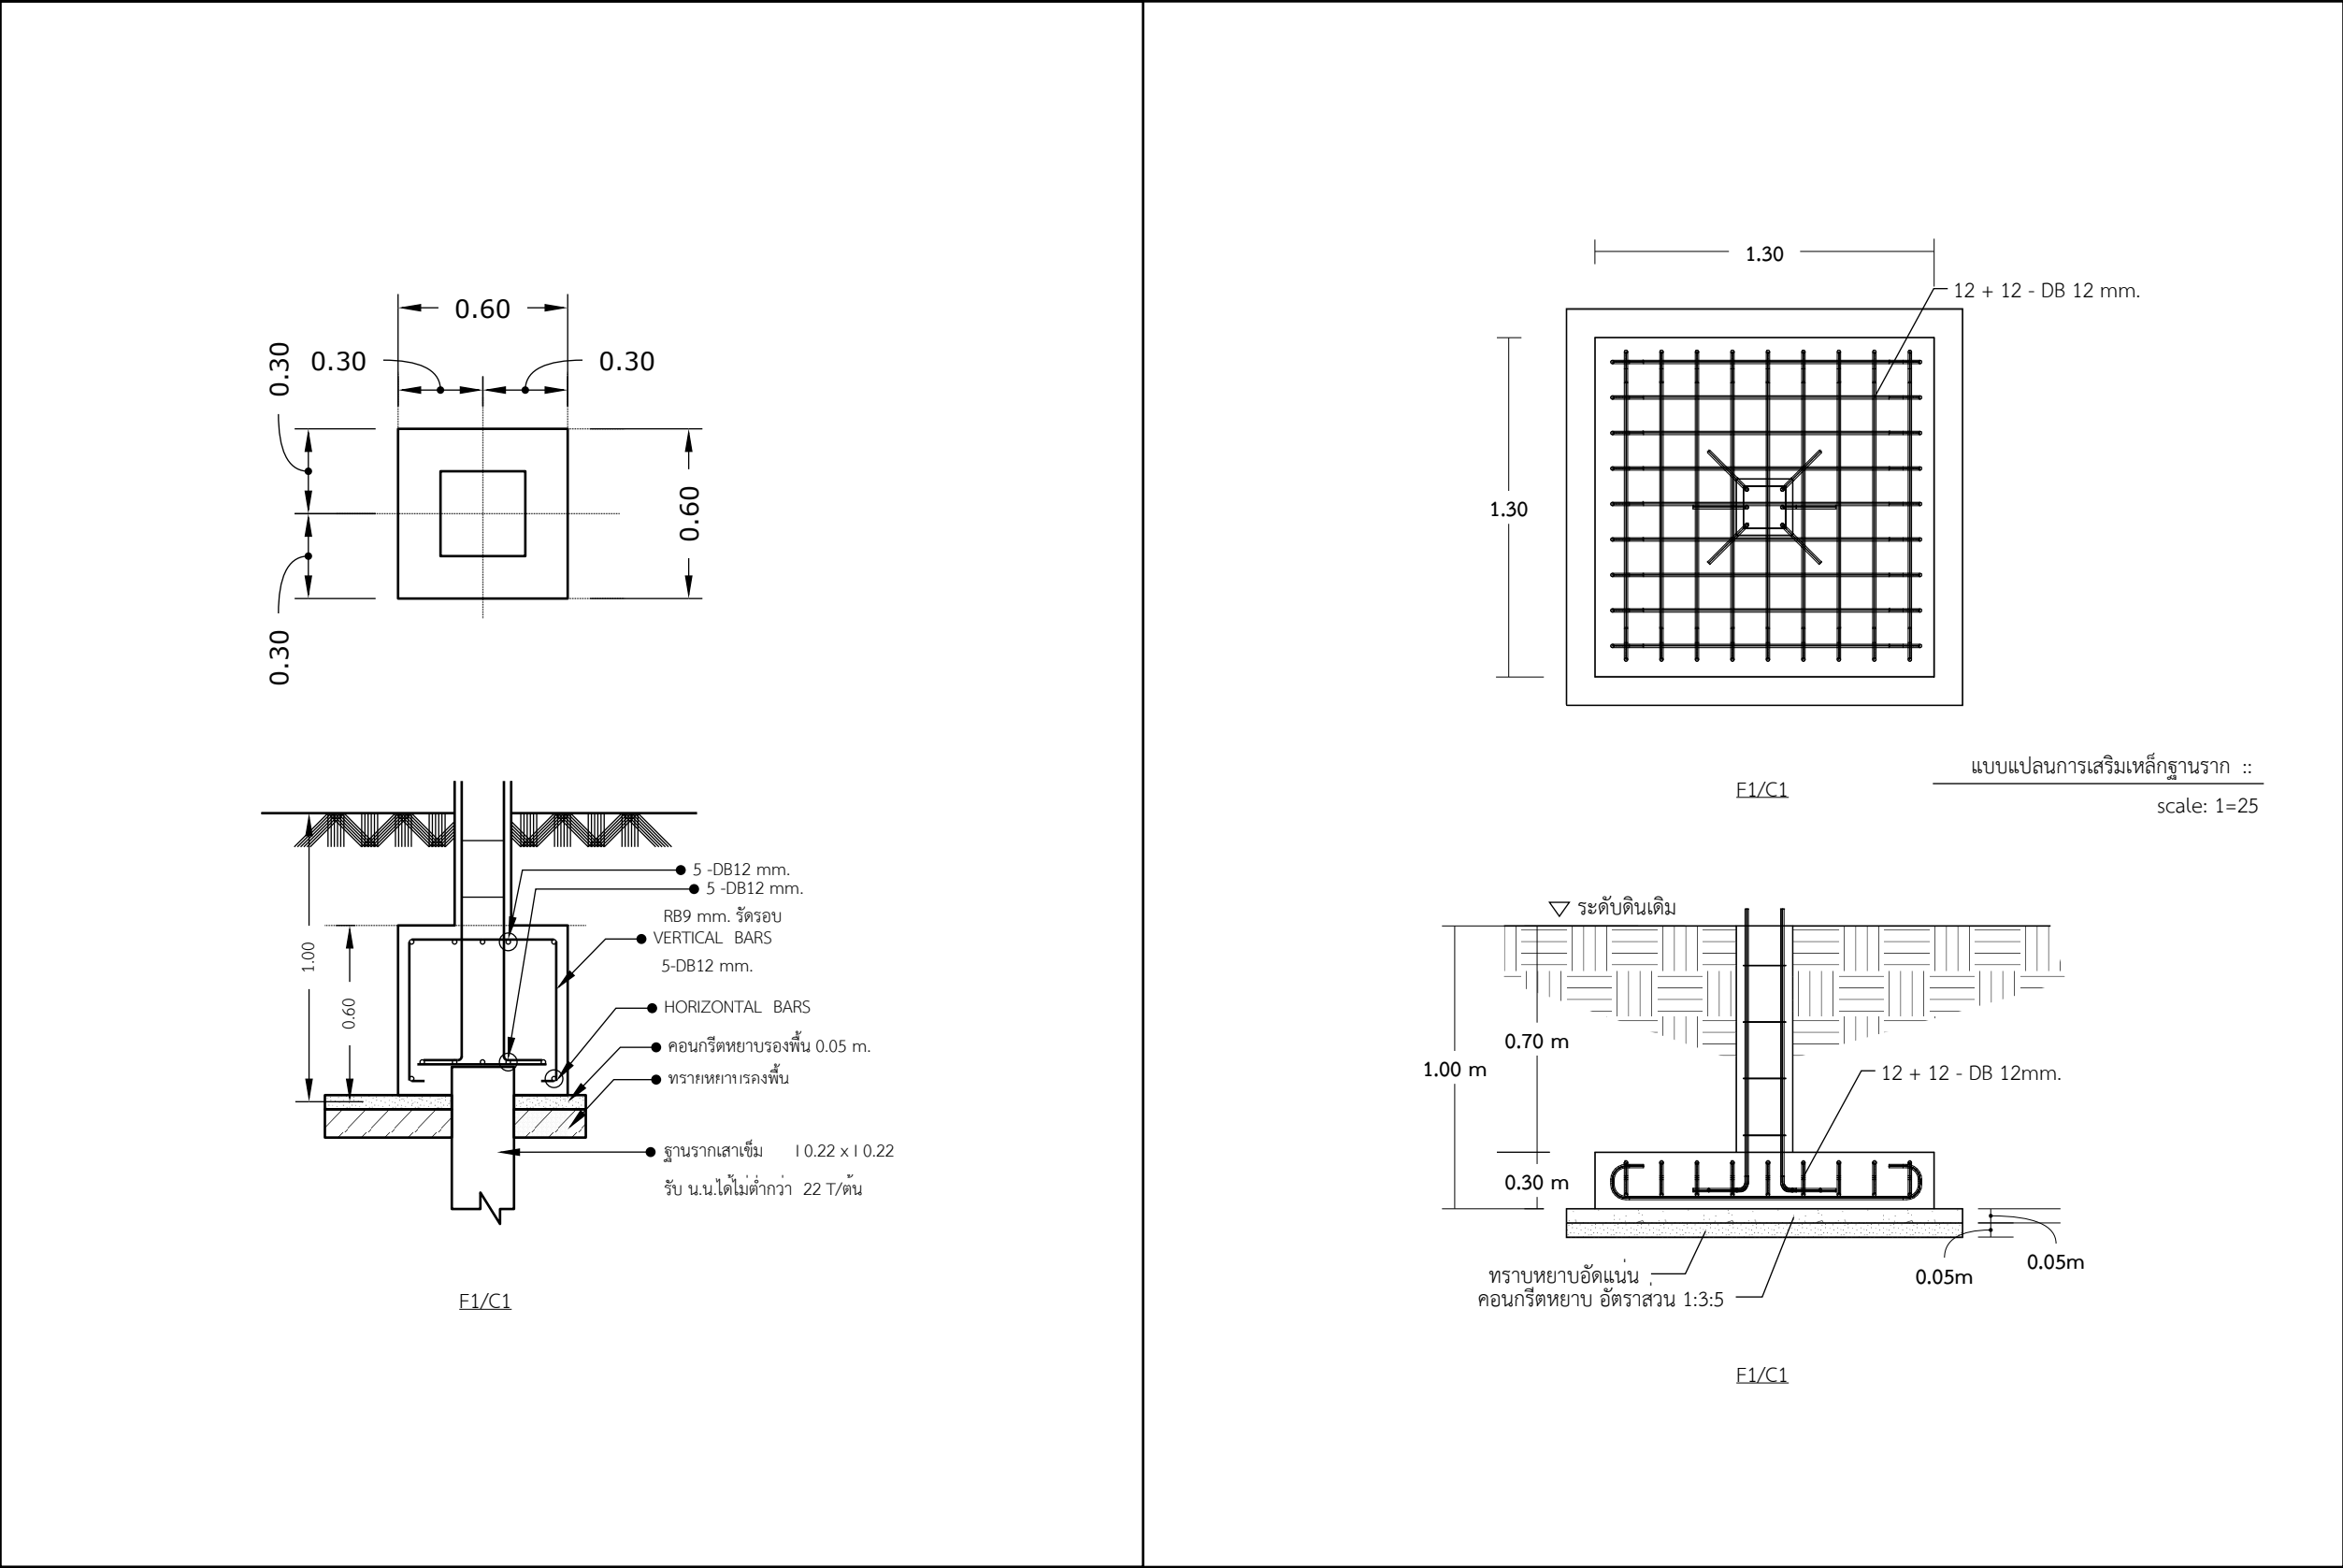

Drawing Title :: Detail Footing
scale: 1 : 50


ชื่อโครงการ โครงการก่อสร้าง อาคารพักอาศัย คสล. 1 ชั้น	
เจ้าของโครงการ คุณปรินทร์ เรืองรัตนวานิช	
สถาปนิก นายนิกร สุขแสง ภสธ.10581 ถ.แจ้งวัฒนะซอย6 แขวงตลาดบางเขน. เขตหลักสี่. กรุงเทพฯ	
วิศวกรโครงสร้าง นายปฐวี เชื้อชม ภย.33663 92 ม. 1 ต.ท่าโพธิ์ศรี อ.เดชอุดม จ.อุบลราชธานี	
วิศวกรไฟฟ้า -	
วิศวกรเครื่องกล -	
ผู้เขียน นายปฐวี เชื้อชม ภย.33663 92 ม. 1 ต.ท่าโพธิ์ศรี อ.เดชอุดม จ.อุบลราชธานี	
ที่ตั้ง บ้านไม้จ้าว ตำบล ป่าตอง อำเภอ กะตุ จังหวัด ภูเก็ต	
แบบแสดง ขยายฐานราก	
FILE NO	DRAWING NO
	24
SUB TOTAL	GRAND TOTAL
DATE	--

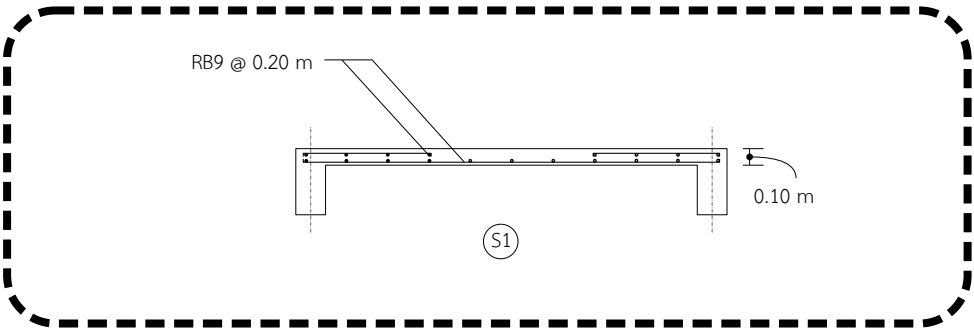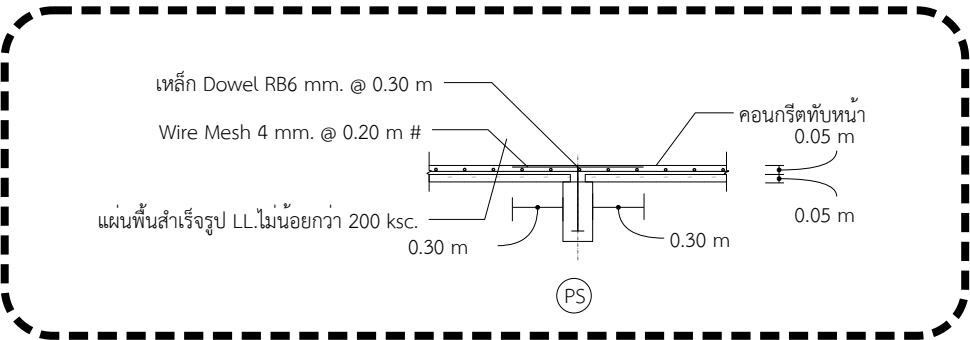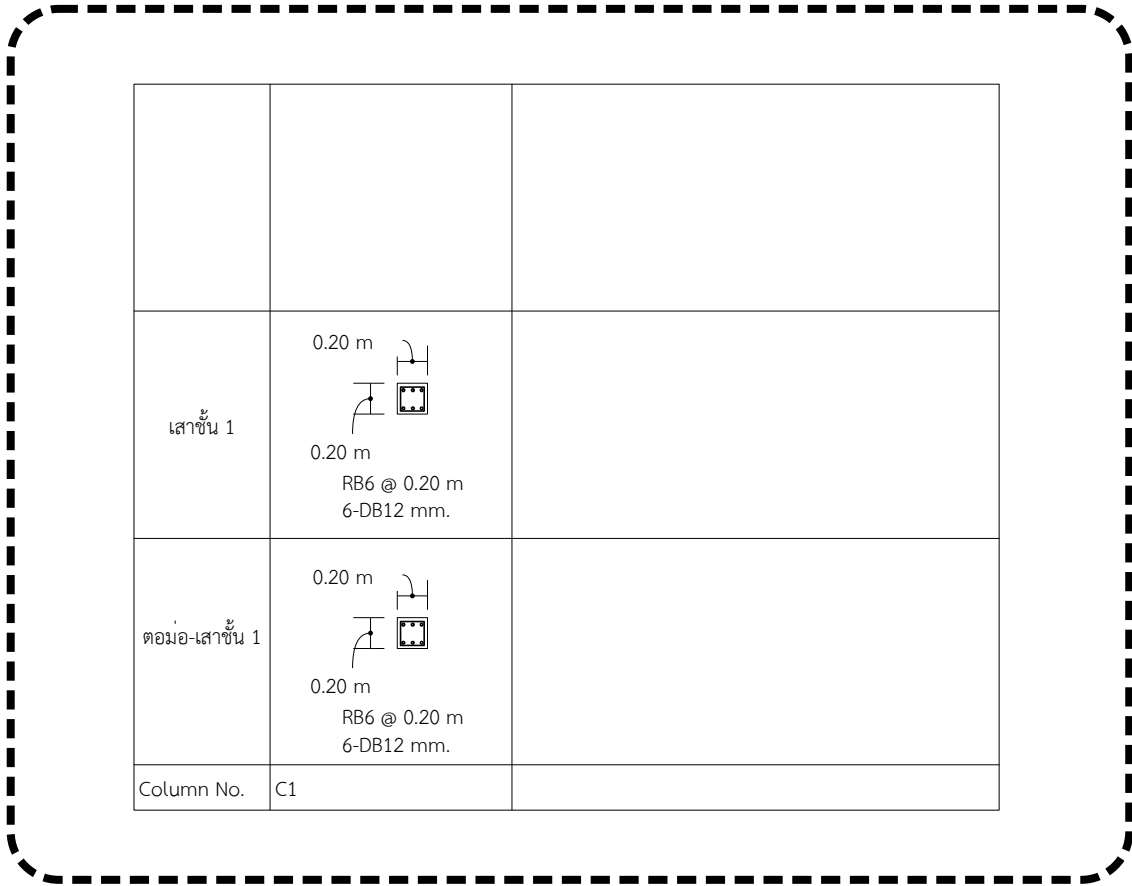

Drawing Title :: Detail Column,Beam,Floor

scale: 1 : 50

S
09

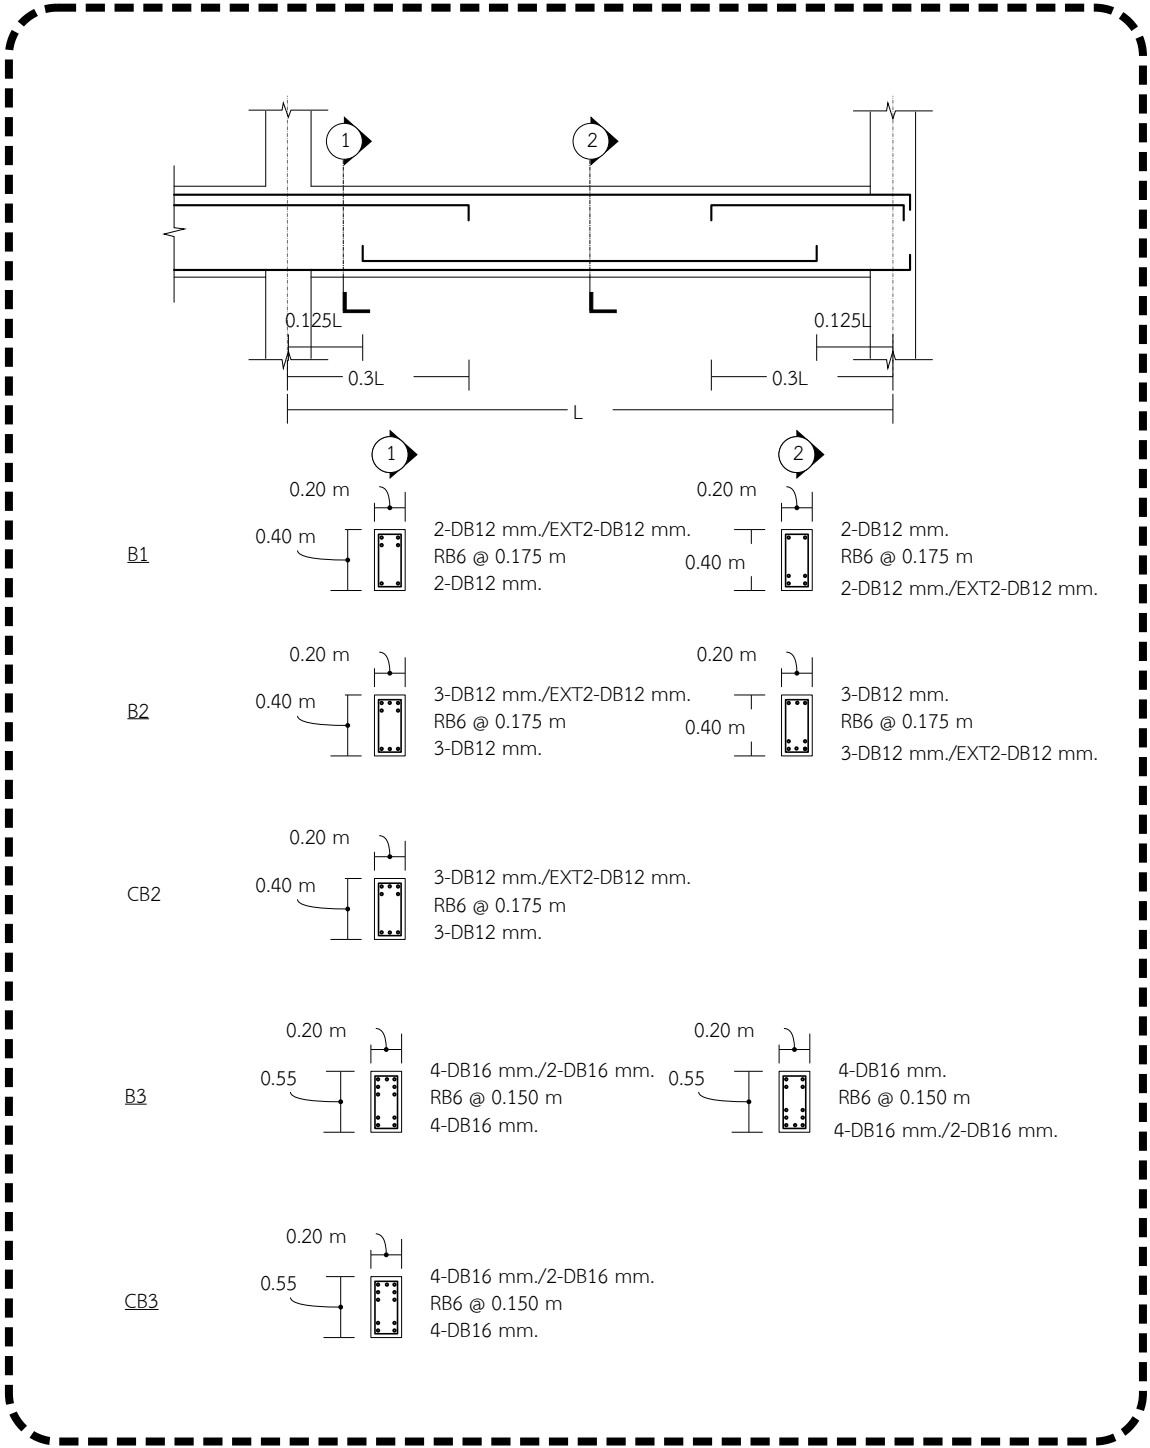

ชื่อโครงการ

โครงการก่อสร้าง
อาคารพักอาศัย
คสล. 1 ชั้น

เจ้าของโครงการ

คุณปรินทร์ เรืองรัตนวานิช

สถาปนิก

นายนิกร สุขแสง
ภสธ.10581
ถ.แจ้งวัฒนะซอย6
แขวงตลาดบางเขน.
เขตหลักสี่. กรุงเทพฯ

วิศวกรโครงสร้าง

นายปฐวี เชื้อชม
ภย.33663

92 ม. 1 ต.ท่าโพธิ์ศรี
อ.เดชอุดม จ.อุบลราชธานี

วิศวกรไฟฟ้า

-

วิศวกรเครื่องกล

-

ผู้เขียน

นายปฐวี เชื้อชม
ภย.33663
92 ม. 1 ต.ท่าโพธิ์ศรี
อ.เดชอุดม จ.อุบลราชธานี

ที่ตั้ง

บ้านไม้จ้าว
ตำบล ป่าตอง
อำเภอ กะทู้
จังหวัด ภูเก็ต

แบบแสดง

ขยายเสา,คาน,พื้น,บันได

FILE NO

DRAWING NO

25



SUB TOTAL

GRAND TOTAL

DATE

--


รายการประกอบแบบ งานระบบไฟฟ้า

  สัญลักษณ์ไฟฟ้า	
แสดงพื้น	รายละเอียด
 MDB	ตู้สวิตช์ปลดวงจร Main Distribution Board ประกอบด้วย
	1. เซฟตี้สวิตช์ (Safety Switch)
	2. สวิตช์บอร์ด (Load Center) พร้อมฝัง Ground Rod
	3. เบรกเกอร์ (Breaker)
	เต้ารับ ชนิดมีกราวด์ฝังผนัง (1 ตัวใน 1 ตลับ)
	เต้ารับคู่ ชนิดมีกราวด์ฝังผนัง (2 ตัวใน 1 ตลับ)
	เต้ารับคู่ ชนิดมีกราวด์ฝังผนัง แบบกันน้ำ (2 ตัวใน 1 ตลับ)
	เต้ารับคู่ ชนิดมีกราวด์ติดบนเฟอร์นิเจอร์ (2 ตัวใน 1 ตลับ)
	เต้ารับคู่ ชนิดมีกราวด์ฝังพื้น (2 ตัวใน 1 ตลับ)
	ตำแหน่งติดตั้งปลั๊กเสาอากาศโทรทัศน์
	ตำแหน่งติดตั้งปลั๊กโทรศัพท์
	ตำแหน่งติดตั้ง Junction Box กรณีเดินสายไฟมาทั้งไว้เพื่อใช้ต่อไฟในภายหลัง
	ตำแหน่งติดตั้งสวิตช์ไฟ เปิด-ปิด ชนิด 1 ทาง (1 สวิตช์/1 ตลับ)
	ตำแหน่งติดตั้งสวิตช์ไฟ เปิด-ปิด ชนิด 1 ทาง (2 สวิตช์/1 ตลับ)
	ตำแหน่งติดตั้งสวิตช์ไฟ เปิด-ปิด ชนิด 2 ทาง
	หลอดไฟ LED
	ตำแหน่งติดตั้งไฟติดผนัง
	ตำแหน่งติดตั้งดวงโคมแบบแขวน
	ตำแหน่งติดตั้งไฟ Downlight ติดฝังฝ้าเพดาน
	ตำแหน่งติดตั้งไฟ Downlight ติดลอย
	ตำแหน่งติดตั้งดวงโคมฟลูออเรสเซนต์ ชนิดทรงกลม ครอบแก้วขาวขุ่น ติดใต้ฝ้าเพดาน
	หลอดฟลูออเรสเซนต์ 18 วัตต์ พร้อมชุดฝาครอบ
	หลอดฟลูออเรสเซนต์ 1x36 วัตต์ พร้อมชุดฝาครอบ
	หลอดฟลูออเรสเซนต์ 2x36 วัตต์ พร้อมชุดฝาครอบ
	ตำแหน่งติดตั้งไฟ Floodlight (ไฟส่องสว่างภายนอก)
	ตำแหน่งติดตั้งไฟ Pendant Luminaries (โคมไฟกึ่ง)
	ตำแหน่งติดตั้งโคมไฟห้อยจากเพดาน,ไฟระย้า

สัญลักษณ์ไฟฟ้า	
แสดงพื้น	รายละเอียด
	ตำแหน่งติดตั้งโคมไฟแสงสว่างฉุกเฉิน Emergency Light
	เครื่องปรับอากาศ
	เครื่องทำน้ำอุ่น
	ช่องจ่ายแอร์ใต้ฝ้า
	พัดลมดูดอากาศชนิดฝังฝ้า
	Manual Station
	Heat Detector
	Smoke Detector
	สัญญาณแจ้งเหตุเพลิงไหม้ Fire Alarm
	ถังดับเพลิง Fire Extinguisher
	ป้ายบอกทางหนีไฟ
-----	แนวทางเดินสายไฟฟ้า (สายไฟนอกชายคา ใหลุมด้วย ท่อร้อยสายไฟ)
-----	สายไฟฟ้า ตามมาตรฐานกำหนดการไฟฟ้า ร้อยในท่อ PVC. เดินฝังในผนังหรือเหนือฝ้าเพดาน
	แอร์คอมเพรสเซอร์ (Air Compressor)

มาตรฐานการปฏิบัติงาน

- การเดินสายจะต้องปฏิบัติตามมาตรฐานของการไฟฟ้าส่วนภูมิภาคโดยเคร่งครัด
- การตัดต่อสายทำได้เฉพาะกล่องต่อสาย ดวงโคม สวิตช์ และเต้าเสียบ
- กล่องต่อสาย(บล็อกไฟ)ต้องใช้ทุกแห่งที่มีสวิตช์ เต้าเสียบ และจุดต่อสายแยกไปยังดวงโคมและอุปกรณ์ไฟฟ้า
- การต่อสายขนาดเล็กให้ใช้ INSULATED SOLDERLESS WIRE CONNECTOR UL-APPROVED ชนิดเกลียวชั้นหรือชนิดที่ใช้เครื่องกลบีบ ขนาดให้ถือตามมาตรฐานของผู้ผลิต
- การต่อสายขนาดใหญ่ให้ใช้ SOLDERLESS WIRE CONNEC UL-APPROVED ชนิดให้ใช้เครื่องมือกลบีบ แล้วพันด้วยเทปพันสายอย่างน้อย 3 ชั้น เมื่อพันแล้วต้องหนาไม่น้อยกว่าฉนวนหุ้มสายไฟ
- การเดินท่อ EMT, IMT จะต้องขนาน หรือตั้งฉากกับพื้น ผนังและโครงสร้าง
- การติดตั้งวัสดุอุปกรณ์ไฟฟ้าต่างๆ ให้เป็นไปตามมาตรฐานการก่อสร้างและคำนึงถึงความปลอดภัยของผู้ใช้งานเป็นหลัก

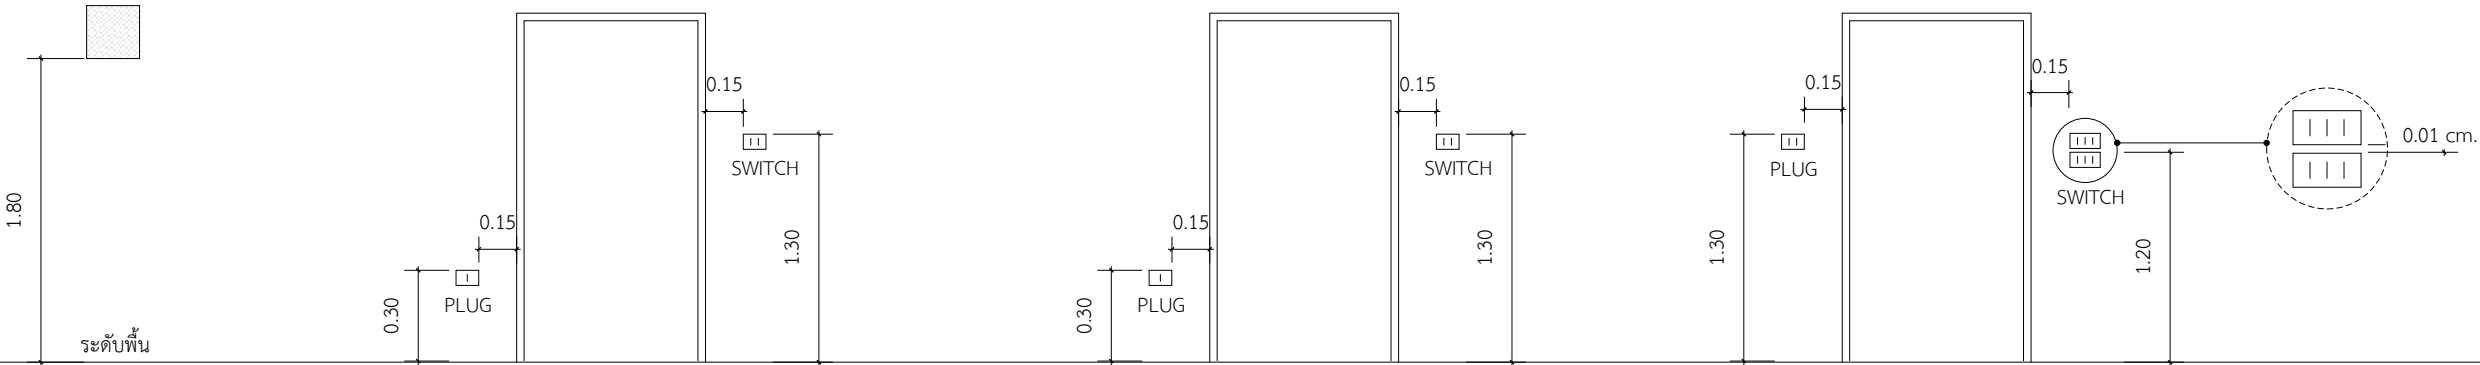

ตำแหน่งสวิตช์บอร์ด

ตำแหน่งสวิตช์และปลั๊กทั่วไป

ตำแหน่งสวิตช์และปลั๊ก ในห้องครัว,ห้องน้ำ,ห้องซักผ้า

หมายเหตุ หากมีการเปลี่ยนแปลง รายละเอียดทางการก่อสร้าง ให้เป็นไปตามมาตรฐานการก่อสร้าง และ คำนึงถึงความปลอดภัยของผู้ใช้งานเป็นหลัก

ชื่อโครงการ

โครงการก่อสร้าง
อาคารพักอาศัย
คสล. 1 ชั้น

เจ้าของโครงการ

คุณปรินทร์ เรืองรัตนวานิช

สถาปนิก

.....
นายนิกร สุขแสง
ภสธ.10581
.....
ถ.แจ้งวัฒนะซอย6
แขวงตลาดบางเขน.
เขตหลักสี่. กรุงเทพฯ

วิศวกรโครงสร้าง

.....
นายปฐวี เชื้อชม
ภย.33663

92 ม. 1 ต.ท่าโพธิ์ศรี
อ.เดชอุดม จ.อุบลราชธานี

วิศวกรไฟฟ้า

วิศวกรเครื่องกล

ผู้เขียน

นายปฐวี เชื้อชม
ภย.33663
92 ม. 1 ต.ท่าโพธิ์ศรี
อ.เดชอุดม จ.อุบลราชธานี

ที่ตั้ง

บ้านไม้จ้าว
ตำบล ป่าตอง
อำเภอ กะตุ
จังหวัด ภูเก็ต

แบบแสดง

รายการประกอบแบบไฟฟ้า

FILE NO

DRAWING NO



26

SUB TOTAL


GRAND TOTAL

DATE

--

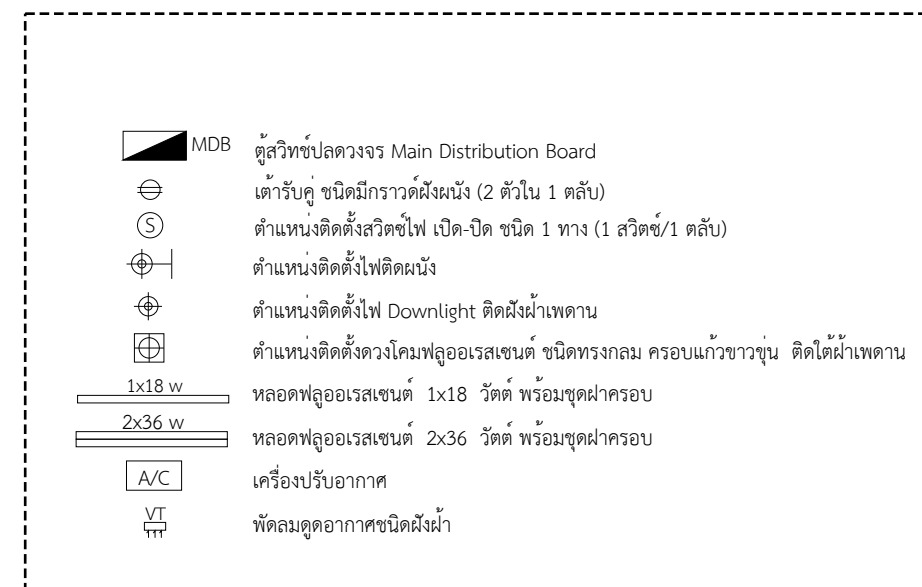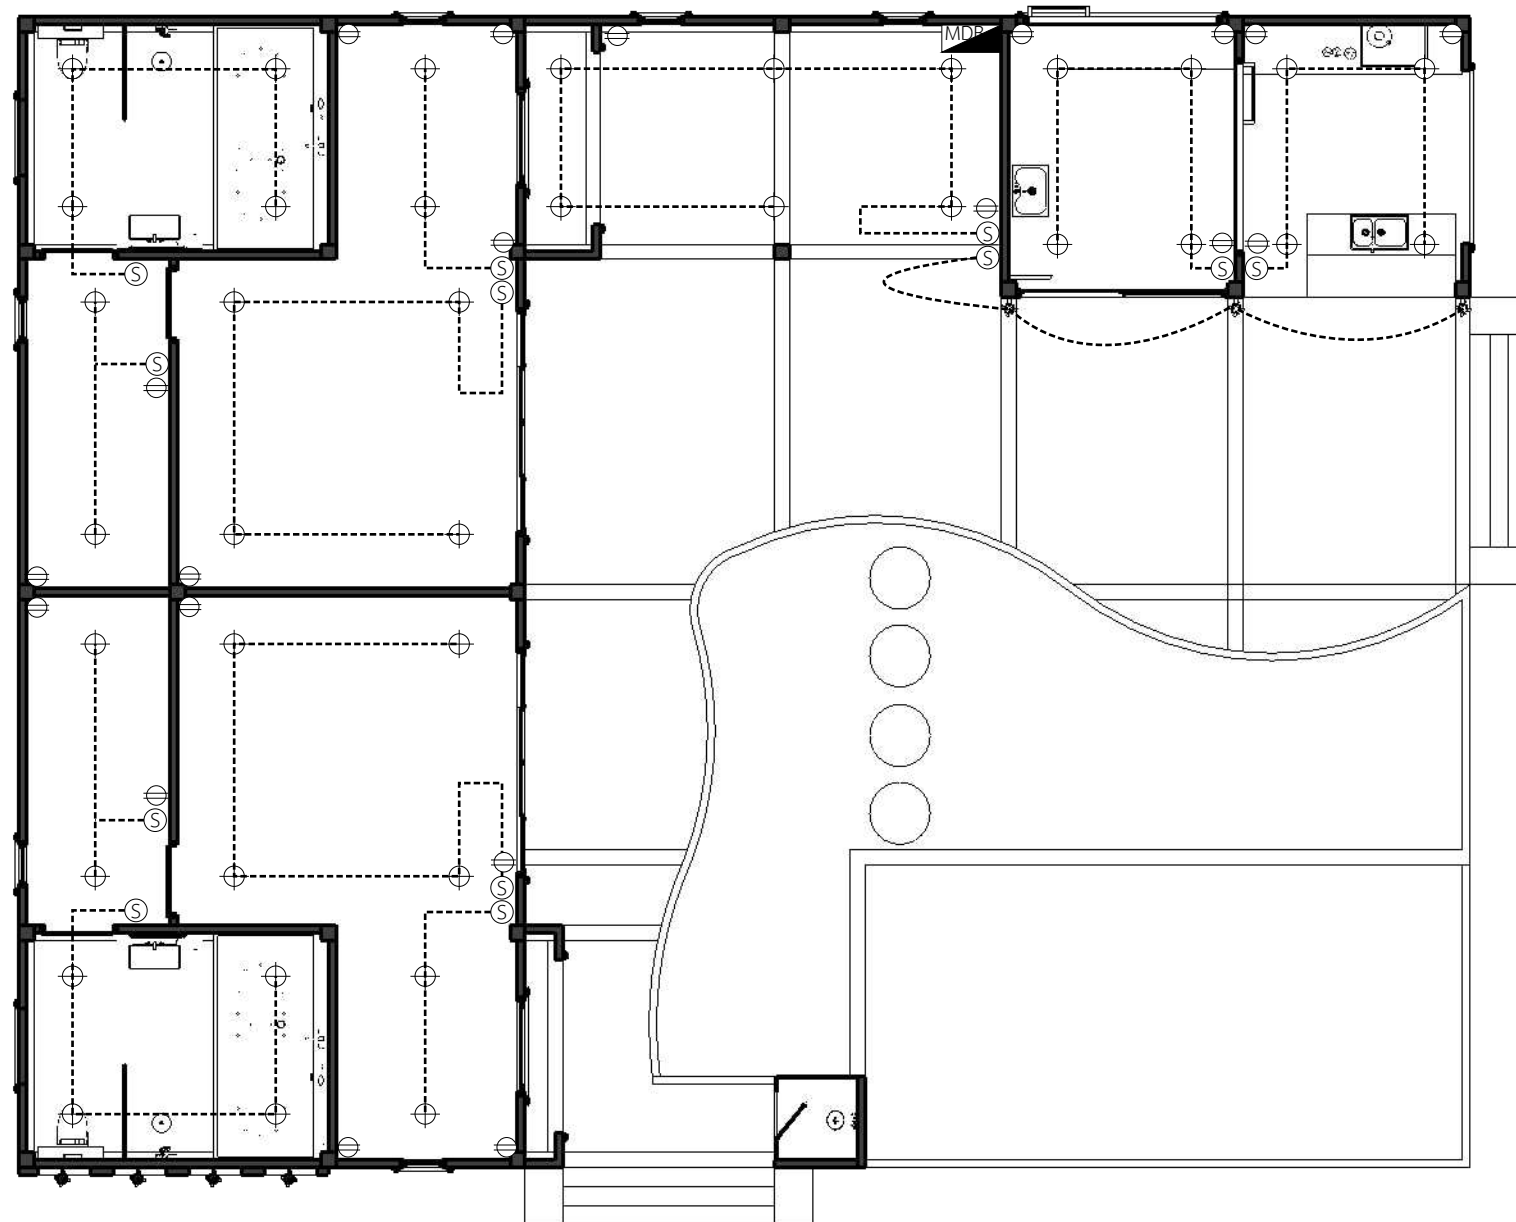

CH.THANAKRIT DESIGN
081-387-9527
ID LINE : jp_pt_









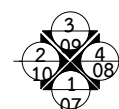



Drawing Title :: 1st Floor Electrical
scale: 1 : 100

E
01



ชื่อโครงการ	
โครงการก่อสร้าง อาคารพักอาศัย คสล. 1 ชั้น	
เจ้าของโครงการ	
คุณปรินทร์ เรืองรัตนวานิช	
สถาปนิก	
นายนิกร สุขแสวง ภสธ.10581 ถ.แจ้งวัฒนะซอย6 แขวงตลาดบางเขน. เขตหลักสี่. กรุงเทพฯ	
วิศวกรโครงสร้าง	
นายปฐวี เชื้อชม ภย.33663 92 ม. 1 ต.ท่าโพธิ์ศรี อ.เดชอุดม จ.อุบลราชธานี	
วิศวกรไฟฟ้า	
-	
วิศวกรเครื่องกล	
-	
ผู้เขียน	
นายปฐวี เชื้อชม ภย.33663 92 ม. 1 ต.ท่าโพธิ์ศรี อ.เดชอุดม จ.อุบลราชธานี	
ที่ตั้ง	
บ้านไม้จ้าว ตำบล ป่าตอง อำเภอ กะทู้ จังหวัดภูเก็ต	
แบบแสดง	
แปลนไฟฟ้า	
FILE NO	DRAWING NO
	27
SUB TOTAL	GRAND TOTAL
DATE	--

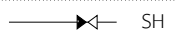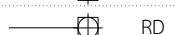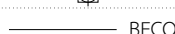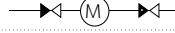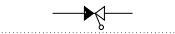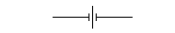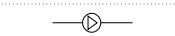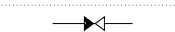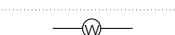รายการประกอบแบบ งานระบบสุขาภิบาล								ชื่อโครงการ		
								โครงการก่อสร้าง อาคารพักอาศัย คสล. 1 ชั้น		
								เจ้าของโครงการ		
								คุณปรินทร์ เรืองรัตนวานิช		
								สถาปนิก		
								นายนิกร สุขแสง ภสธ.10581 ถ.แจ้งวัฒนะซอย6 แขวงตลาดบางเขน. เขตหลักสี่. กรุงเทพฯ		
								วิศวกรโครงสร้าง		
								นายปฐวี เชื้อชม ภย.33663 92 ม. 1 ต.ท่าโพธิ์ศรี อ.เดชอุดม จ.อุบลราชธานี		
								วิศวกรไฟฟ้า		
								-		
								วิศวกรเครื่องกล		
								-		
								ผู้เขียน		
								นายปฐวี เชื้อชม ภย.33663 92 ม. 1 ต.ท่าโพธิ์ศรี อ.เดชอุดม จ.อุบลราชธานี		
								ที่ตั้ง		
								บ้านไม้จ้าว ตำบล ป่าตอง อำเภอ กะตุ จังหวัด ภูเก็ต		
								แบบแสดง		
								รายการประกอบแบบสุขาภิบาล		
ข้อกำหนดทั่วไปในการเดินท่อ				ข้อกำหนดและสัญลักษณ์				ตารางขนาดท่อสำหรับสุขภัณฑ์ที่มีระบุในแบบ		
ข้อกำหนดทั่วไปในการเดินท่อ				สัญลักษณ์	คำอธิบาย	ตัวย่อ	ชนิดสุขภัณฑ์	ท่อน้ำเย็น-น้ำร้อน	ท่อระบายน้ำ	ท่อระบายอากาศ
ก. การเดินท่อ S, W & V ในห้องน้ำชุดต่างๆให้เป็นไปดังต่อไปนี้ 1. การเดินท่อ S , W & V ให้เป็นไปตามตัวอย่างการเดินท่อของห้องน้ำชุดต่างๆ ดังแสดงในแบบขยาย 2. สำหรับชุดห้องน้ำที่ไม่มีตัวอย่างการเดินท่อ S , W & V ต้องเดินให้ถูกต้องตามหลักวิชาการ และมาตรฐานการเดินท่อกายในอาคารของ วสท. ข. การเดินท่อ CW ในห้องน้ำชุดต่างๆ ให้เป็นดังต่อไปนี้ 1. การเดินท่อ CW ให้เป็นไปตามตัวอย่างการเดินท่อของห้องน้ำชุดต่างๆ ดังแสดงในแบบขยาย 2. มี AIR CHAMBER สูงอย่างน้อย 0.30 ม. ติดตั้งเหนือท่อ CW ในแนวตั้งทุกจุด 3. ท่อ CW ที่จ่ายน้ำเข้าเครื่องสุขภัณฑ์ให้เดินในแนวตั้งภายในผนัง 4. ท่อ CW ในแนวนอนให้เดินเหนือฝ้าเพดานพร้อมทำ HANGER ยึดท่อให้มั่นคง 5. ก่อนต่อท่อเข้าเครื่องสุขภัณฑ์ให้ทำการติดตั้ง STOP VALVE ทุกจุด 6.การเดินท่อน้ำร้อน (HW) ให้หุ้มฉนวนกันความร้อนตลอดความยาวท่อ				S	ท่อน้ำโสโครก	S	โถชักโครกหม้อน้ำ (WC)	1/2"	4"	2"
				W	ท่อน้ำเสียทั่วไป	W	โถปัสสาวะฟลัชวาล์ว (UR)	1/2"	2"	1 1/2"
				V	ท่อระบายอากาศ	V	อ่างล้างหน้า (LAV)	1/2"	2"	1 1/2"
				CW	ท่อน้ำใช้ หรือน้ำเย็น	CW	อ่างชักล้าง (SS)	1/2"	2"	1 1/2"
				RL	ท่อน้ำฝน	HW	อ่างอาบน้ำ (BT)	1/2"	2"	1 1/2"
					โถส้วม	WC	ฝักบัวอาบน้ำ (SH)	1/2"	2"	1 1/2"
					โถปัสสาวะ	UR	ช่องระบายน้ำที่พื้น (FD)	-	2"	1 1/2"
					อ่างล้างหน้าและอ่างล้างทั่วไป	LAV,SS	ก๊อกน้ำ (HB , FAU)	1/2"	-	-
					ฝักบัวอาบน้ำ	SH	สายชำระ (SRH)	1/2"	-	-
					ตะแกรงระบายน้ำที่พื้น	FD				
					ช่องระบายน้ำที่หลังคา	RD				
					ฝาล้างท่อนบนพื้น	BFCO				
					ฝาล้างท่อใต้พื้น	CO				
					ก๊อกล้างพื้น	FAU				
					สายชำระ	SRU				
					ก๊อกสนามชนิด BALL VALVE 3/4"	HB				
					บ่อพัก	MH				
					บ่อดักไขมัน	SMH				
					มิเตอร์ประปา	M				
					วาล์วลูกกลอย	MFV				
					ข้อต่อท่อนชนิด UNION	-				
					ท่อระบายอากาศทะลุหลังคา	VTR				
					เครื่องสูบน้ำประปา	CWP				
					วาล์วประตูน้ำ	GV				
					เครื่องคั้นน้ำร้อน	-				
					วาล์วกันน้ำย้อน CHECK VALVE	CV				
	บอลวาล์ว									
						</				

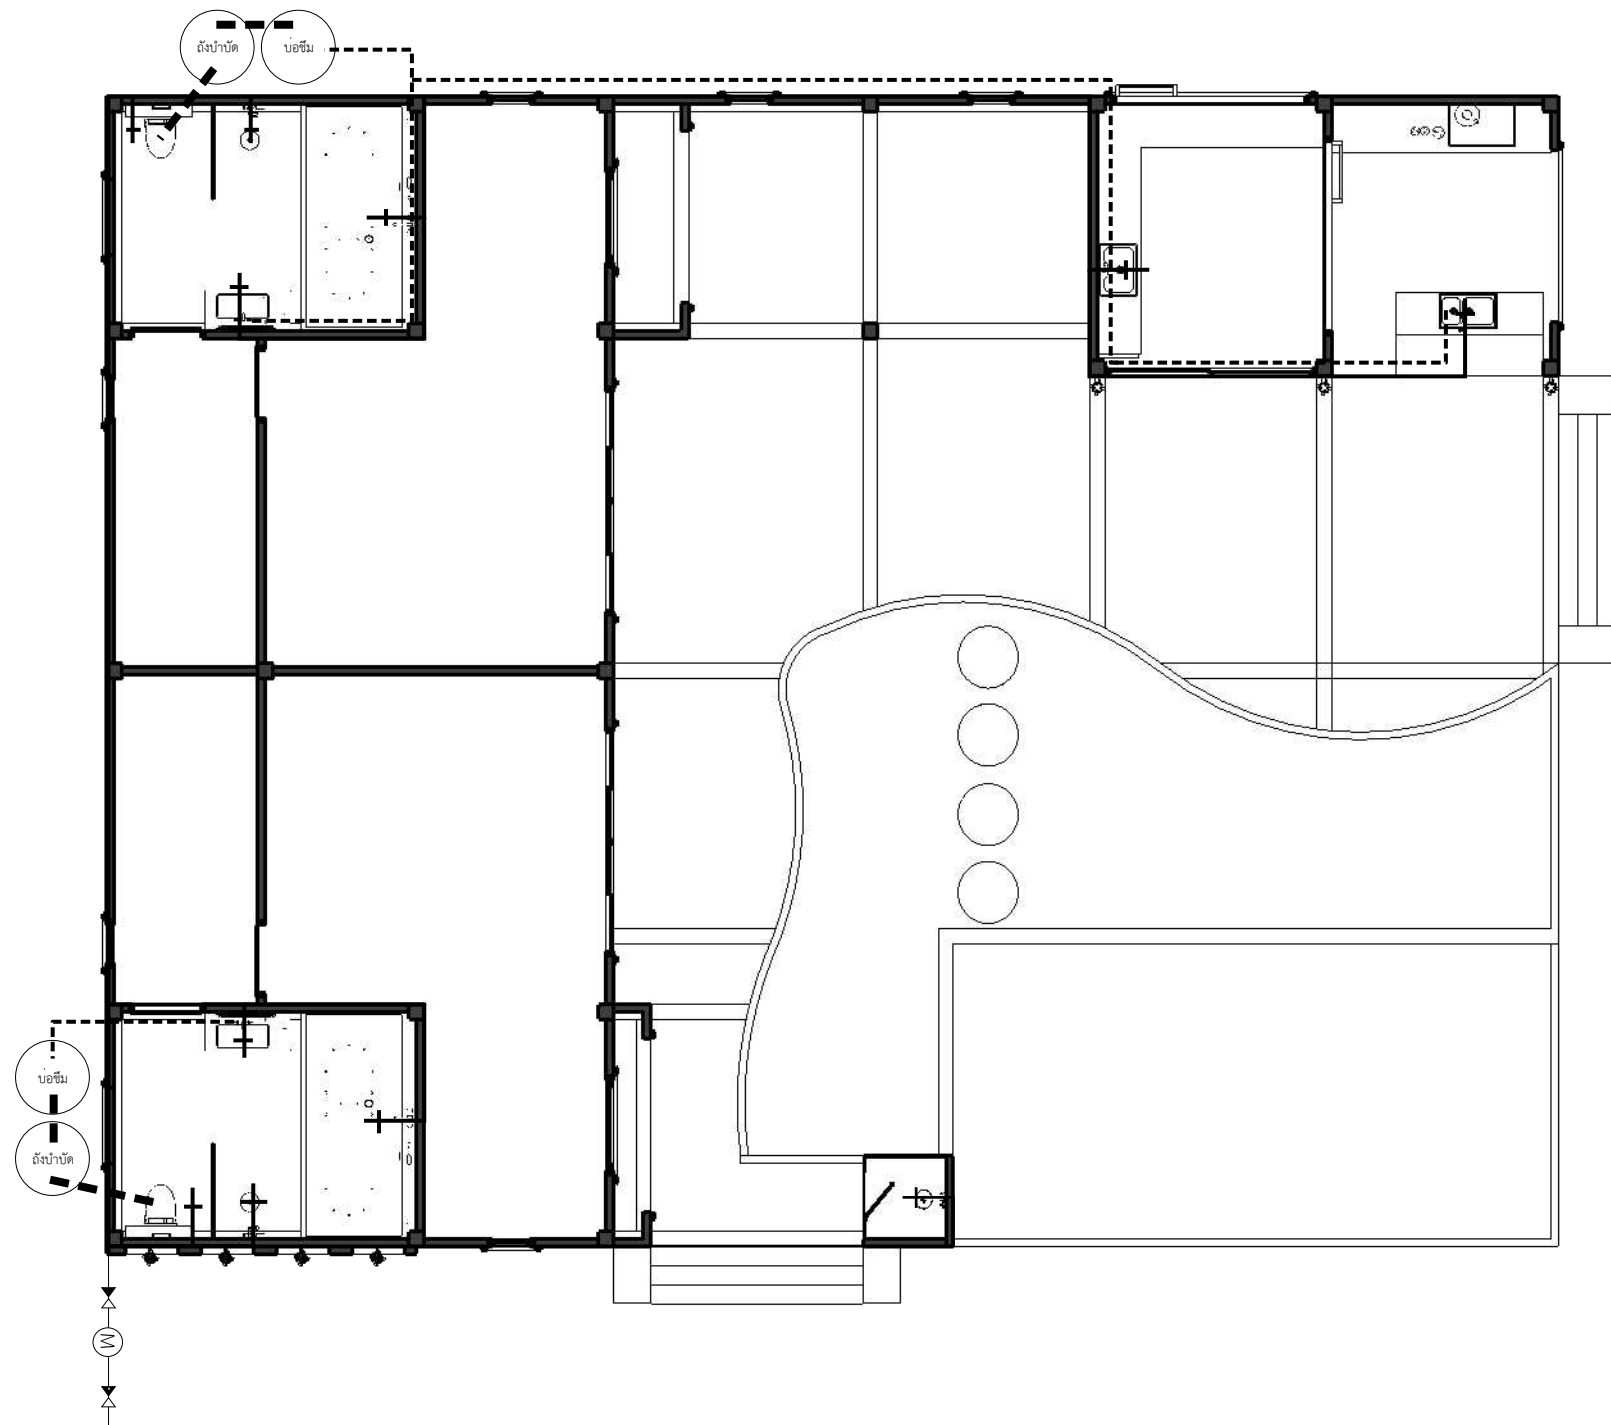

หมายเหตุ
ท่อระบายน้ำ

บ่อพักสำเร็จรูป ขนาด 0.40 x 0.40 ทุกระยะไม่เกิน 6.00 ม.
ความยาวไม่เกิน 16.00 ม.

ท่อโศโครก ท่อ PVC ขนาด 5 "

ถังบำบัด ดูแบบขยาย


CH.THANAKRIT DESIGN
081-387-9527
ID LINE : jp_pt_

Drawing Title :: ชั้น 1 Sanitary
scale: 1 : 75

SN
01



ชื่อโครงการ	
โครงการก่อสร้าง อาคารพักอาศัย คสล. 1 ชั้น	
เจ้าของโครงการ	
คุณปรินทร์ เรืองรัตนวานิช	
สถาปนิก	
..... นายนิกร สุขแสง ภสธ.10581 ถ.แจ้งวัฒนะซอย6 แขวงตลาดบางเขน. เขตหลักสี่. กรุงเทพฯ	
วิศวกรโครงสร้าง	
..... นายปฐวี เชื้อชม ภย.33663 92 ม. 1 ต.ท่าโพธิ์ศรี อ.เดชอุดม จ.อุบลราชธานี	
วิศวกรไฟฟ้า	
-	
วิศวกรเครื่องกล	
-	
ผู้เขียน	
นายปฐวี เชื้อชม ภย.33663 92 ม. 1 ต.ท่าโพธิ์ศรี อ.เดชอุดม จ.อุบลราชธานี	
ที่ตั้ง	
บ้านไม้จ้าว ตำบล ป่าตอง อำเภอ กะทู้ จังหวัดภูเก็ต	
แบบแสดง	
แปลนสุขาภิบาล	
FILE NO	DRAWING NO
	29
SUB TOTAL	GRAND TOTAL
DATE	--

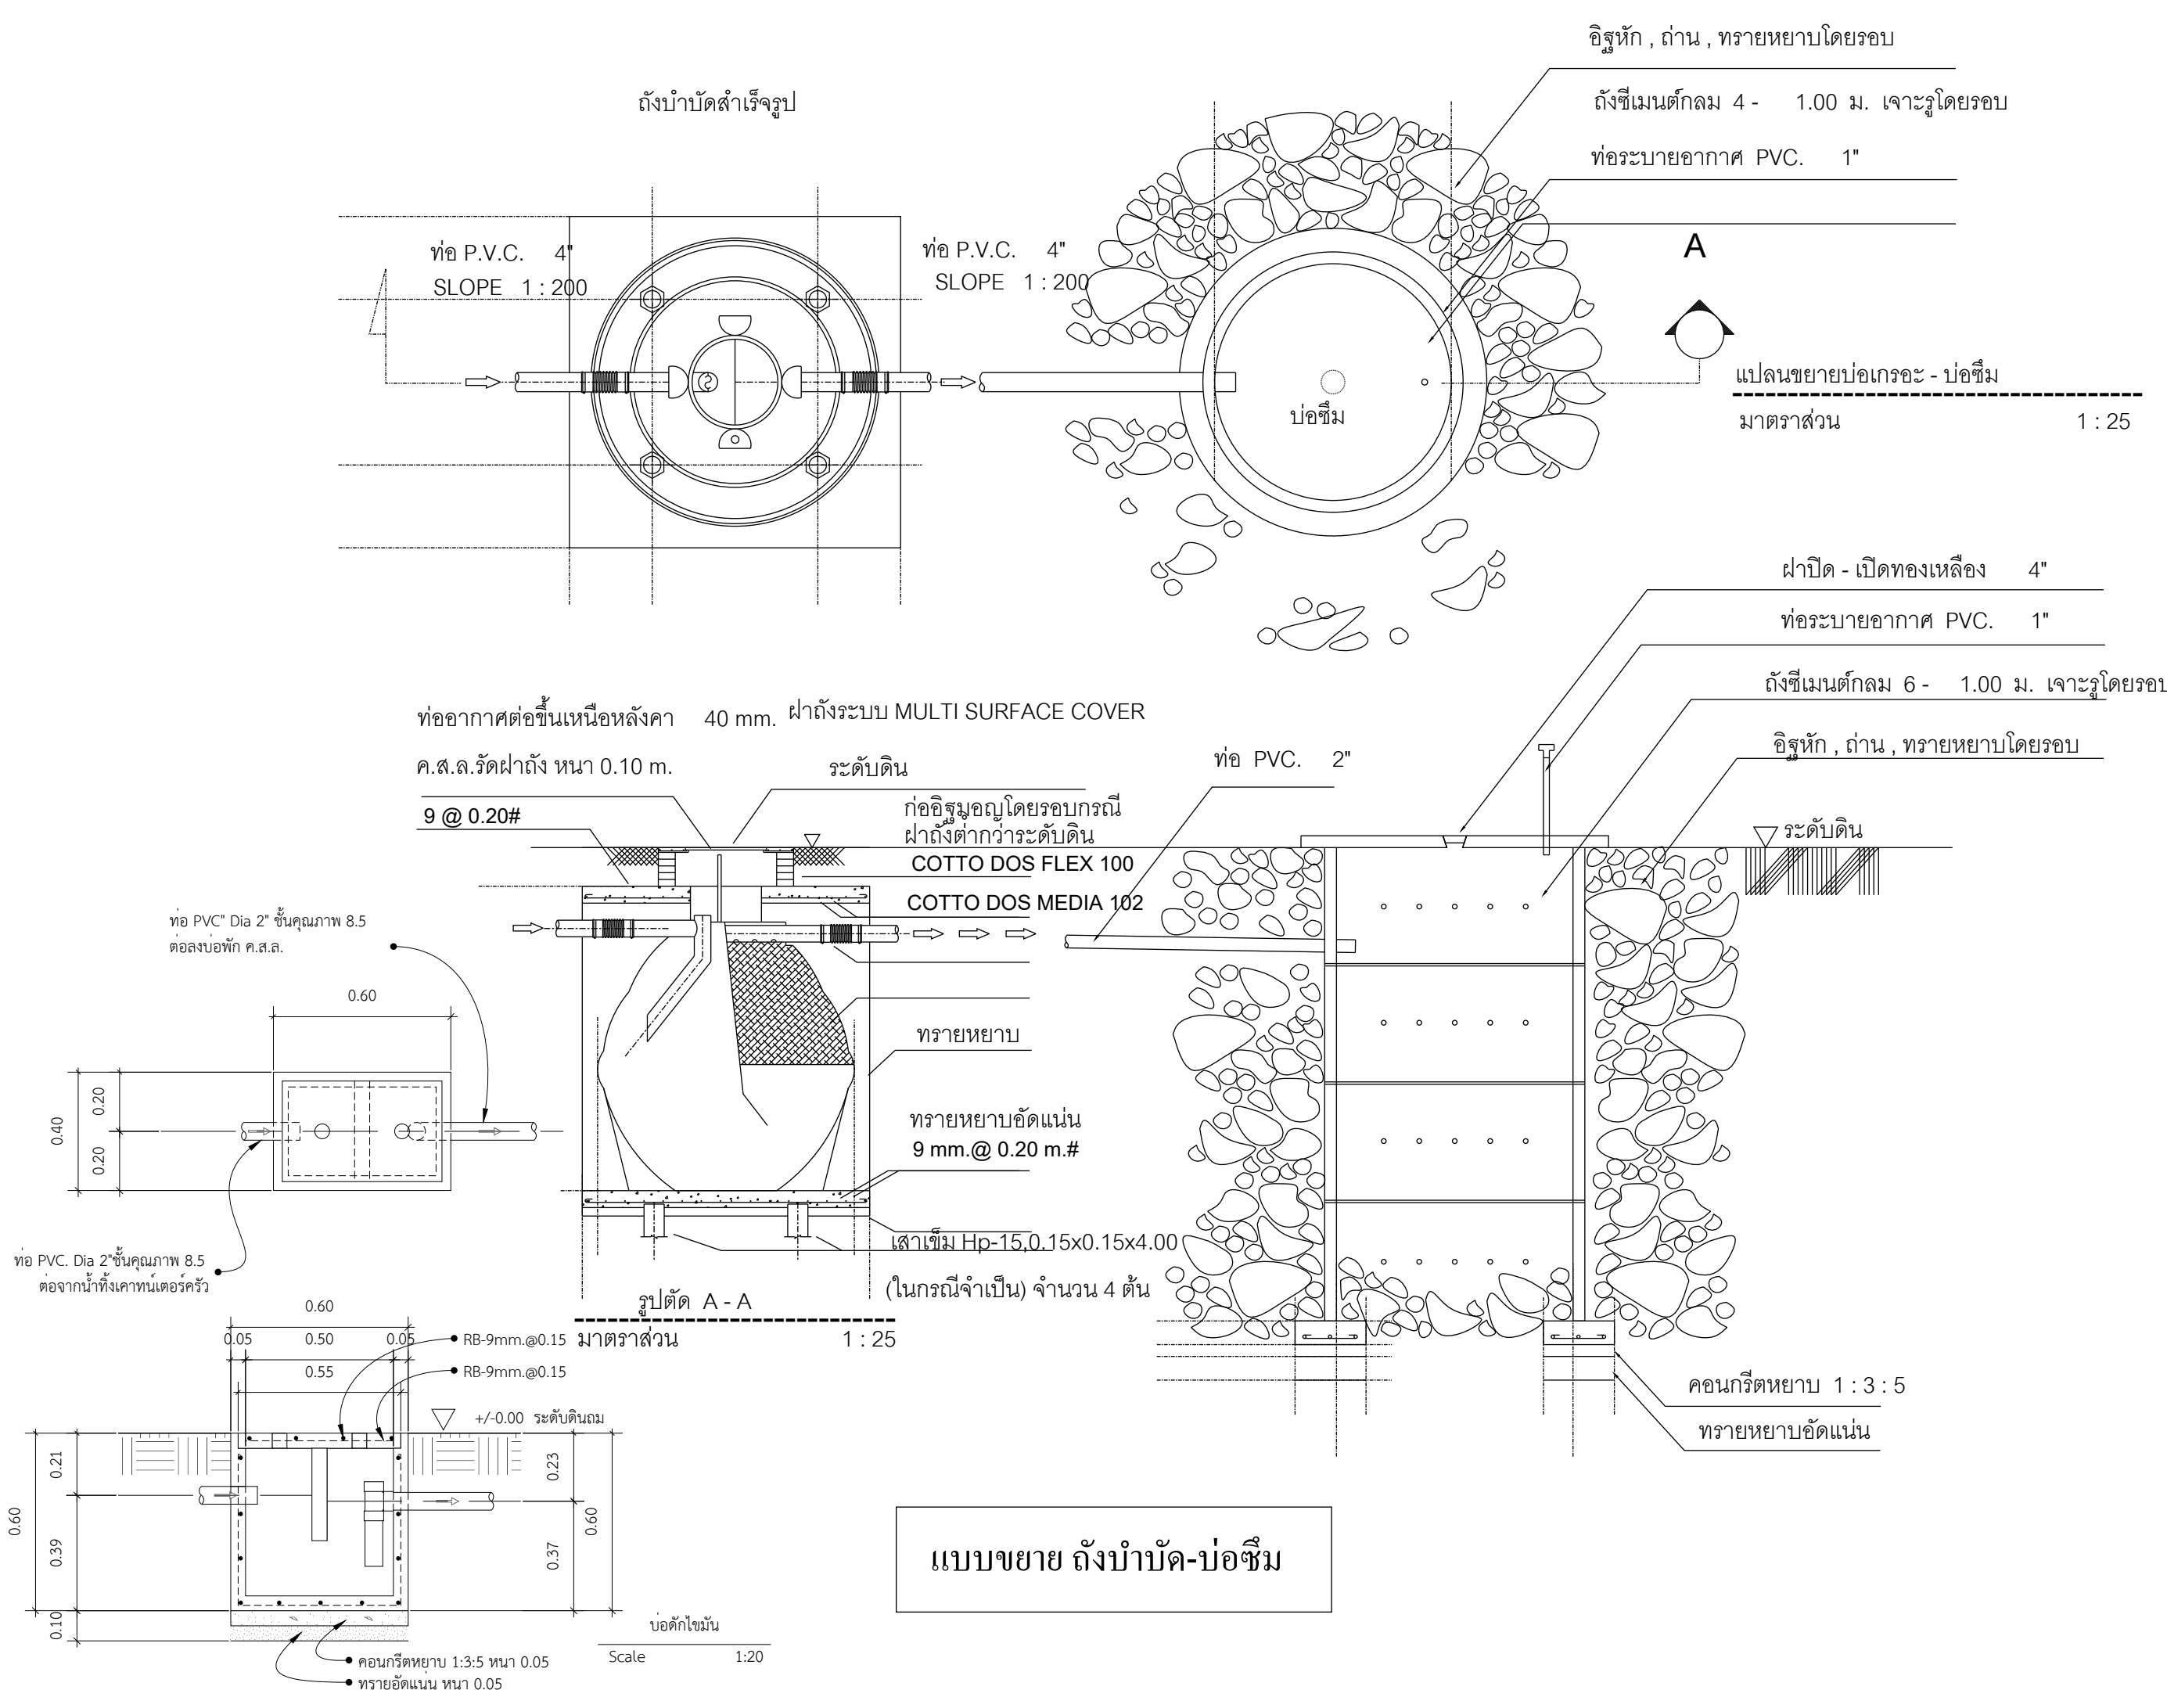

ชื่อโครงการ	
โครงการก่อสร้างอาคารพักอาศัย	
คสล. 1 ชั้น	
เจ้าของโครงการ	
คุณปรีนทร เรืองรัตนวานิช	
สถาปนิก	
นายนิกร สุขแสง ภสธ.10581 ถ.แจ้งวัฒนะซอย6 แขวงตลาดบางเขน. เขตหลักสี่. กรุงเทพฯ	
วิศวกรโครงสร้าง	
นายปฐวี เชื้อชม ภย.33663 92 ม. 1 ต.ท่าโพธิ์ศรี อ.เดชอุดม จ.อุบลราชธานี	
วิศวกรไฟฟ้า	
วิศวกรเครื่องกล	
ผู้เขียน	
นายปฐวี เชื้อชม ภย.33663 92 ม. 1 ต.ท่าโพธิ์ศรี อ.เดชอุดม จ.อุบลราชธานี	
ที่ตั้ง	
บ้านไม้จ้าว ตำบล ป่าตอง อำเภอ กะตุ จังหวัด ภูเก็ต	
แบบแสดง	
ขยายถังน้ำบาด-บ่อพัก	
FILE NO	DRAWING NO
	30
SUB TOTAL	GRAND TOTAL
DATE	--

ของอเหล็กปลอก (ดูรายละเอียด ก)



เหล็กเสริมตามยาว
มีเส้นผ่านศูนย์กลาง
ไม่น้อยกว่า 12 มม.
จำนวนไม่น้อยกว่า
๔ เส้น

ตัด ① - ①

รูปที่ 15 ตัวอย่างการเสริมเหล็กในเสา


ตัวอย่างการเสริมเหล็กในคาน

Technical drawing of a reinforced concrete beam cross-section showing reinforcement layout. The drawing includes dimensions for the distance between stirrups (80 cm), the distance between longitudinal bars (10 cm), and the distance between the top and bottom bars (20 cm). It also shows the placement of stirrups and longitudinal bars, and the location of the reinforcement cage.


ของอเหล็กปลอก (ดูรายละเอียด ข)
เหล็กเสริมตามยาว
มีเส้นผ่านศูนย์กลาง
ไม่น้อยกว่า 12 มม.
จำนวนไม่น้อยกว่า
4 เส้น

รูปตัด ② - ②

รูปที่ 16 ตัวอย่างการเสริมเหล็กในคาน

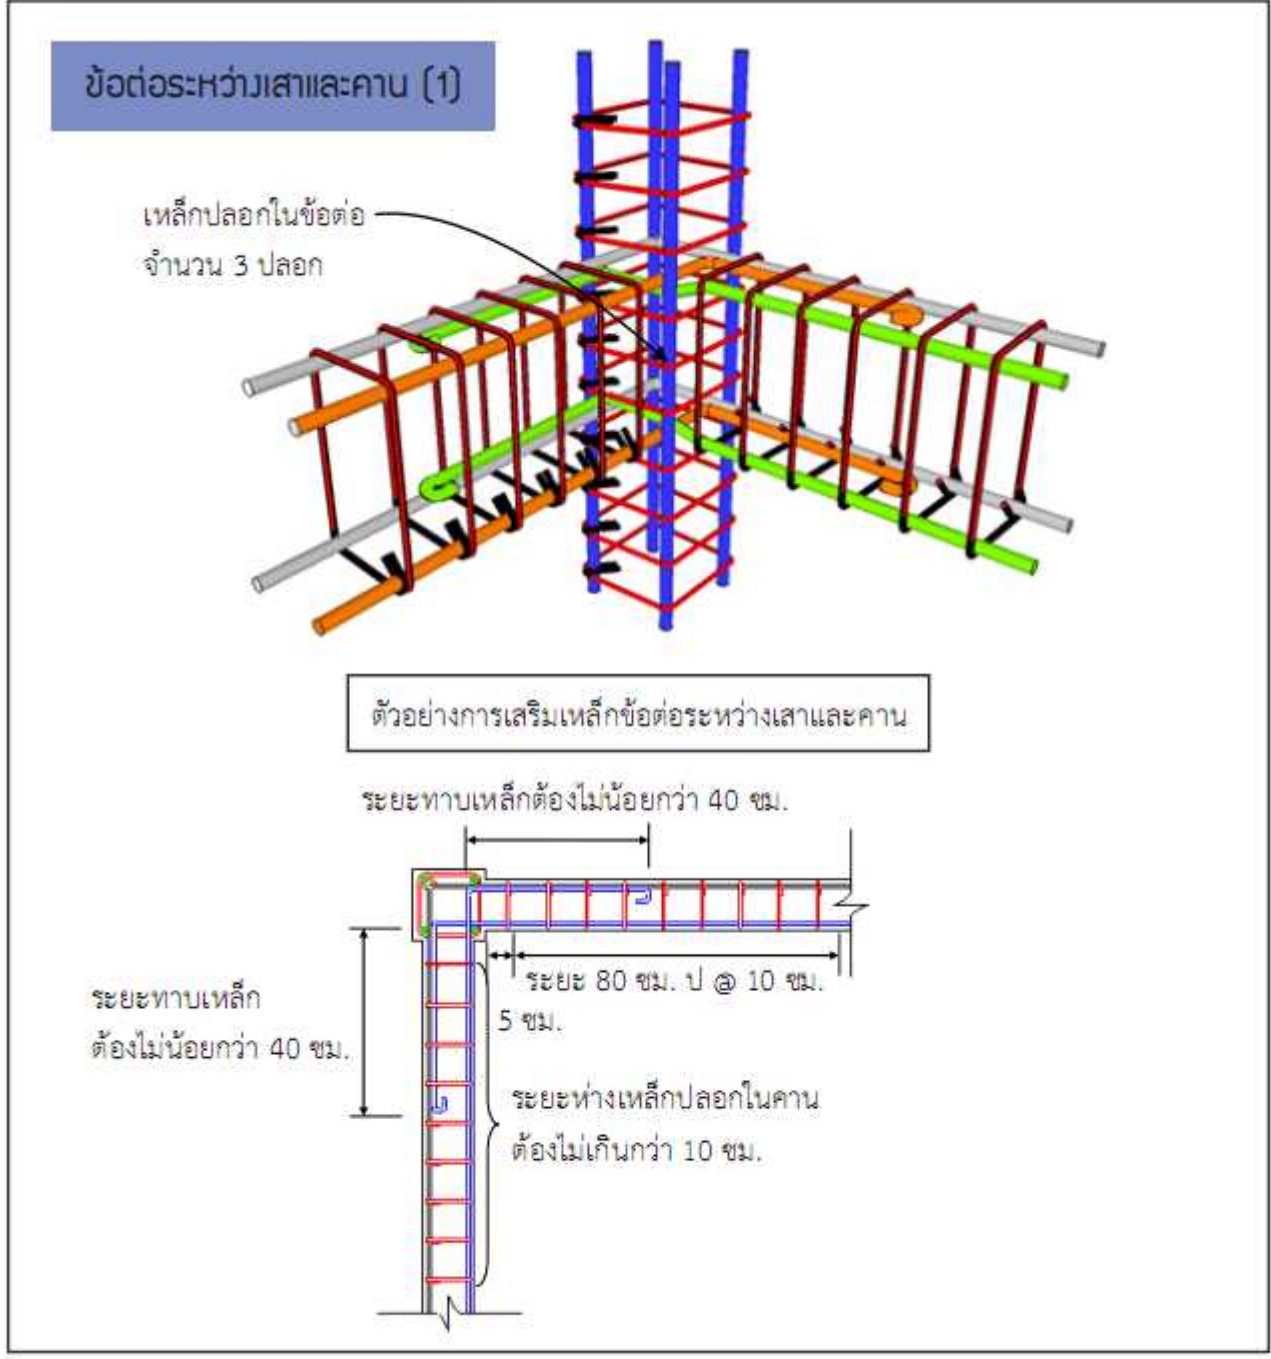

รูปที่ 17 ตัวอย่างรายละเอียดการเสริมเหล็กบริเวณข้อต่อระหว่างเสาและคาน

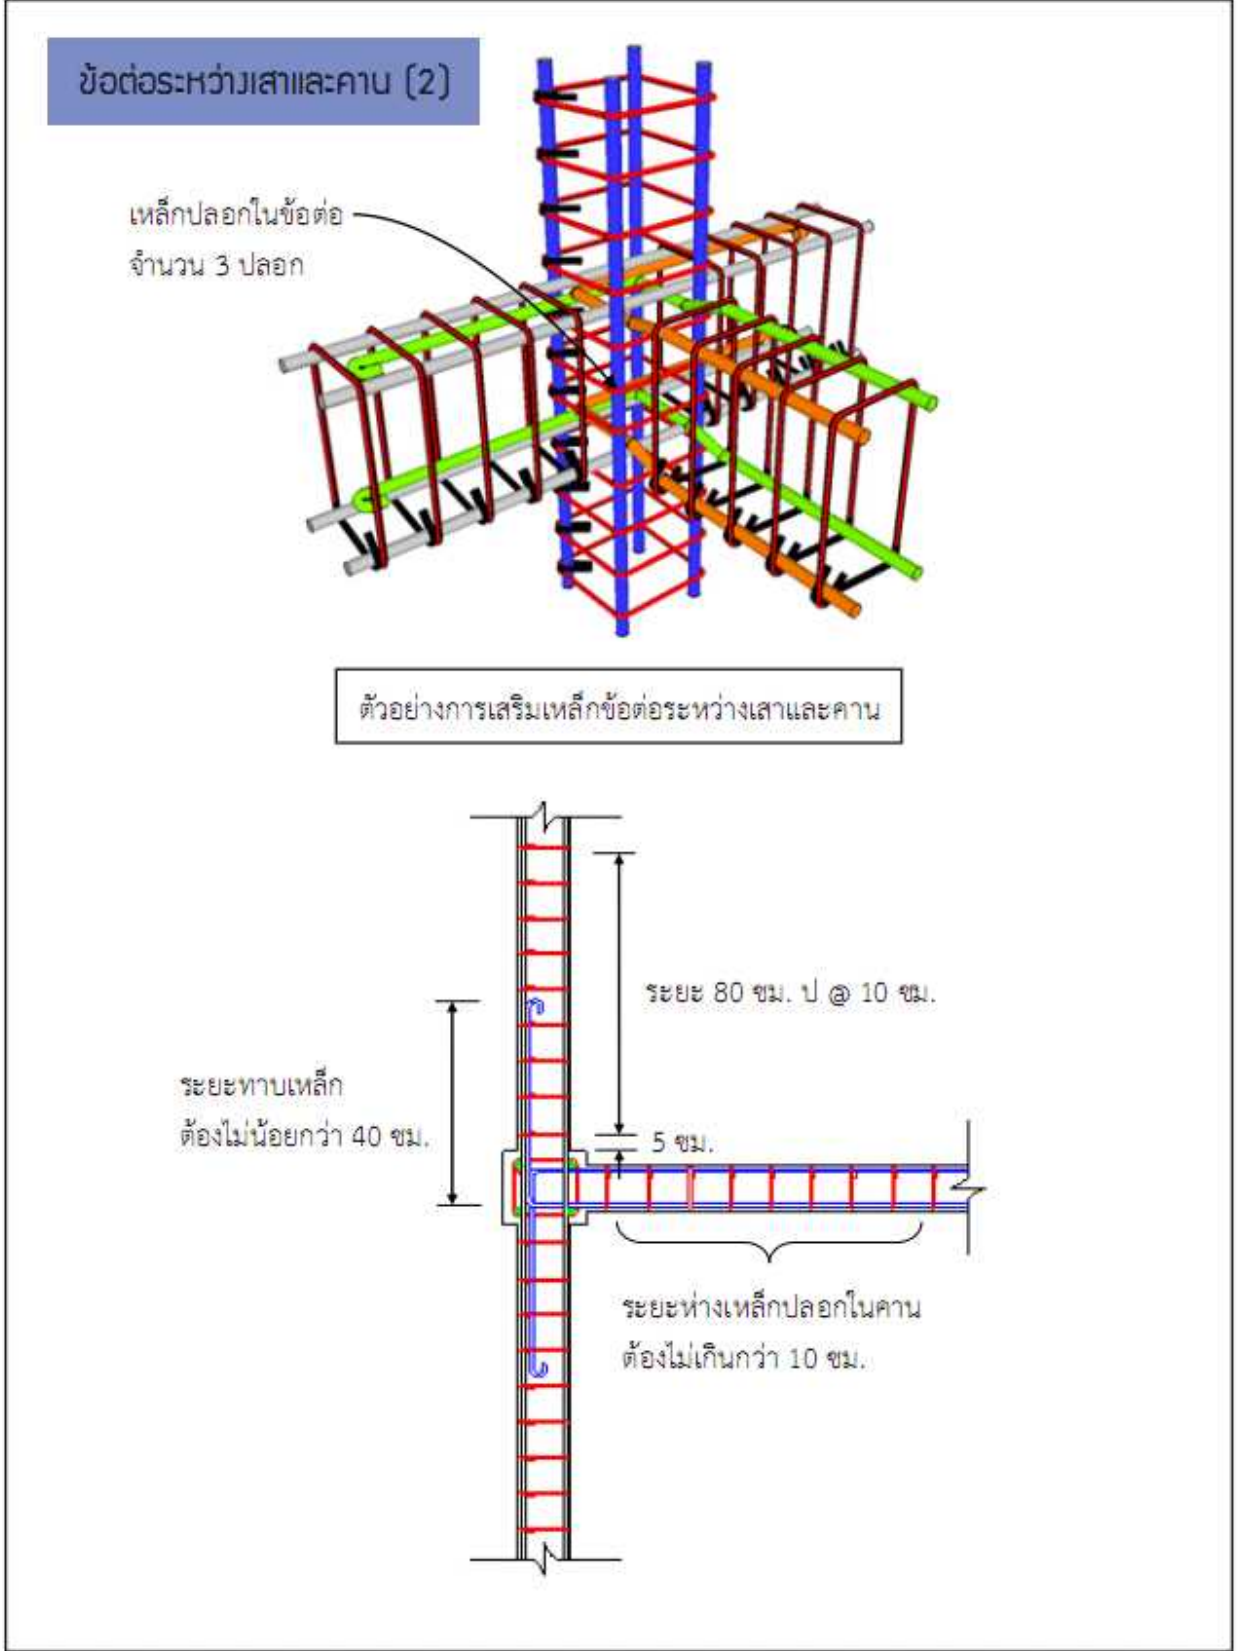

รูปที่ 18 ตัวอย่างรายละเอียดการเสริมเหล็กบริเวณข้อต่อระหว่างเสาและคาน